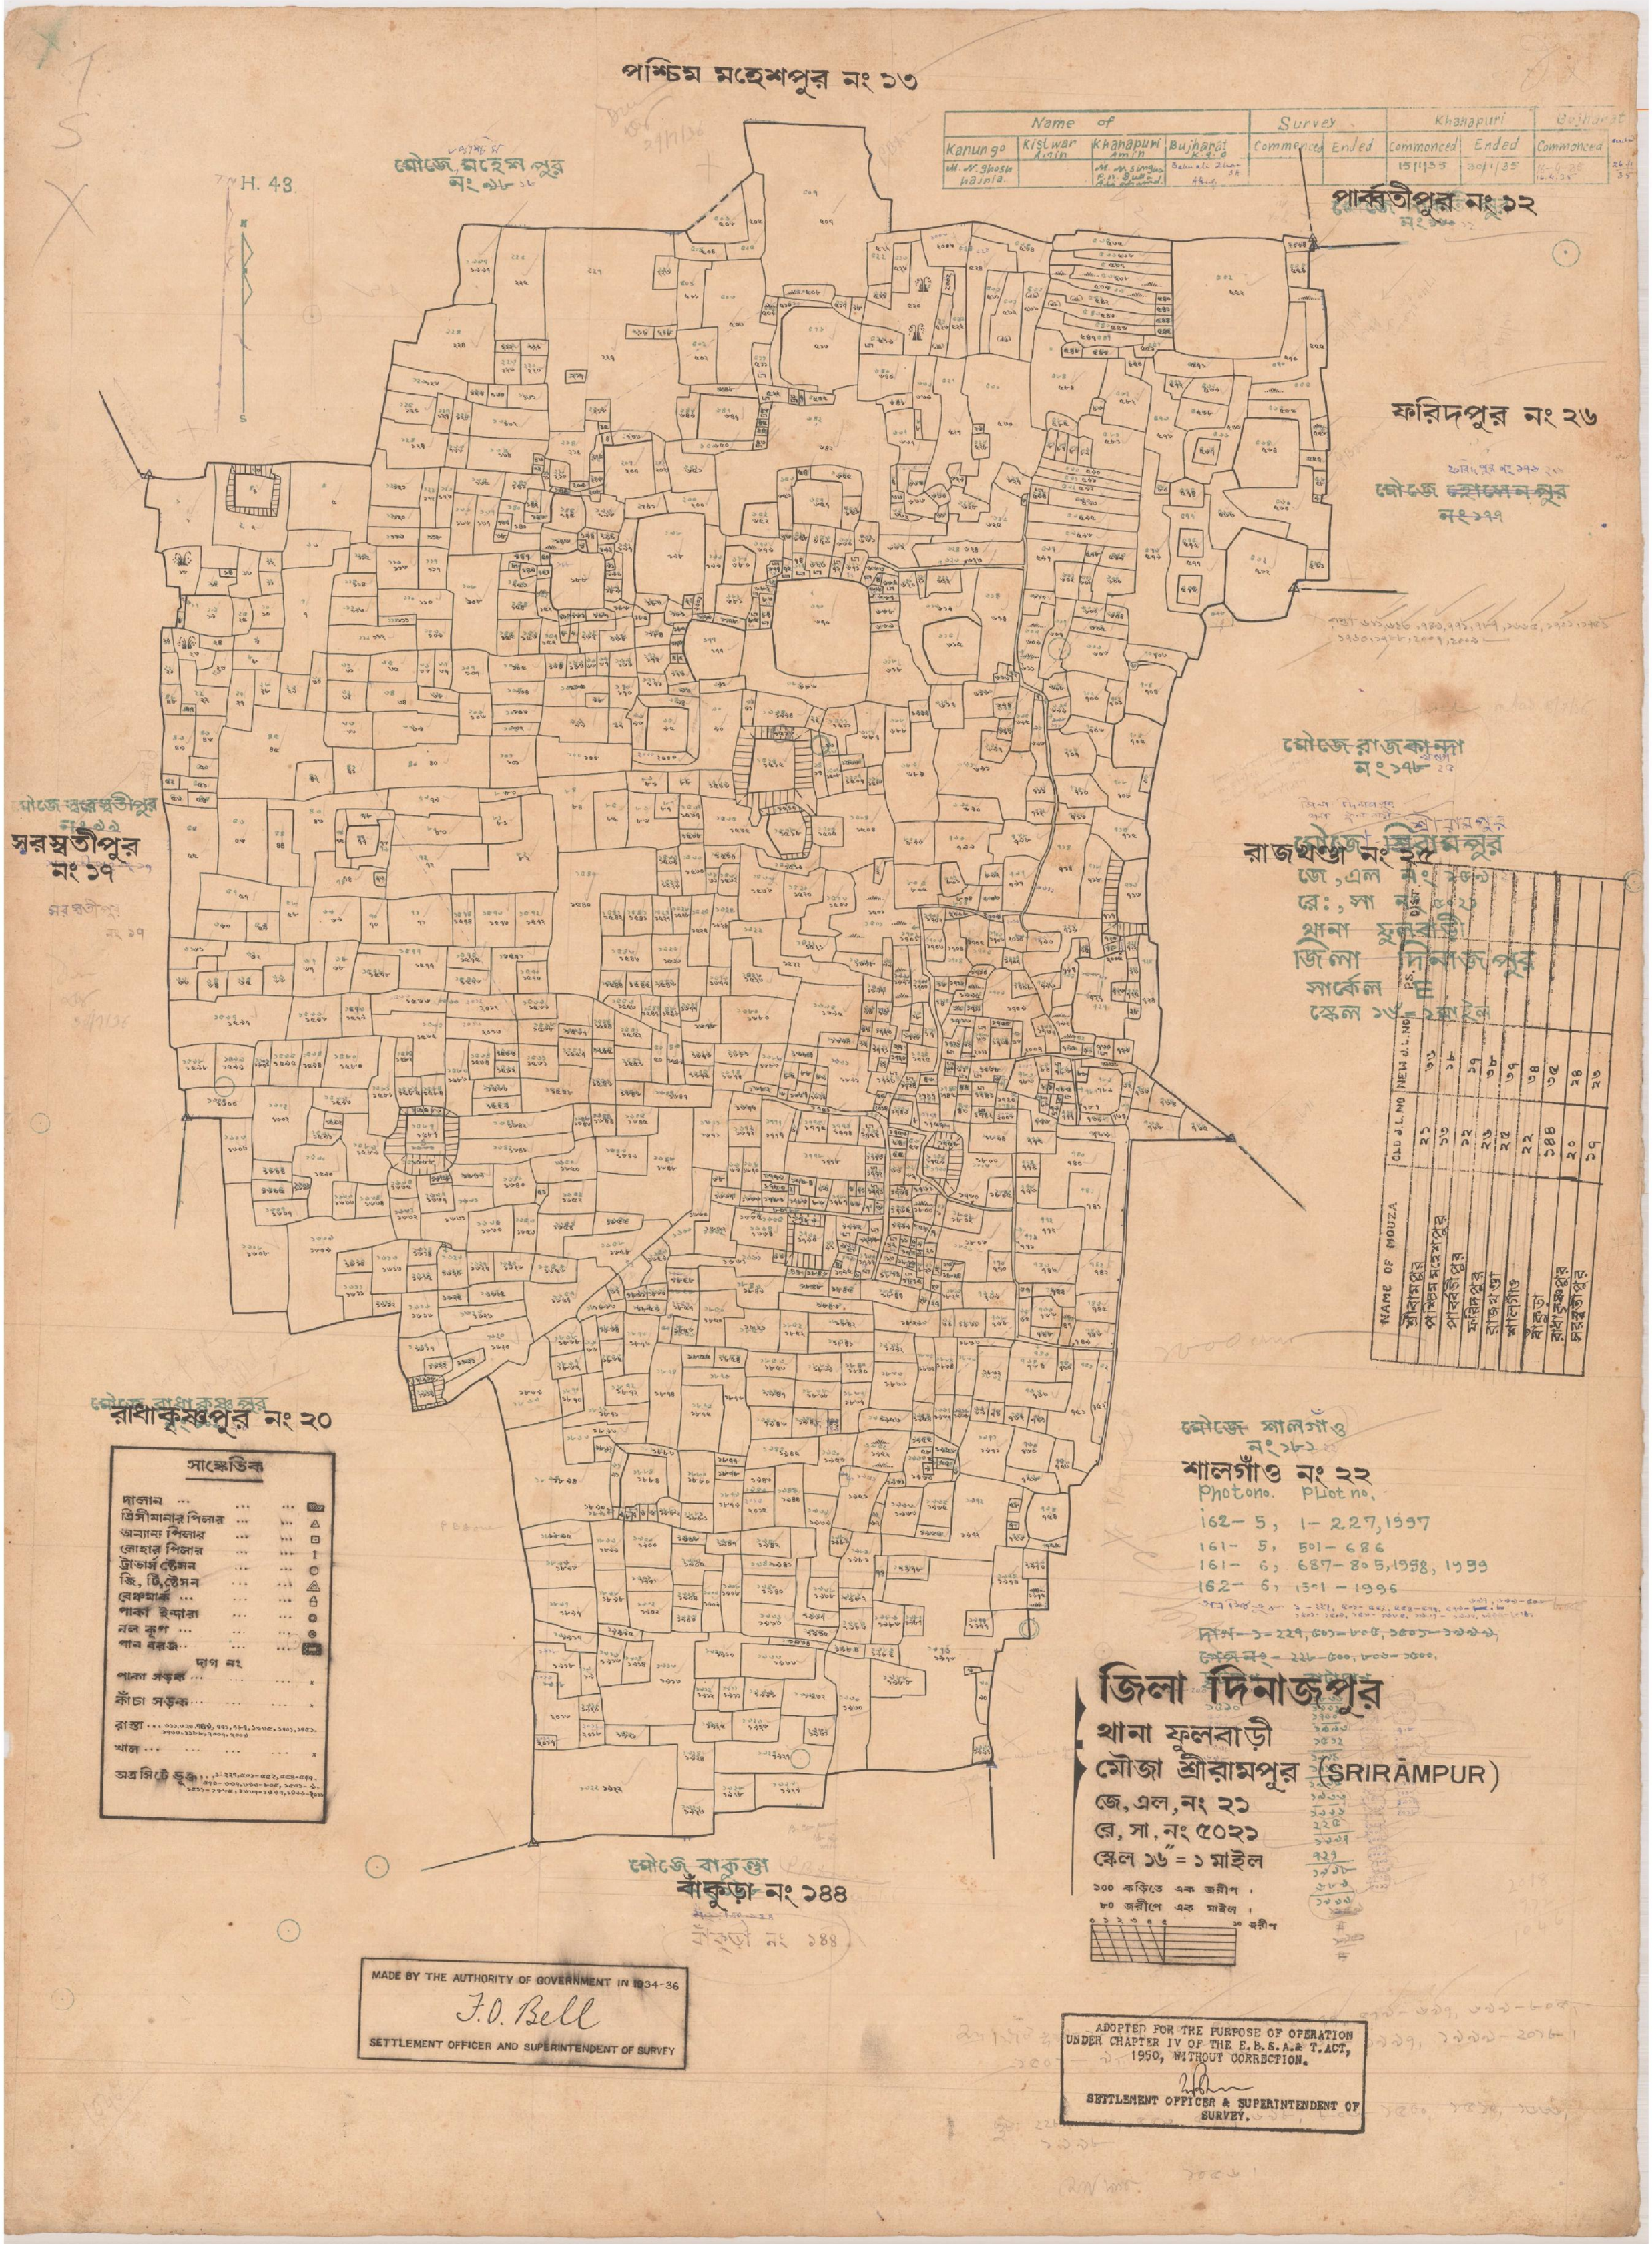
পশ্চিম মহেশপুর নং ১৩
H. 43.
মৌজে মহেশপুর নং ১৮
পার্ব্বতীপুর নং ১২
ফরিদপুর নং ২৬
মৌজে রাজকান্দা নং ১৭৮
মৌজে শ্রীরামপুর
রাজথণ্ডা নং ২৫
জে, এল নং ২১
রে, সা নং ৫০২১
থানা ফুলবাড়ী
জিলা দিনাজপুর
সার্কেল
স্কেল ১৬" = ১ মাইল
মৌজে সরস্বতীপুর
সরস্বতীপুর নং ১৭
মৌজে রাধাকৃষ্ণপুর
রাধাকৃষ্ণপুর নং ২০
মৌজে শালগাঁও নং ১৮১
শালগাঁও নং ২২
Photo no. Plot no.
162- 5, 1- 227, 1997
161- 5, 501- 686
161- 6, 687- 805, 1998, 1999
162- 6, 1501 - 1996
জিলা দিনাজপুর
থানা ফুলবাড়ী
মৌজা শ্রীরামপুর (SRIRAMPUR)
জে, এল, নং ২১
রে, সা, নং ৫০২১
স্কেল ১৬" = ১ মাইল
২০০ কড়িতে এক জরীপ ।
৮০ জরীপে এক মাইল ।
০ ১ ২ ৩ ৪ ৫ ১০ জরীপ
সাঙ্কেতিক
দালান
ত্রিসীমানার পিলার
অন্যান্য পিলার
লোহার পিলার
ট্রাভার্স ষ্টেসন
জি, টি, ষ্টেসন
বেঞ্চমার্ক
পাকা ইন্দারা
নল কূপ
পান বরজ
দাগ নং
পাকা সড়ক
কাঁচা সড়ক
রাস্তা
খাল
অত্র সিটে ভুক্ত
মৌজে বাকুণ্ডা
বাঁকুড়া নং ১৪৪
Name of
Kanungo: M. N. Ghosh, Najnia.
Kistwar Amin
Khanapuri Amin: M. M. Singha, R. N. Gupta, Abu Ahmed.
Bujharat K.G.: Salimali Sikder, Abul
Survey: Commenced / Ended
Khanapuri: Commenced 15/1/35, Ended 30/1/35
Bujharat: Commenced 16-9-35, 16.4.35
NAME OF MOUZA
OLD J.L. NO
NEW J.L. NO
শ্রীরামপুর
পশ্চিম মহেশপুর
পার্ব্বতীপুর
ফরিদপুর
রাজথণ্ডা
শালগাঁও
বাঁকুড়া
রাধাকৃষ্ণপুর
সরস্বতীপুর
MADE BY THE AUTHORITY OF GOVERNMENT IN 1934-36
F.O. Bell
SETTLEMENT OFFICER AND SUPERINTENDENT OF SURVEY
ADOPTED FOR THE PURPOSE OF OPERATION UNDER CHAPTER IV OF THE E.B.S.A.& T.ACT, 1950, WITHOUT CORRECTION.
SETTLEMENT OFFICER & SUPERINTENDENT OF SURVEY.