Kanungo	Kistwar Amin	Khanapuri Amin	Panjhabat Kanungo	Survey Commenced	Survey Ended	Khanapuri Commenced	Khanapuri Ended	Panjhabat Commenced	Panjhabat Ended
Kamalla	Rahen Uddin Mia	Rahen Uddin Mia	Abdul Gani S.D.	1-5-35	5-2-35	7-2-35	1-5-35	25-5-35	31-5-35
1	2	3	4	5	6	7	8	9	10

জিলা দিনাজপুর

থানা ফুলবাড়ী

মৌজা সিলাইবাড়ী (SILAIBARI)

জে. এল. নং ১৮২

রে. সা. নং ৪৭৯১

স্কেল ১৬" = ১ মাইল

১০০ কাঠিতে এক জরীপ।
৮০ জরীপে এক মাইল।

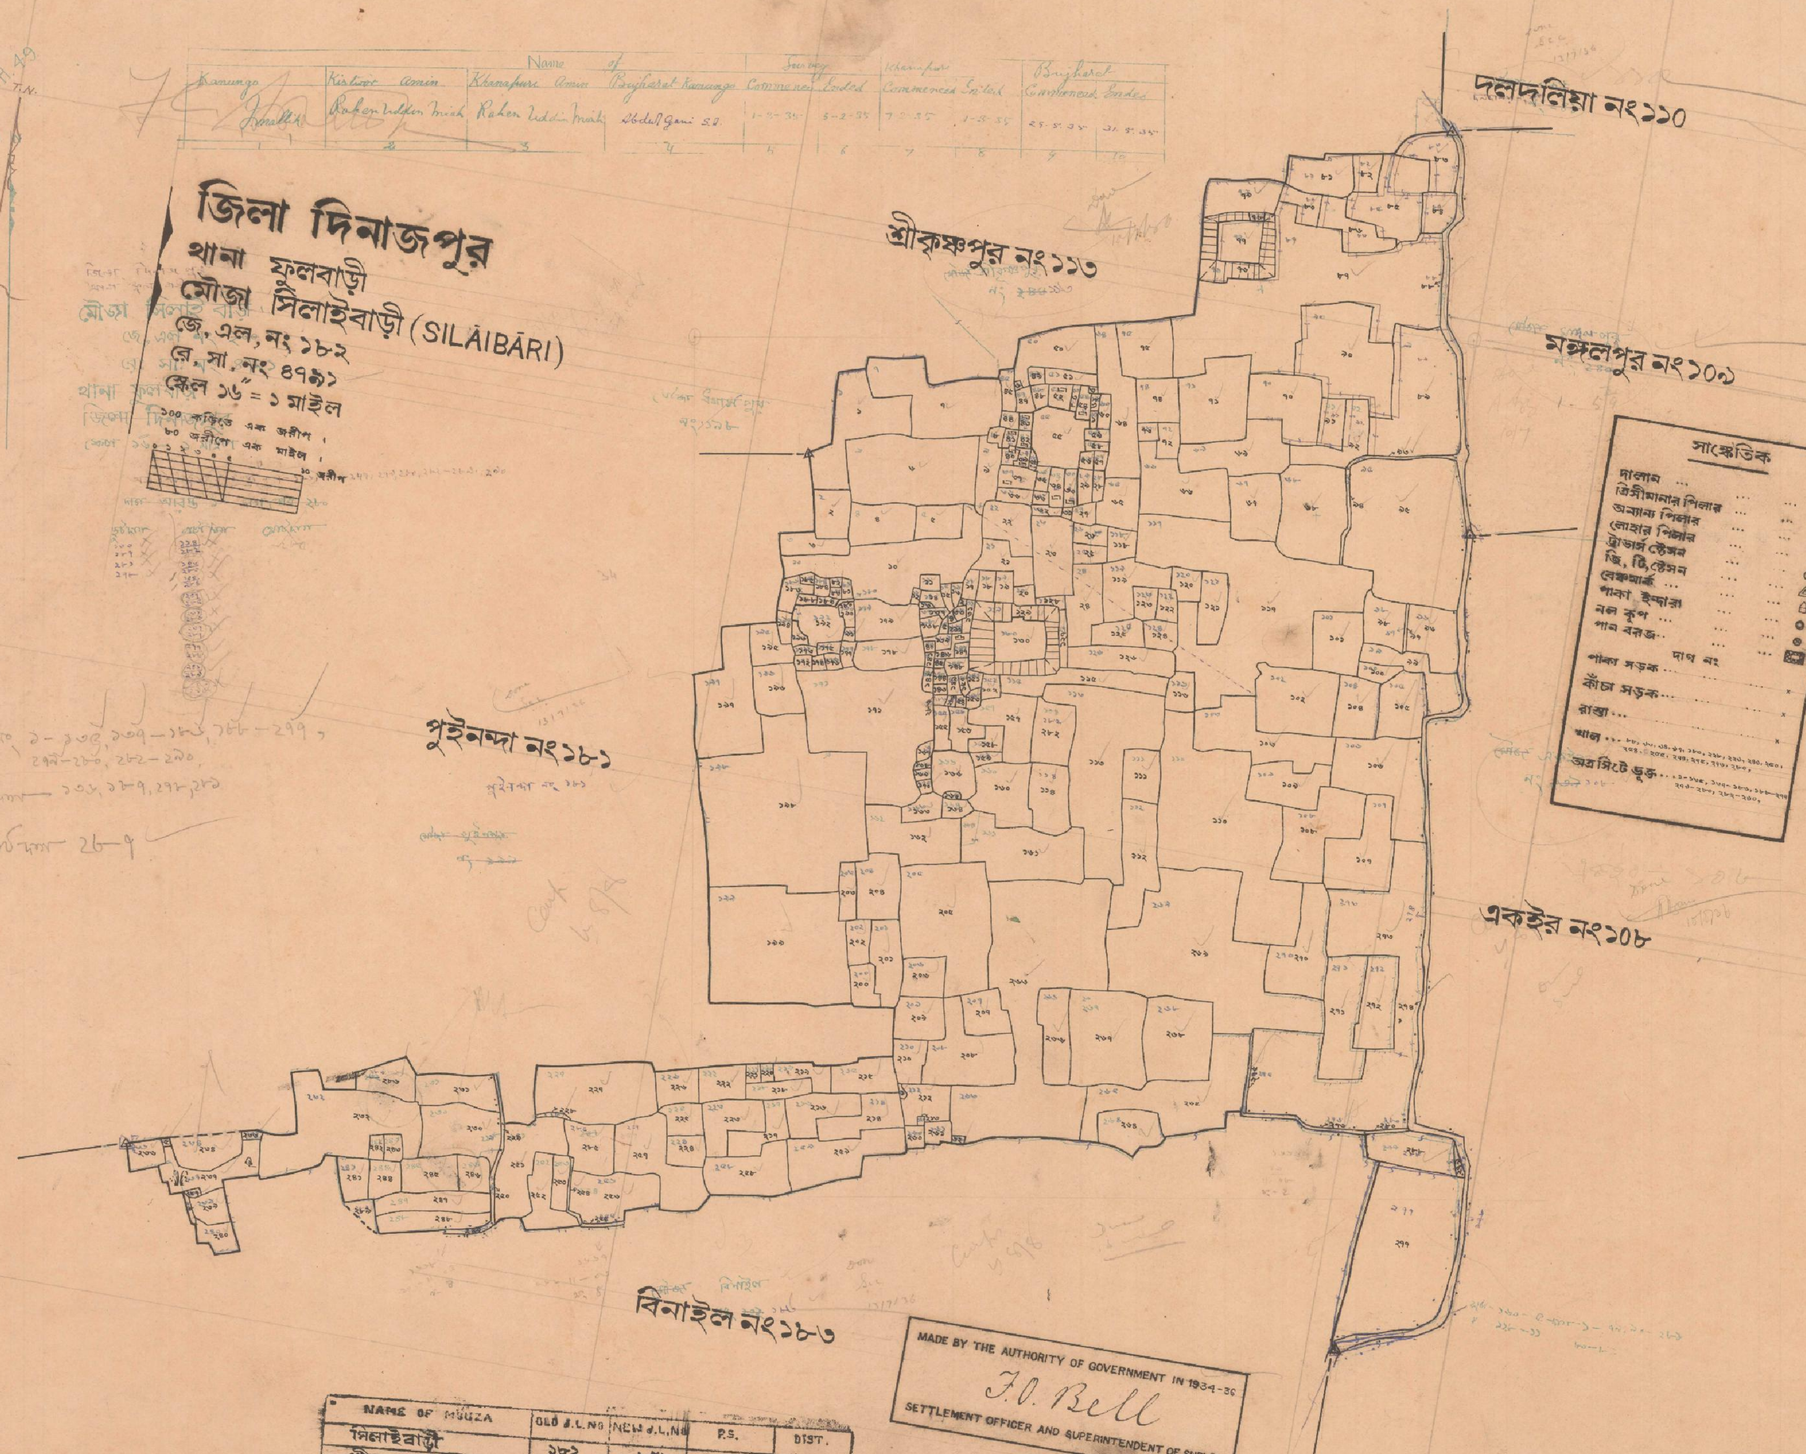

NAME OF MOUZA	OLD J.L. NO	NEW J.L. NO	P.S.	DIST.
সিলাইবাড়ী	১৮২	১৫৮		
শ্রীকৃষ্ণপুর	১১৩	১৫৯		
পুইনন্দা	১৮১	১৬৬		
বিনাইল	১৮৩	১৭৮		
একইর	১০৮	১৫৫		
মঙ্গলপুর	১০৯	১৫৭		
দলদলিয়া	১১০	১৫৬		

MADE BY THE AUTHORITY OF GOVERNMENT IN 1934-36
F. O. Bell
SETTLEMENT OFFICER AND SUPERINTENDENT OF SURVEY

ADOPTED FOR THE PURPOSE OF OPERATION UNDER CHAPTER IV OF THE B.B.S.A.& T.ACT, 1950, WITHOUT CORRECTION.
SETTLEMENT OFFICER & SUPERINTENDENT OF SURVEY.