জিলা দিনাজপুর

থানা বীরগঞ্জ

মৌজা চকপাতলা (CHAK PÀTLÀ)

জে, এল, নং ৫৫

রে, সা, নং ১৪.

স্কেল ১৬" = ১ মাইল

১০০ কড়িতে এক জরীপ ।

৮০ জরীপে এক মাইল ।

০ ১ ২ ৩ ৪ ৫ ১০ জরীপ

Survey		Khanapuri		Bujarat	
Commenced	Ended	Commenced	Ended	Commenced	Ended
		20.10.35.	31.10.35.	27-12-35	31.12.35

সাঙ্কেতিক

দালান	
ত্রিসীমানার পিলার	△
অন্যান্য পিলার	⊡
লোহার পিলার	I
ট্রাভার্স ষ্টেসন	○
জি, টি, ষ্টেসন	△
বেঞ্চমার্ক	
পাকা ইন্দারা	●
নল কূপ	G
পান বরজ	
দাগ নং	
পাকা সড়ক	×
কাঁচা সড়ক	×
রাস্তা	৯, ১০, ১৬০,
খাল	×
অত্রসিটে ভুক্ত ...	১-৪, ৬-৫৪, ৫৬, ৫৮-৮৮ ৯০-১১৪, ১১৬-১২০, ১২২-১৫৪, ১৫৬, ১৫৮-১৭০, ১৭৬-২৫০।

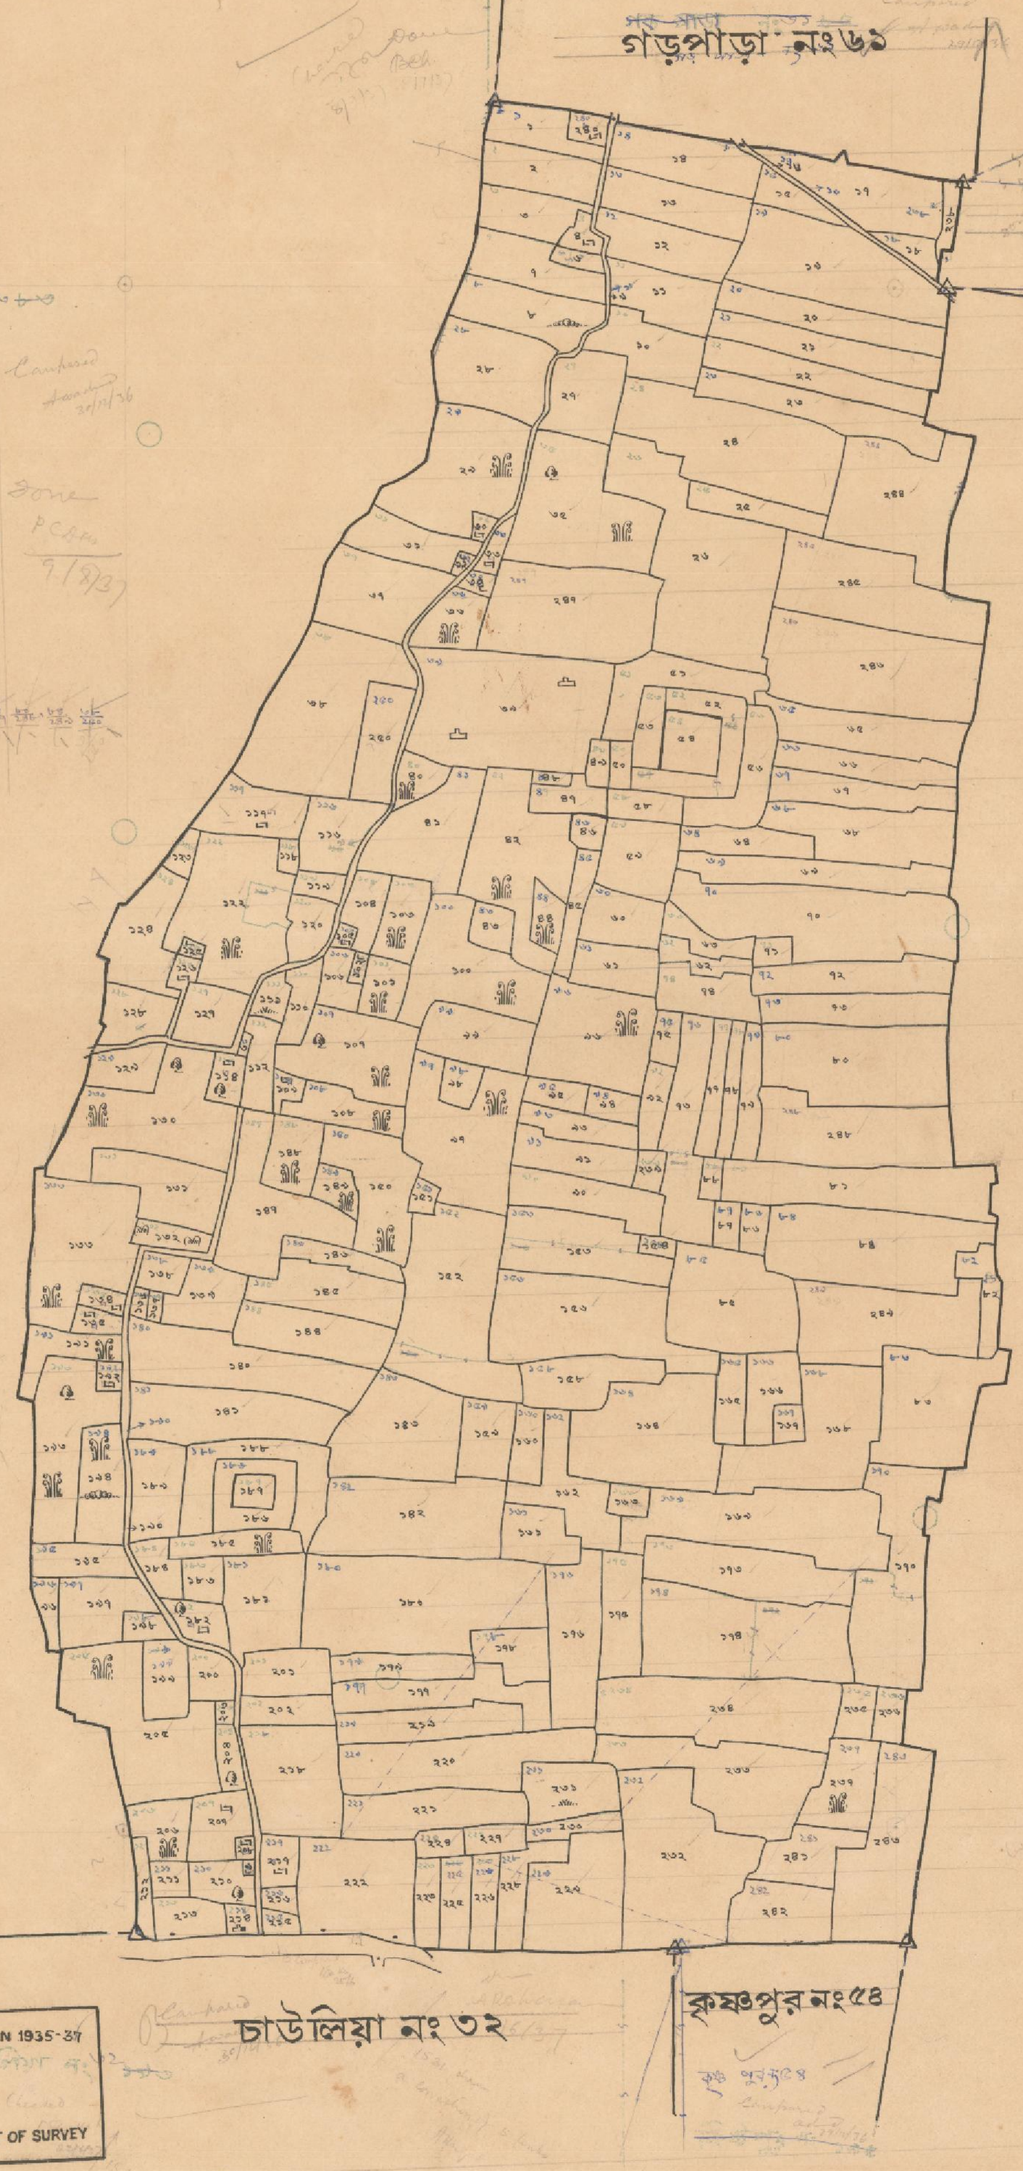

MADE BY THE AUTHORITY OF GOVERNMENT IN 1935-37

For Bell

SETTLEMENT OFFICER AND SUPERINTENDENT OF SURVEY

ADOPTED FOR THE PURPOSE OF OPERATION UNDER CHAPTER IV OF THE E.B.S.A.& T.ACT, 1950, WITHOUT CORRECTION.

SETTLEMENT OFFICER & SUPERINTENDENT OF SURVEY.