জিলা দিনাজপুর

থানা ফুলবাড়ী

মৌজা পার্ব্বতীপুর (PARBBATIPUR)

জে, এল, নং ১২

রে, সা, নং ৫০০৭

স্কেল ১৬" = ১ মাইল

১০০ কড়িতে এক জরীপ।

৮০ জরীপে এক মাইল।

Name of				Survey		Khanapuri		Bujharat	
Kanungo	Kistwari Amin	Khanapuri Amin	Bujharat Amin	Commenced	Ended	Commenced	Ended	Commenced	Ended
Sri N. Ghosh Bajria		Sri Kumar Ali Khan	Sri N. Ghosh Hajra			[illegible]	[illegible]	[illegible]	[illegible]

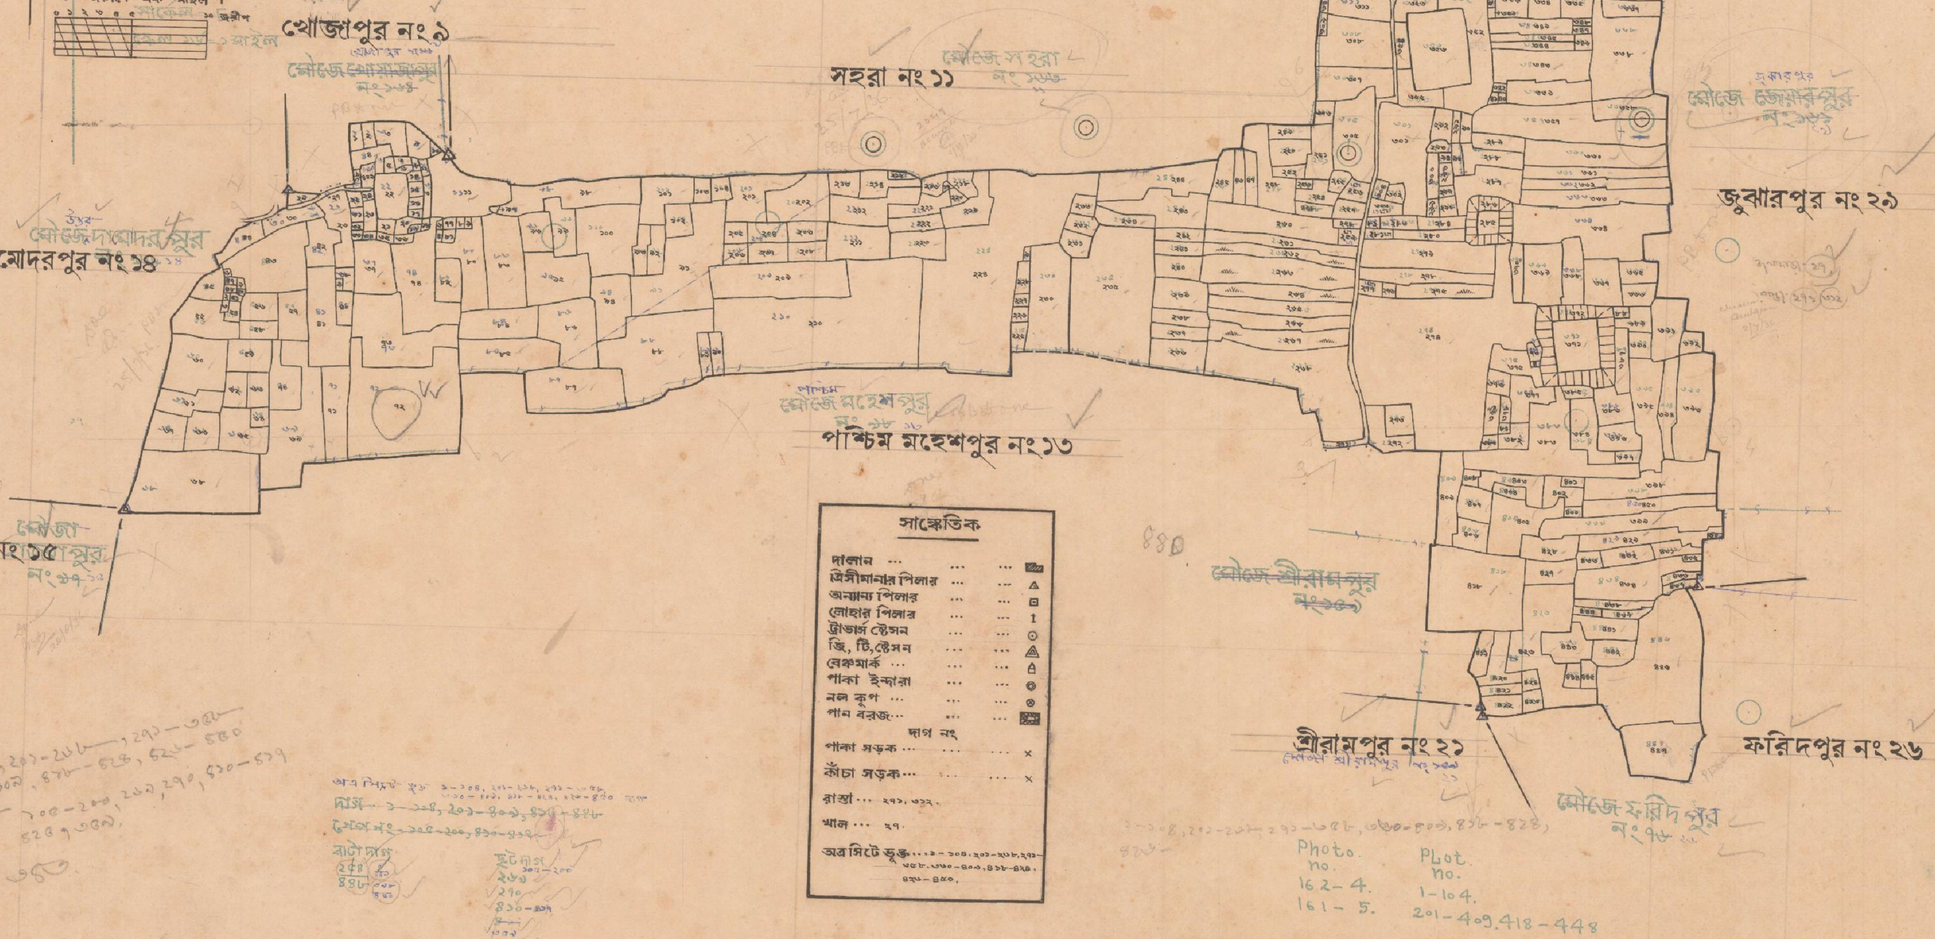

সাঙ্কেতিক

দালান ...	... ...
ত্রিসীমানার পিলার	... ...
অন্যান্য পিলার	... ...
লোহার পিলার	... ...
ট্রাভার্স ষ্টেসন	... ...
জি, টি, ষ্টেসন	... ...
বেঞ্চমার্ক ...	... ...
পাকা ইন্দারা	... ...
নল কূপ ...	... ...
পান বরজ...	... ...

দাগ নং

পাকা সড়ক ...	... ... ×
কাঁচা সড়ক...	... ... ×

রাস্তা ... ২৭১, ৩২২.

খাল ... ২৭.

অত্র সিটে ভুক্ত ... ১-১০৪, ২০১-২০৮, ২৭১-৩৫৮, ৩৬০-৪০৯, ৪১৮-৪৭৩, ৪৭৮-৪৮০.

NAME OF MOUZA	OLD J.L.NO	NEW J.L.NO	P.S.	DIST.
পার্ব্বতীপুর	১২	১৭		
খোজা পুর	৯	৮		
সহরা	১১	১৬		
বড় গাছা	৩০	২৫		
জুঝার পুর	২৯	২৪		
ফরিদ পুর	২৬	৩৮		
শ্রীরাম পুর	২১	৩৬		
পশ্চিম মহেশ পুর	১৩	১৮		
হাজরা পুর	১৫	১৯		
উত্তর দামোদর পুর	১৪	২০		

MADE BY THE AUTHORITY OF GOVERNMENT IN 1934-36

F.O. Bell

SETTLEMENT OFFICER AND SUPERINTENDENT OF SURVEY

ADOPTED FOR THE PURPOSE OF OPERATION UNDER CHAPTER IV OF THE B.B.S.A.& T.ACT, 1950, WITHOUT CORRECTION.

SETTLEMENT OFFICER & SUPERINTENDENT OF SURVEY.