জিলা দিনাজপুর

থানা বীরগঞ্জ

মৌজা বড়কালা (BARAKĀLĀ)

জে, এল, নং ৩৭

রে, সা, নং ৬৮

স্কেল ১৬ = ১ মাইল

১০০ কড়িতে এক জরীপ ।

৮০ জরীপে এক মাইল ।

Name of			Survey			
Kanungo	Khanapuri Amin	Bujhara Kanungo	Khanapuri		Bujharal	
			Commenced	Ended	Commenced	Ended
B. N. Banerjee	Haripada Halder	S. N. Bagchi, M.A. Syed Amin, B. N. Banerjee	21.10.35	25.10.35	20.1.36 12.1.36	14.1.36

সাঙ্কেতিক

দালান ... ...

ত্রিসীমানার পিলার ... ... △

অন্যান্য পিলার ... ... □

লোহার পিলার 1

ট্রাভার্স ষ্টেসন ... ... ○

জি, টি, ষ্টেসন ... ... △

বেঞ্চমার্ক ... ...

পাকা ইন্দারা ... ...

নল কূপ ... ...

পান বরজ ... ...

দাগ নং

পাকা সড়ক ... ... ×

কাঁচা সড়ক ১২,

রাস্তা ... ১৯, ৯৪, ২৭০,

খাল ২৭২,

অত্র সিটে ভুক্ত ... ১–১৬৬, ১৬৮–২০২, ২০৬–২৪৬,

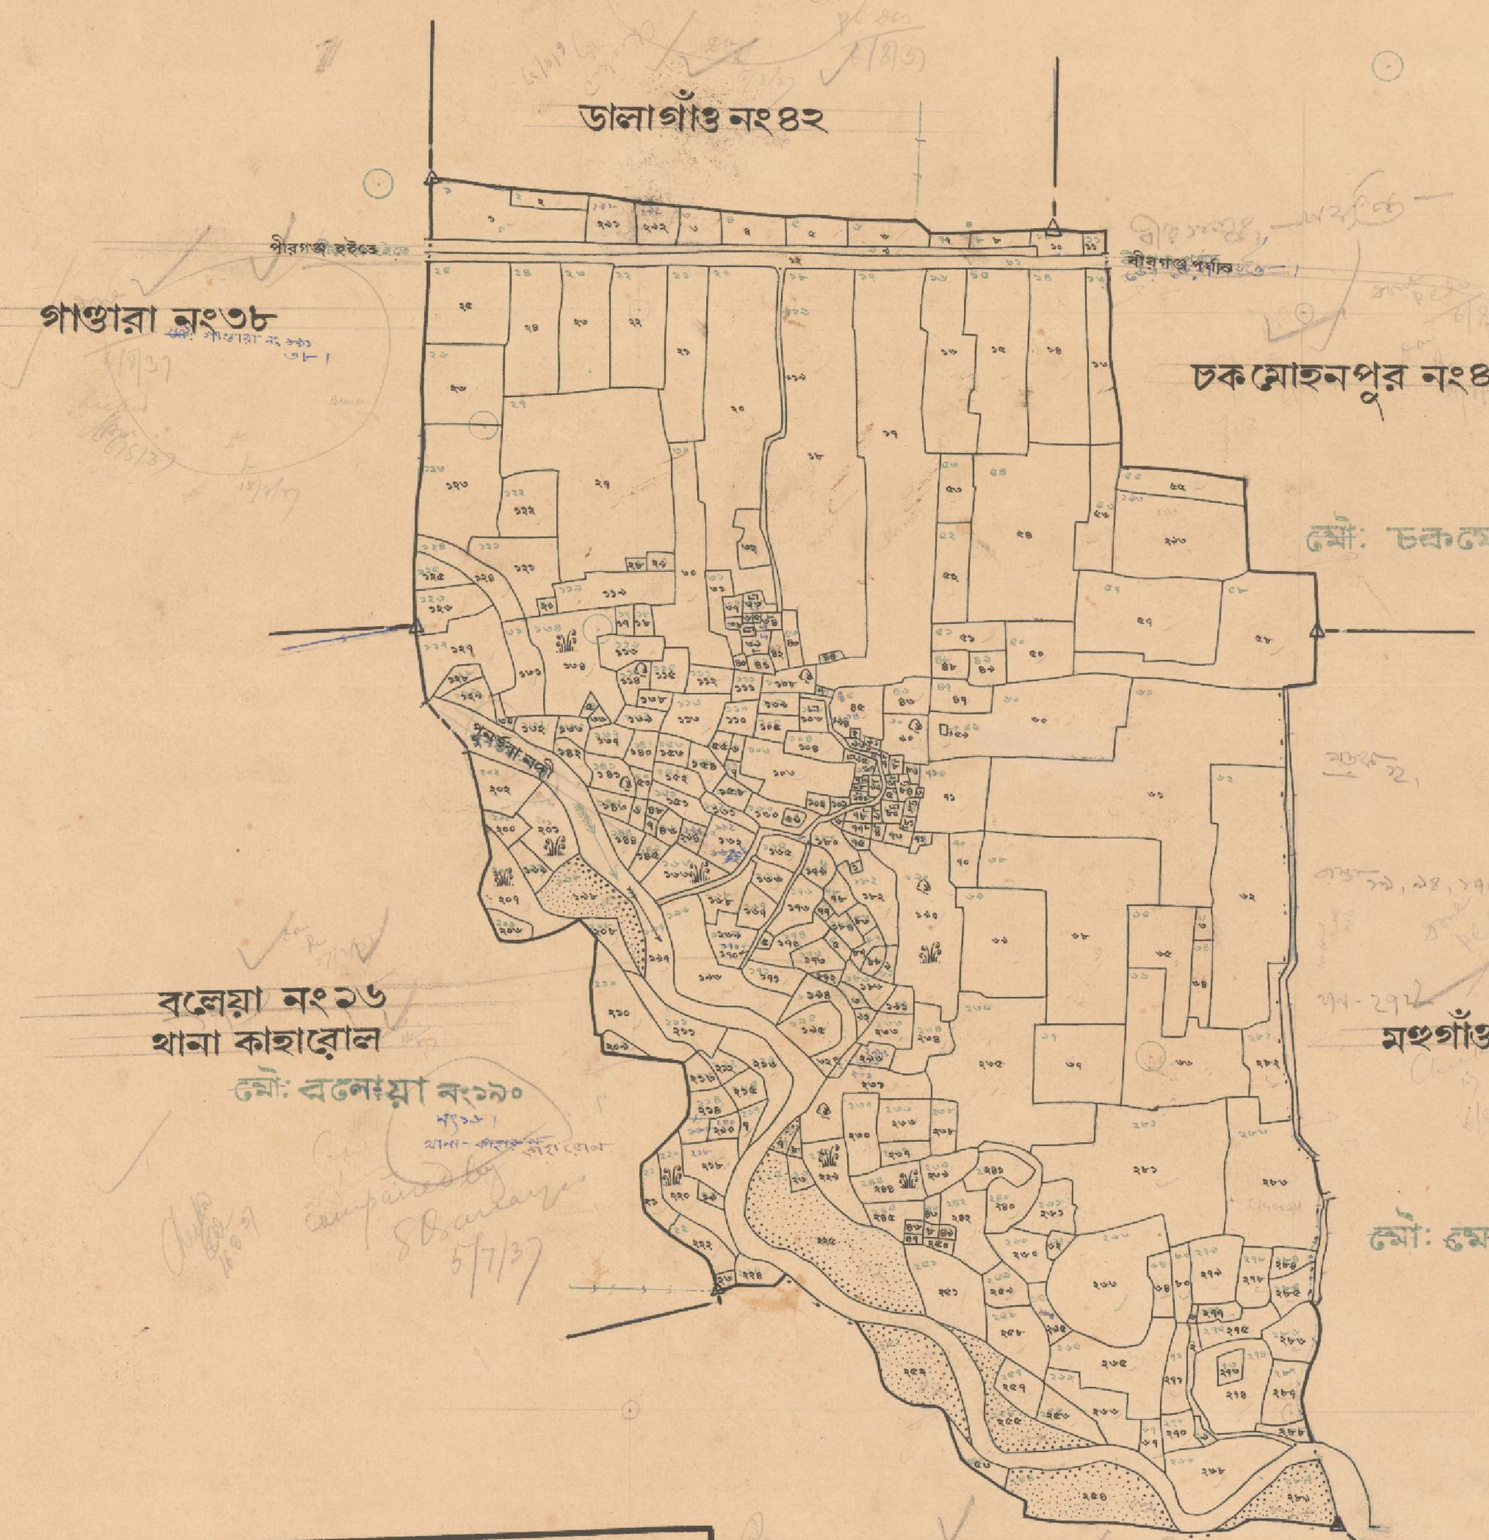

MADE BY THE AUTHORITY OF GOVERNMENT IN 1935-37

F. O. Bell

SETTLEMENT OFFICER AND SUPERINTENDENT OF SURVEY

Photo No	Plots No
100-18	1-112, 290-293
02 145-2	113-281, 294-295
144-2	282-289

ADOPTED FOR THE PURPOSE OF OPERATION UNDER CHAPTER IV OF THE E.B.S.A.& T.ACT, 1950, WITHOUT CORRECTION.

SETTLEMENT OFFICER & SUPERINTENDENT OF SURVEY.