H-53

জিলা দিনাজপুর

থানা নবাবগঞ্জ

মৌজা আন্দলগ্রাম (ANDALGRAM) সিট নং১

জে, এল, নং ১৩৮ রে, সা, নং ৪৪২৯, ৪৫৩০

রে, সা, নং ৪৪২৯, ৪৫৩০

স্কেল ১৬" = ১ মাইল

১০০ কড়িতে এক জরীপ ;
৮০ জরীপে এক মাইল ;

0 1 2 3 4 5 ... 30 জরীপ

জিলা দিনাজপুর
সার্কেল
স্কেল ১৬" = ১ মাইল

Name of				Survey		Khanapuri		Bujharat	
Kanungo	Kistiwar Amin	Khanapuri Amin	Bujharat	Commenced	Ended	Commenced	Ended	Commenced	Ended
M.N. S	Rofiq	Rofiq	M.N.S	17-1-35	5-2-35	17-1-35	5-2-35	11.6.35	18.6.35

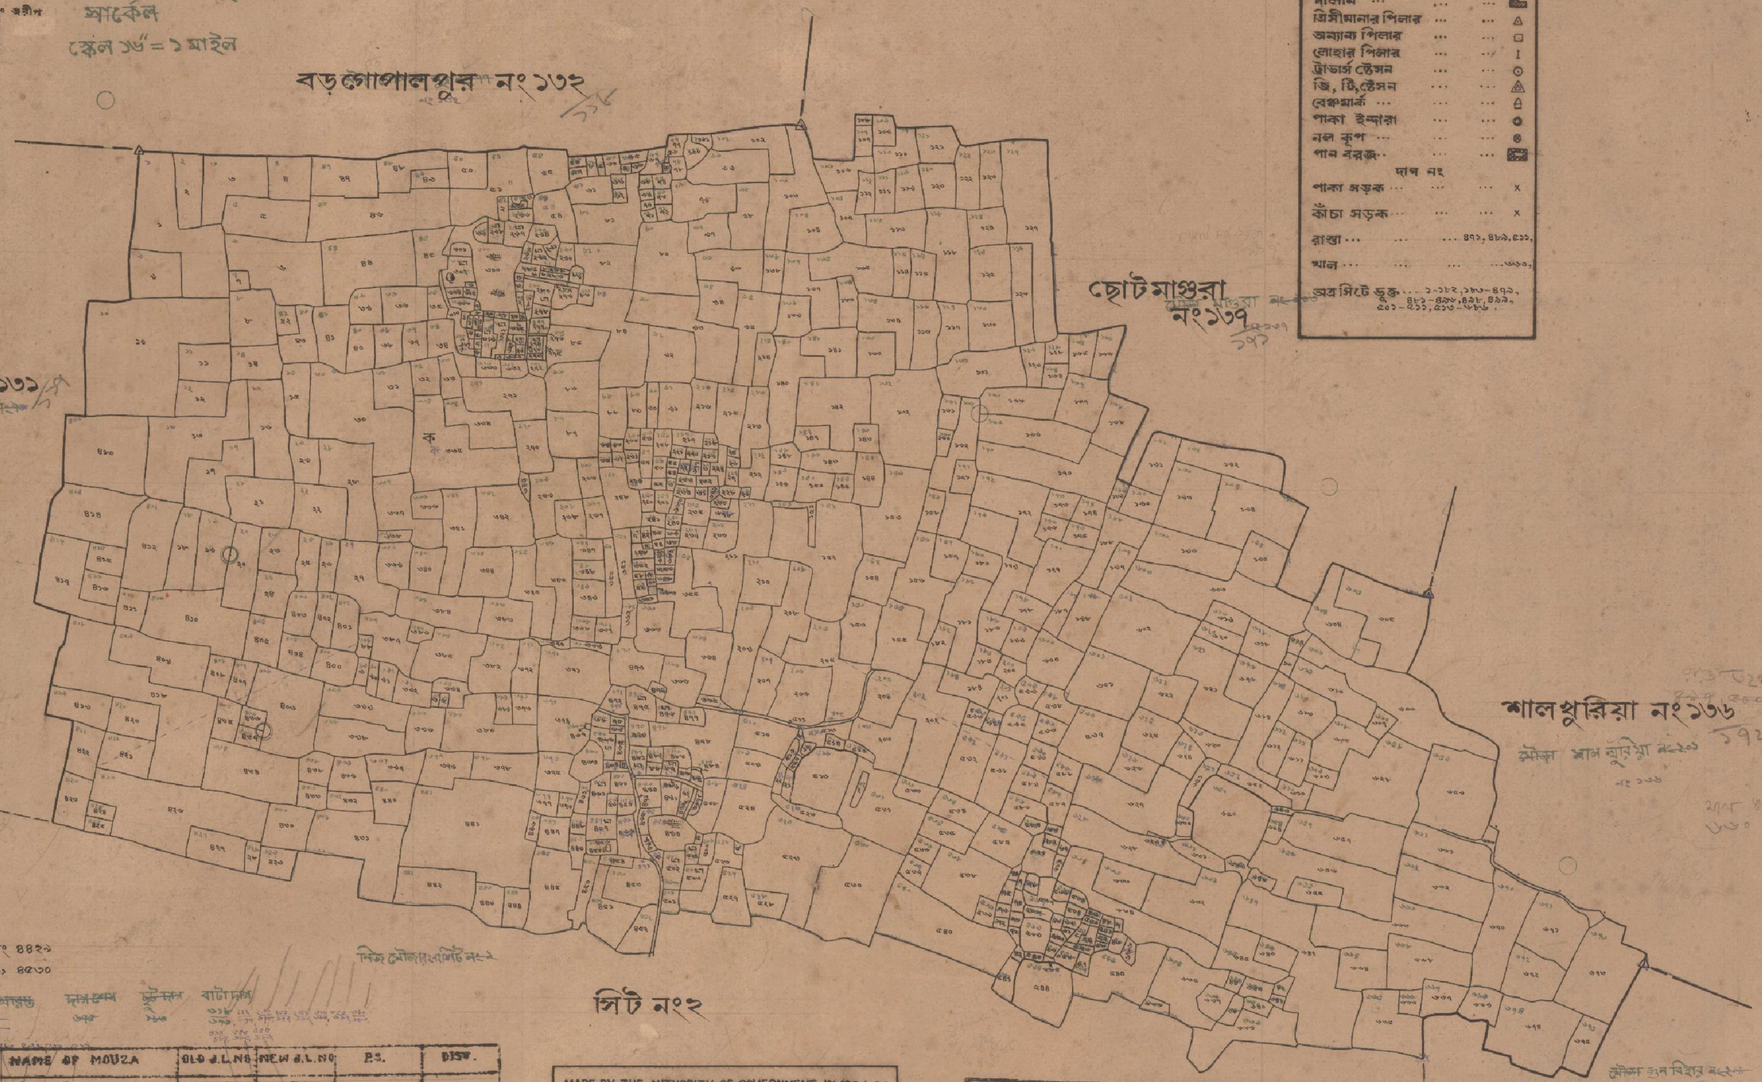

সাঙ্কেতিক

দালান	
ত্রিসীমানার পিলার	△
অন্যান্য পিলার	□
লোহার পিলার	I
ট্রাভার্স ষ্টেসন	⊙
জি, টি, ষ্টেসন	△
বেঞ্চমার্ক	
পাকা ইন্দারা	●
নল কূপ	⊗
পান বরজ	
দাগ নং	
পাকা সড়ক	X
কাঁচা সড়ক	X
রাস্তা	৪৭১, ৪৮৯, ৫১১,
খাল	৬৬১০,
এই সিটে ভুক্ত ...	১-১৮২, ১৯৬-৪৭১, ৪৭১-৪৮৮, ৪৮৯-৪৯৭, ৪৯৯-৫১১, ৫১৩-৬৬১।

ক- আন্দলগ্রাম রে, সা, নং ৪৪২৯
খ- চণ্ডিপুর " " " ৪৫৩০

সিট নং২

	NAME OF MOUZA	OLD J.L.NO	NEW J.L.NO	P.S.	DIST.
	আন্দলগ্রাম	১৩৮	১৭৩		
	বড়গোপালপুর	১৩৯	১৭৮		
	ছোটমাঞ্জরা	১৩৭	১৭২		
	শালখুরিয়া	১৩৬	১৭২		
	গুণবিহার	১৪১	১৭৬		
	দিওর	১৩১	১১৭		

MADE BY THE AUTHORITY OF GOVERNMENT IN 1934-36

F.O. Bell

SETTLEMENT OFFICER AND SUPERINTENDENT OF SURVEY

ADOPTED FOR THE PURPOSES OF OPERATION UNDER CHAPTER IV OF THE B.T.S.A.& T. ACT, 1950, WITHOUT CORRECTION.

SETTLEMENT OFFICER & SUPERINTENDENT OF SURVEY.

Photo No
170-5
170-6
171-5

Plots
1- 404, 441-526
527- 676
405- 440