জিলা দিনাজপুর

থানা বীরগঞ্জ

মৌজা জগদল সিট নং ২ (JAGDAL)

জে, এল, নং ১৬৩

রে, সা, নং ৯২

স্কেল ১৬" = ১ মাইল

১০০ কড়িতে এক জরীপ।

৮০ জরীপে এক মাইল।

Kanungo	Kistwar Amin	Khanpuri Amin	Sujhoraf Amin	Bujharat Amin	Survey Commenced	Survey Ended	Khanapuri Commenced	Khanapuri Ended	Bujharat Commenced	Bujharat Ended
Nr. Banerjee		Jalaluddin Zaka		B.K. Pandit + Jnan B. Chaudhury			15/10/35	5/12/35	20/1/36	29/1/36

সাঙ্কেতিক

দালান ... ...

ত্রিসীমানার পিলার ... ...

অন্যান্য পিলার ... ...

লোহার পিলার ... ...

ট্রাভার্স ষ্টেসন ... ...

জি, টি, ষ্টেসন ... ...

বেঞ্চমার্ক ... ...

পাকা ইন্দারা ... ...

নল কূপ ... ...

পান বরজ ... ...

দাগ নং

পাকা সড়ক ... ... ×

কাঁচা সড়ক ... ... ×

রাস্তা ... ১১০৪, ১১৬৬, ১২৪২, ১২৬৫, ১৪২২, ১৪২৫, ১৪৪৭,

খাল ... ... ×

অত্রসিটে ভুক্ত ... ১০০৪, ১০১৮ – ১১৮১, ১১৮৭ – ১২১০, ১২১৩ – ১২১৯, ১২৯৪ – ১৩৪০, ১৩৪৭, ১৩৪৯ – ১৪৫২,

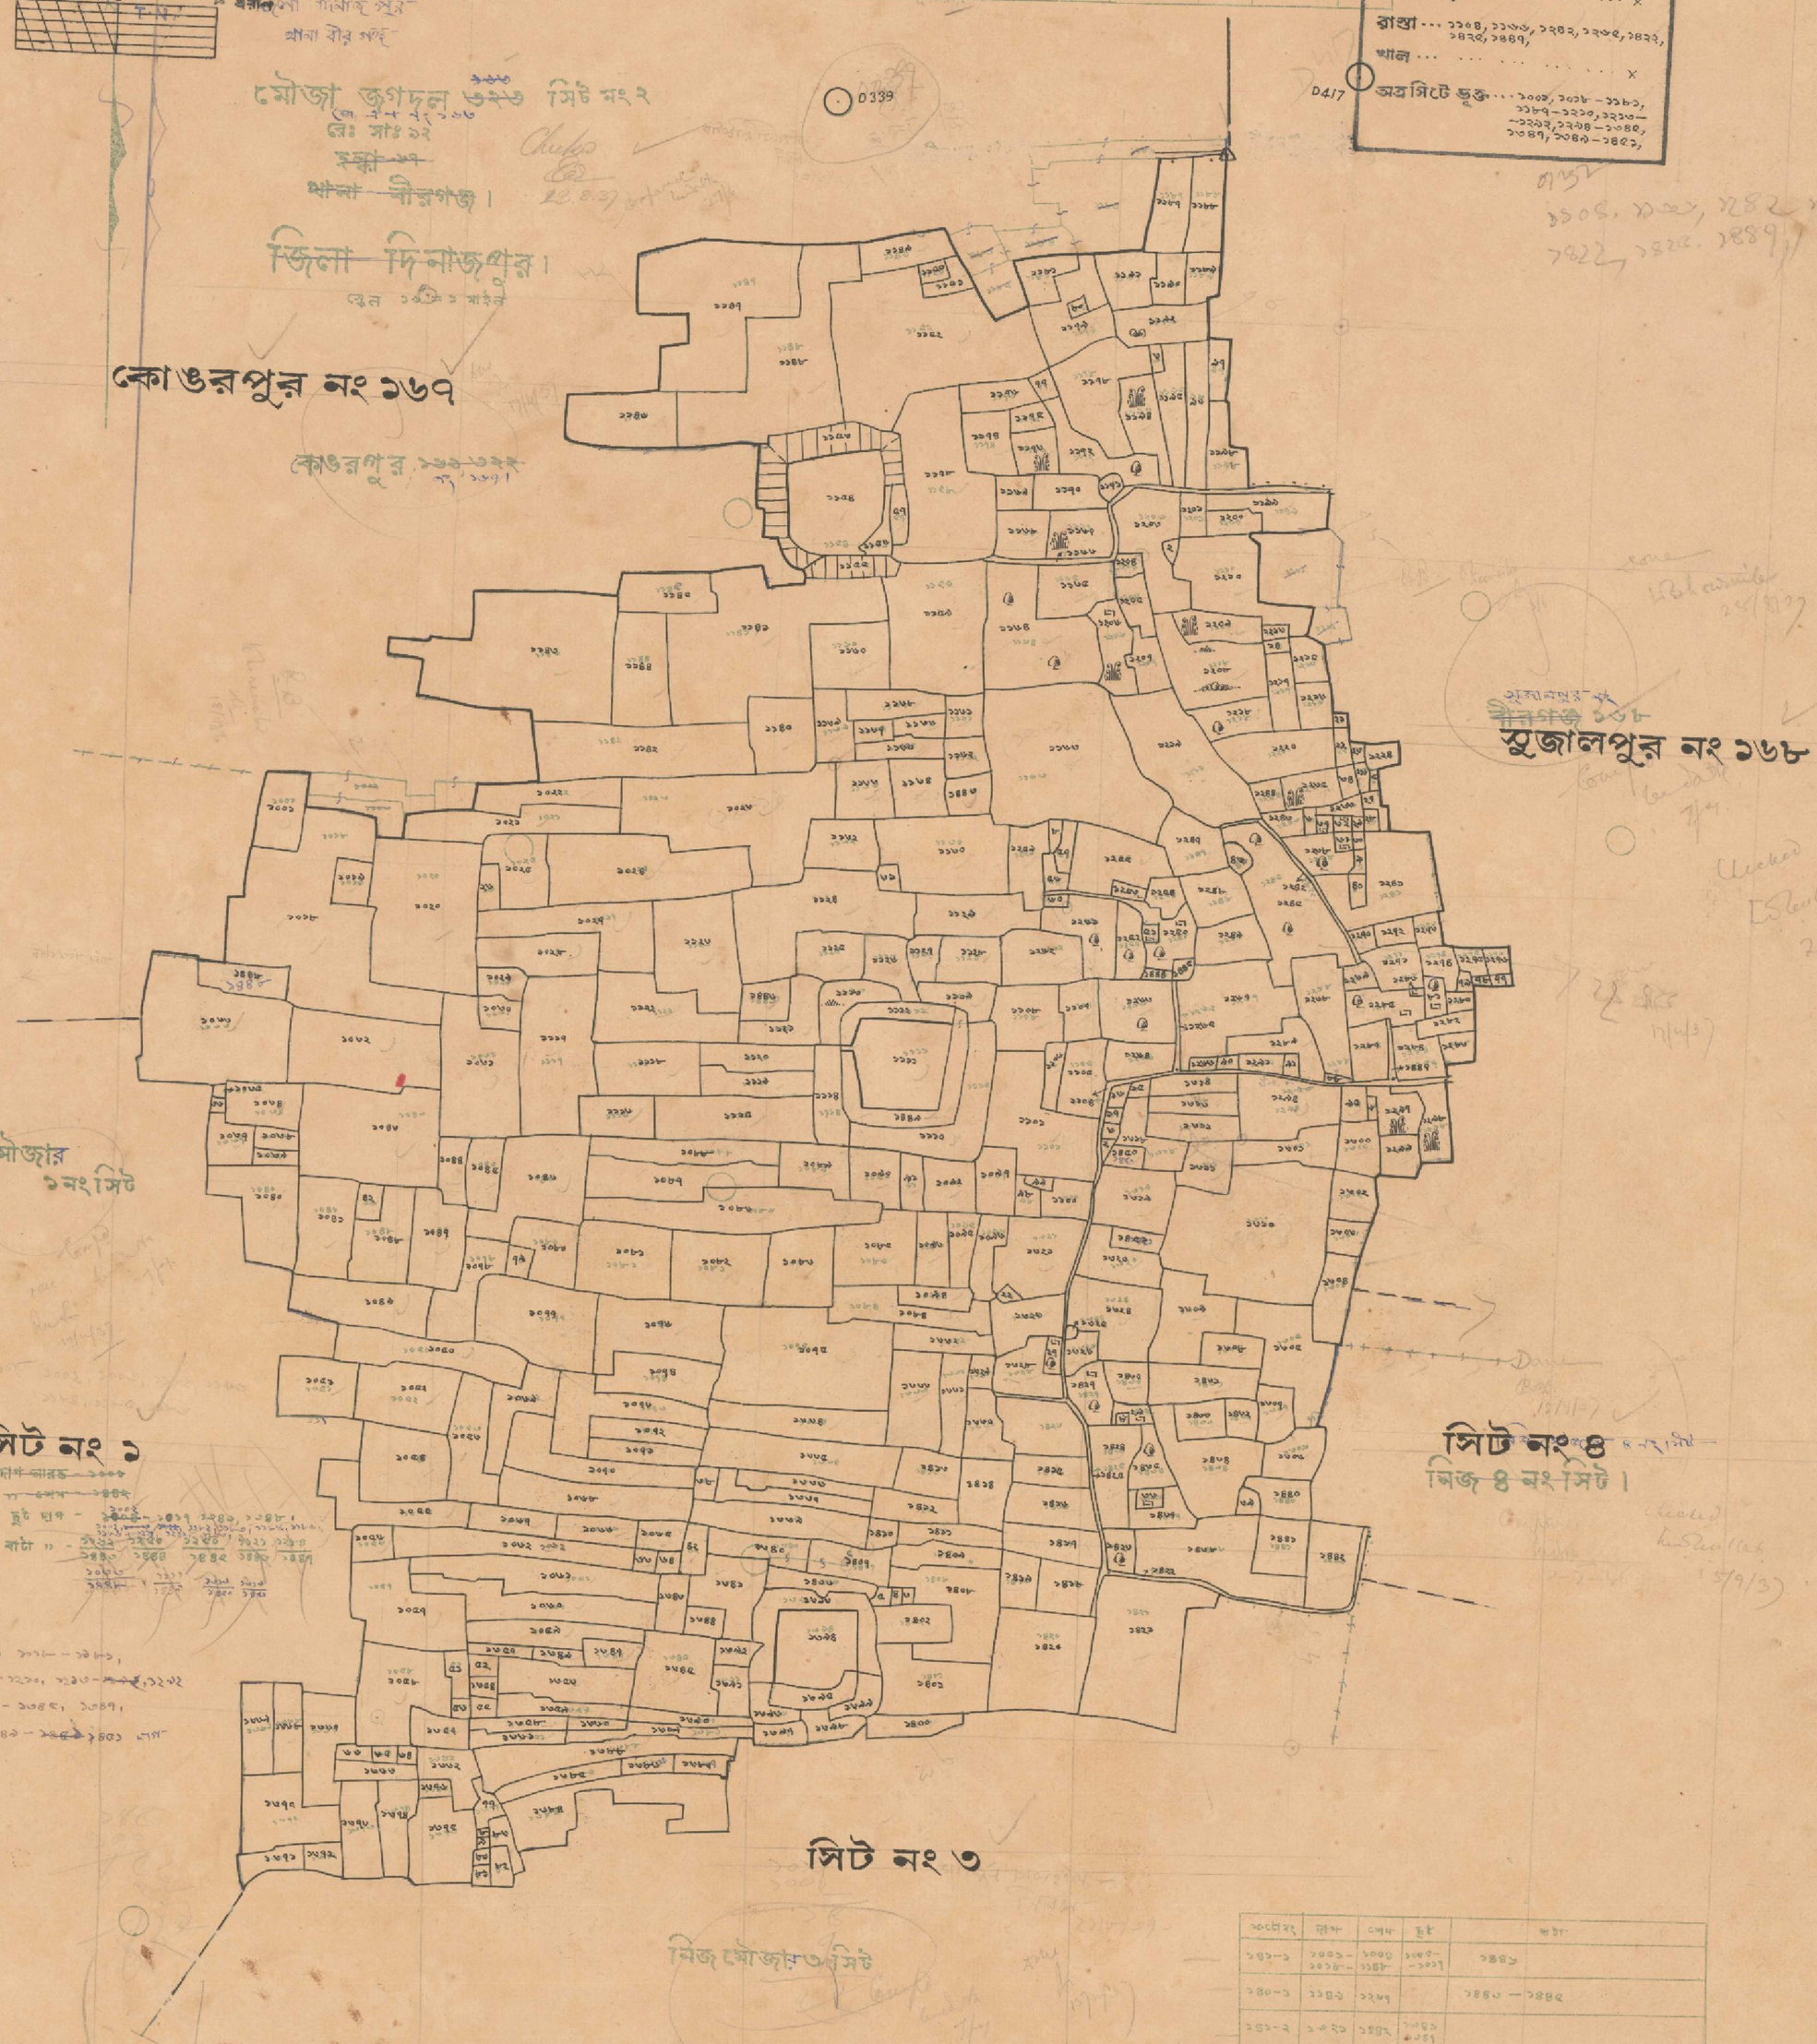

[illegible]	দাগ	খেমা	ইঞ্চি		মন্তব্য
[illegible]	[illegible]	[illegible]	[illegible]	[illegible]	
[illegible]	[illegible]	[illegible]		[illegible]	[illegible]
[illegible]	[illegible]	[illegible]	[illegible]		
[illegible]	[illegible]	[illegible]			

MADE BY THE AUTHORITY OF GOVERNMENT IN 1935-37

F O Bell

SETTLEMENT OFFICER AND SUPERINTENDENT OF SURVEY

ADOPTED FOR THE PURPOSE OF OPERATION UNDER CHAPTER IV OF THE E.B.B.A.& T.ACT, 1950, WITHOUT CORRECTION.

SETTLEMENT OFFICER & SUPERINTENDENT OF SURVEY.