জিলা দিনাজপুর

থানা ফুলবাড়ী
মৌজা ভাটপাইল (BHAT PAIL)
জে.এল.নং ১৮০
রে.সা.নং ৪৭৯৫
স্কেল ১৬" = ১ মাইল

১০০ কড়িতে এক জরীপ।
৮০ জরীপে এক মাইল।

Kanungo	Inspector	Amin	Khanapur amin	Sighurat kanungo	Survey Commenced	Survey Ended	Khanapur Commenced	Khanapur Ended	Bighurat Commenced	Bighurat Ended
Mallik	Abdul Latif Mech		Abdul Latif Mech	Abdul Gani					20.5.36	25.5.36

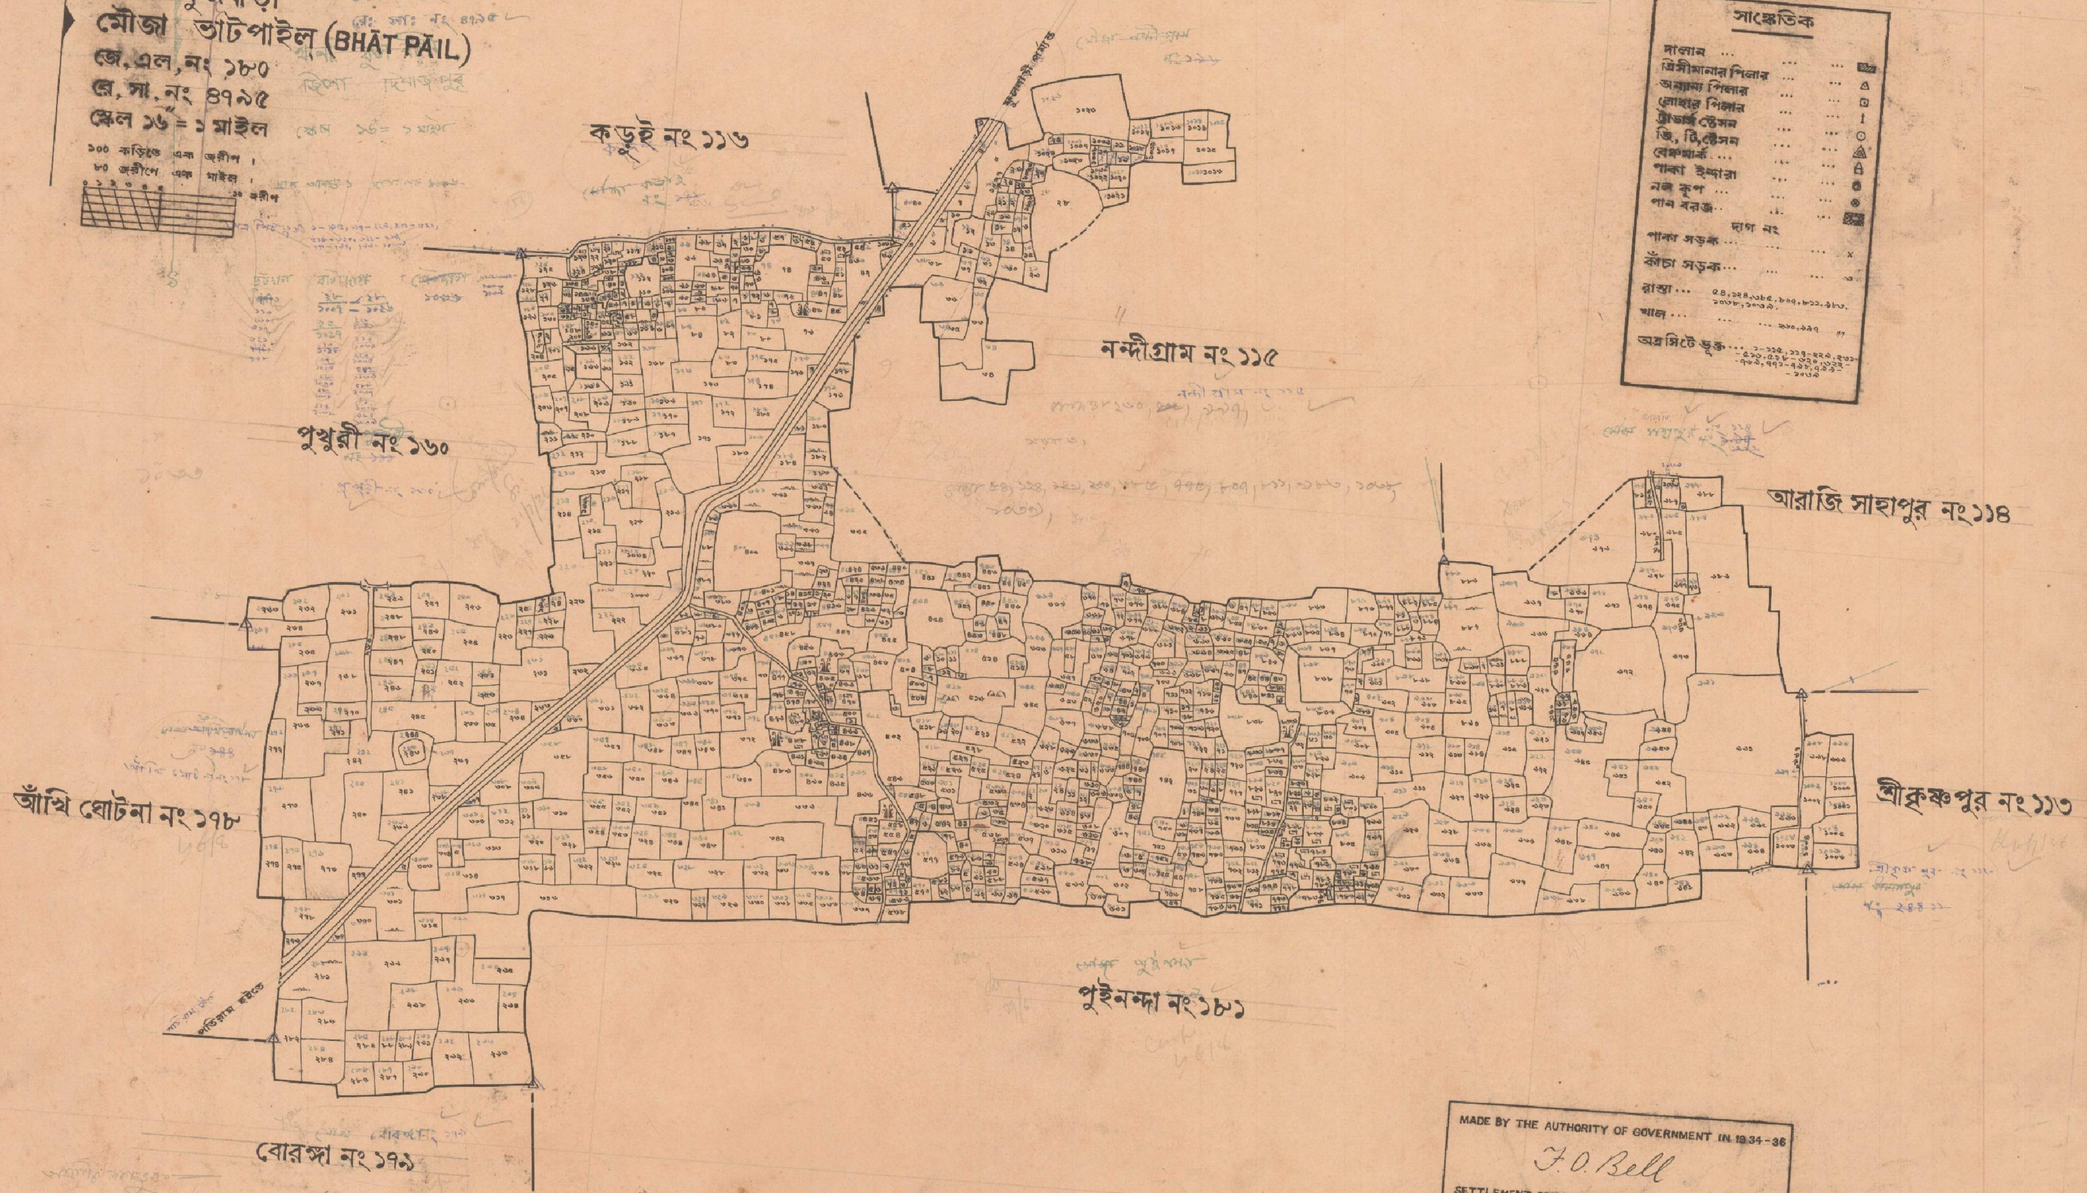

সাঙ্কেতিক

দালান ...
ত্রিসীমানার পিলার ...
অন্যান্য পিলার ...
লোহার পিলার ...
ট্রাভার্স ষ্টেসন ...
জি. টি. ষ্টেসন ...
বেঞ্চমার্ক ...
পাকা ইমারত ...
নল কূপ ...
পান বরজ ...

দাগ নং

পাকা সড়ক ...
কাঁচা সড়ক ...
রাস্তা ... ৫৪, ২২৪, ৩১৮৫, ৮৩৭, ৮৩১, ৫১৮, ১০১৮, ১৩০৩.
খাল ... ২৯০, ৩১৭
অত্র সিটে ভুক্ত ...

MADE BY THE AUTHORITY OF GOVERNMENT IN 1934-36
F. O. Bell
SETTLEMENT OFFICER AND SUPERINTENDENT OF SURVEY

NAME OF MOUZA	OLD J.L.NO	NEW J.L.NO	R.S.	DIST.
ভাটপাইল	১৮০	১৬২		
কড়ুই	১১৬	১০২		
নন্দীগ্রাম	১১৫	১৬০		
আরজী সাহাপুর	১১৪	১৬১		
শ্রীকৃষ্ণপুর	১১৩	১৫৯		
পুইনন্দা	১৮১	১৬৩		
বোরঙ্গা	১৭৯	১৬৪		
আঁখিঘোটনা	১৭৮	১৬৫		
পুখরী	১৬০	১০১		

ADOPTED FOR THE PURPOSE OF OPERATION UNDER CHAPTER IV OF THE B.B.S.A.& T.ACT, 1950, WITHOUT CORRECTION.

SETTLEMENT OFFICER & SUPERINTENDENT OF SURVEY.