জিলা দিনাজপুর

থানা বোচাগঞ্জ
মৌজা সাহসপুর (SAHASPUR)
জে, এল, নং ৩৭
রে, সা, নং ৩১৫
স্কেল ১৬" = ১ মাইল

১০০ গজে এক ইঞ্চি
৮০ জরীপে এক মাইল
০ ১ ২ ৩ ৪ ৫ ১০ জরীপ

Name of				Survey			
				Kistwar		Khanapuri	
Kanoon go.	Kistwar Amin	Khanapuri Amin	Bugharat kgo.	Commenced	Ended	Commenced	Ended
D. C. Sen.	Md. Hanif	Md. Hanif	Nur Chowdhury	11-12-35	19-12-35	20-12-35	

সাঙ্কেতিক

দালান	Bugharat	
ত্রিসীমানার পিলার		
ক্রমানা পিলার	Commenced	Ended
লোহার পিলার		
ট্রাভার্স ষ্টেসন		
জি, টি, ষ্টেসন		
বেঞ্চমার্ক		
পাকা ইন্দারা		
নল কূপ		
পান বরজ		

দাগ নং
পাকা সড়ক
কাঁচা সড়ক
রাস্তা
খাল
অত্রসিটে ভূক্ত

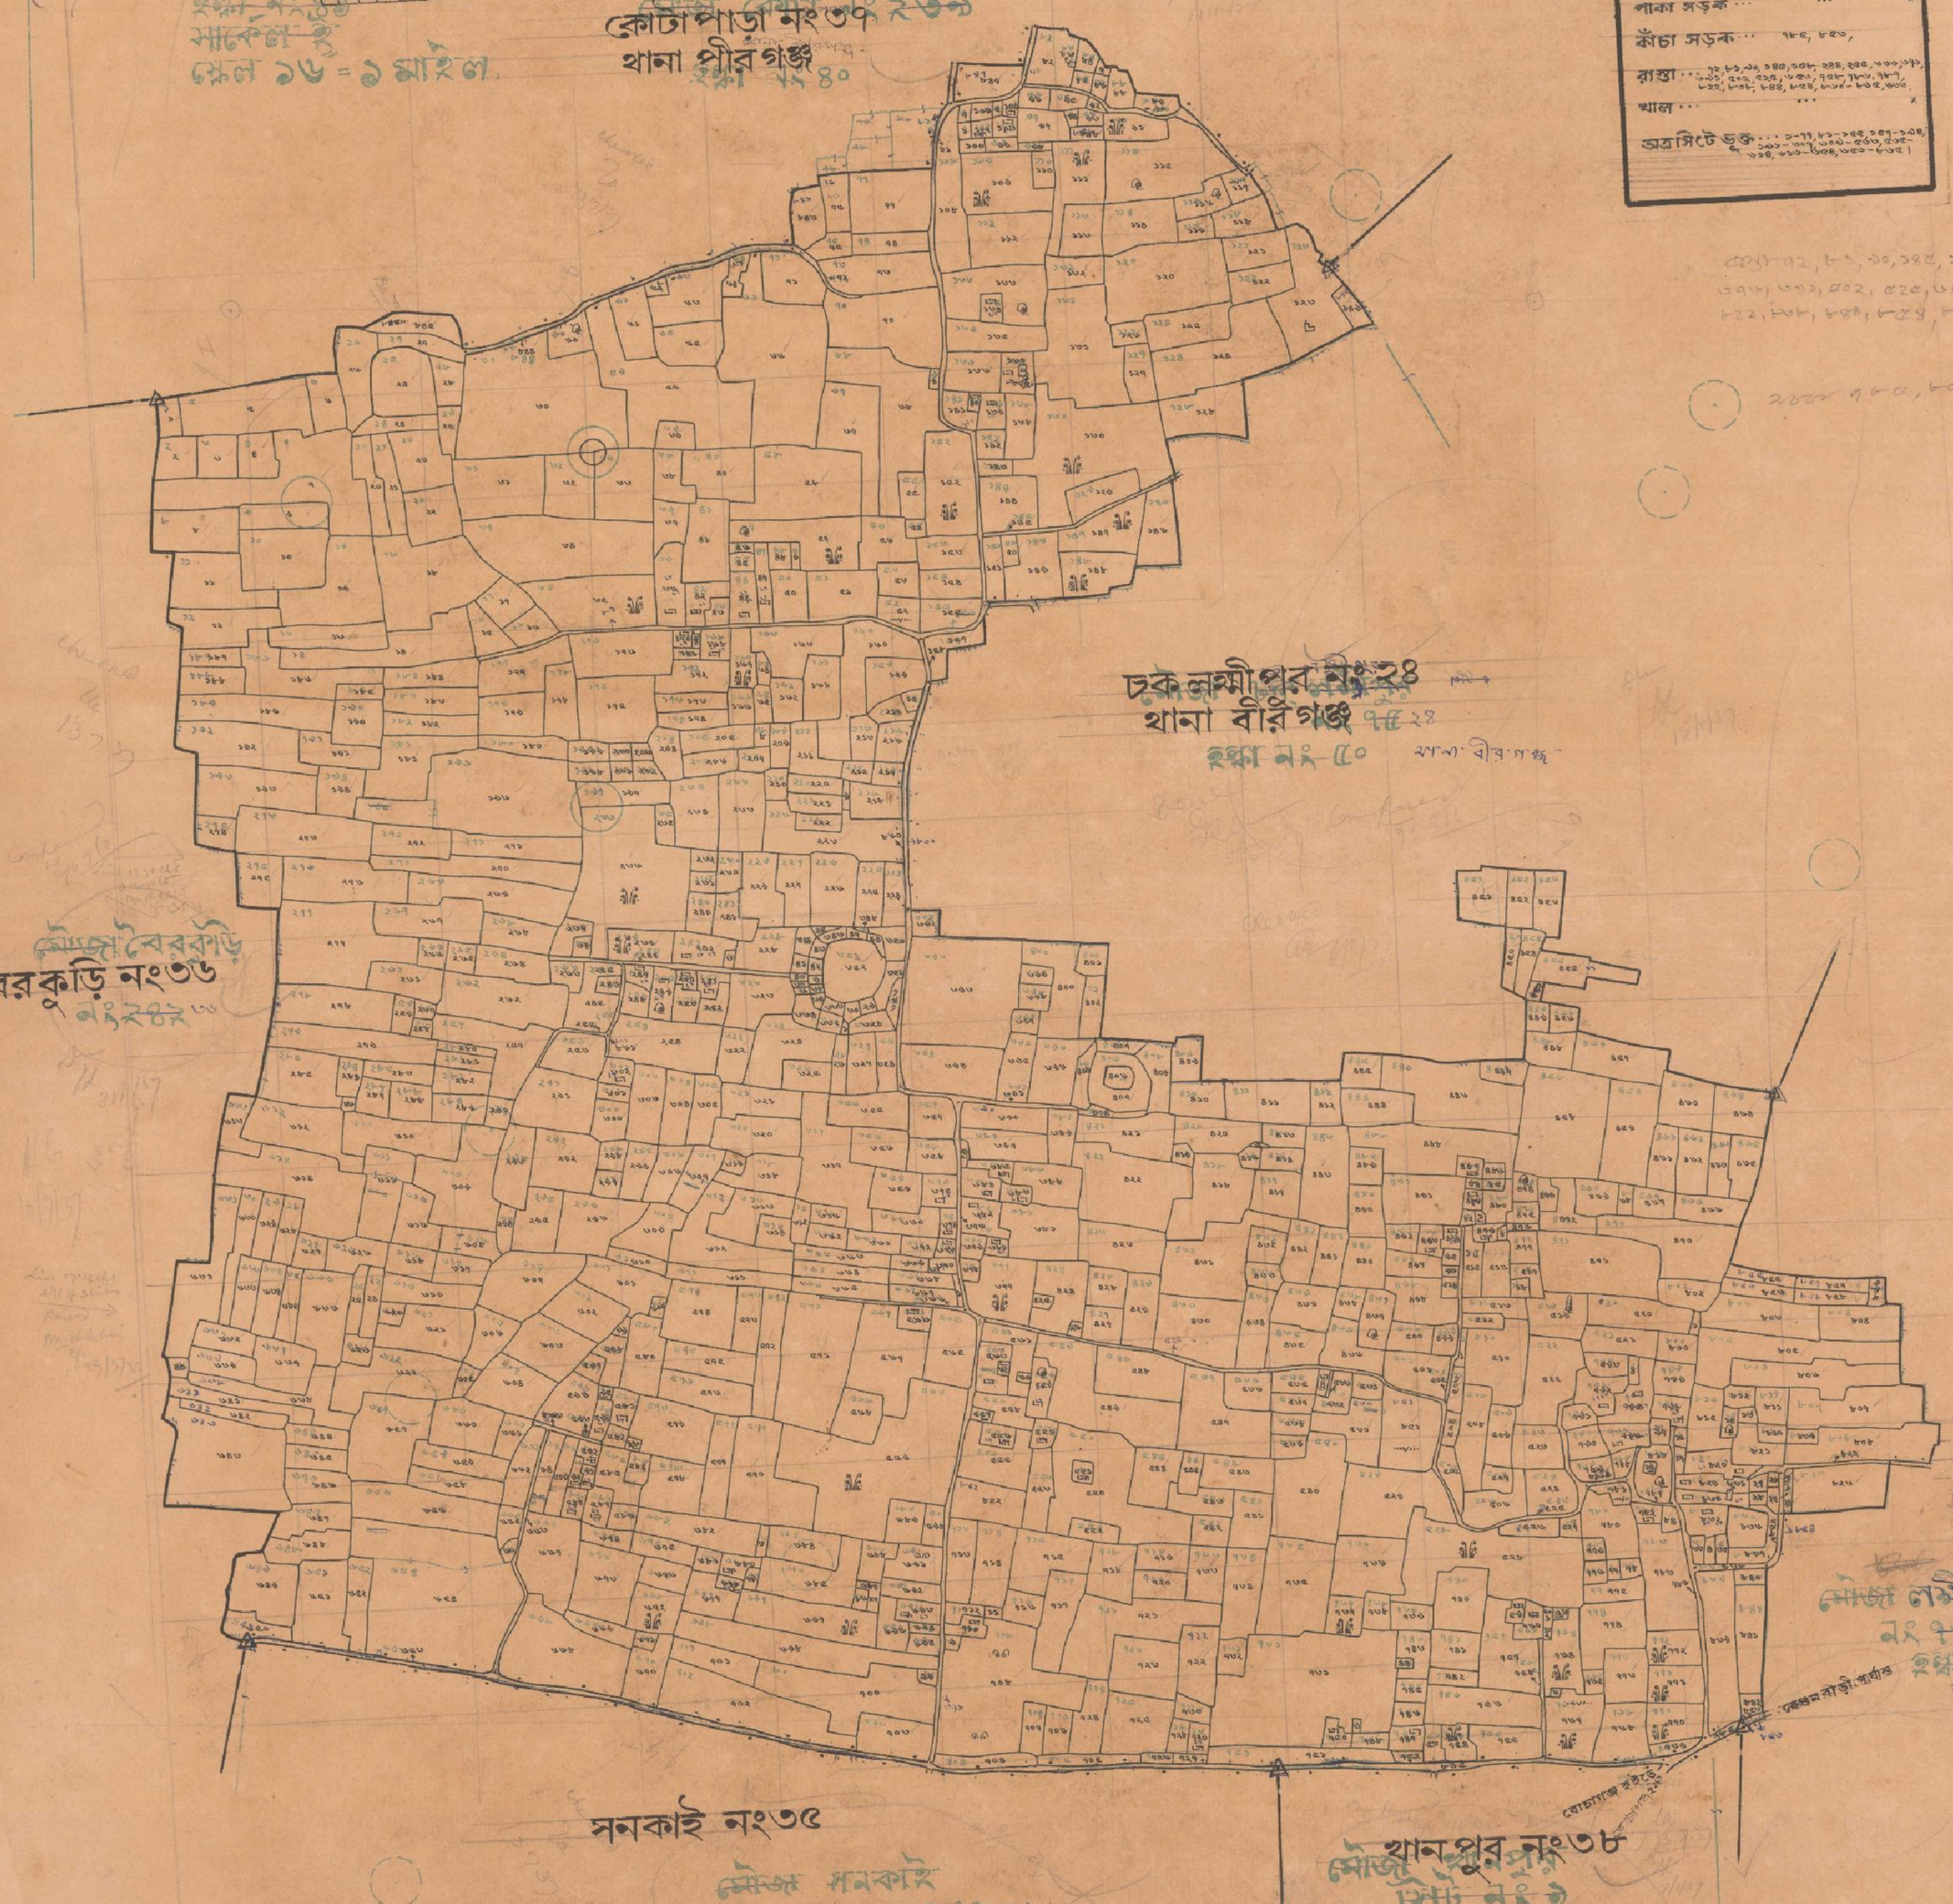

MADE BY THE AUTHORITY OF GOVERNMENT IN 1935-37
For Bell
SETTLEMENT OFFICER AND SUPERINTENDENT OF SURVEY

ADOPTED FOR THE PURPOSE OF OPERATION UNDER CHAPTER IV OF THE E.B.S.A.& T.ACT, 1950, WITHOUT CORRECTION.
SETTLEMENT OFFICER & SUPERINTENDENT OF SURVEY.