জিলা দিনাজপুর

থানা বীরগঞ্জ

মৌজা নিজপাড়া সিট নং ২ (NIJPĀRĀ)

জে, এল, নং ১৪৬

রে, সা, নং ৩৮

স্কেল ১৬" = ১ মাইল

১০০ কড়িতে এক জরীপ।
৮০ জরীপে এক মাইল।

Kanungo	Kistwar Amin	Khanapuri Amin	Bujharat Kanungo	Survey Commenced	Survey Ended	Khanapuri Commenced	Khanapuri Ended
P.N. Adhikari		Madhab Ch. Biswas	P.N. Adhikari			25.10.3[illegible]	[illegible]

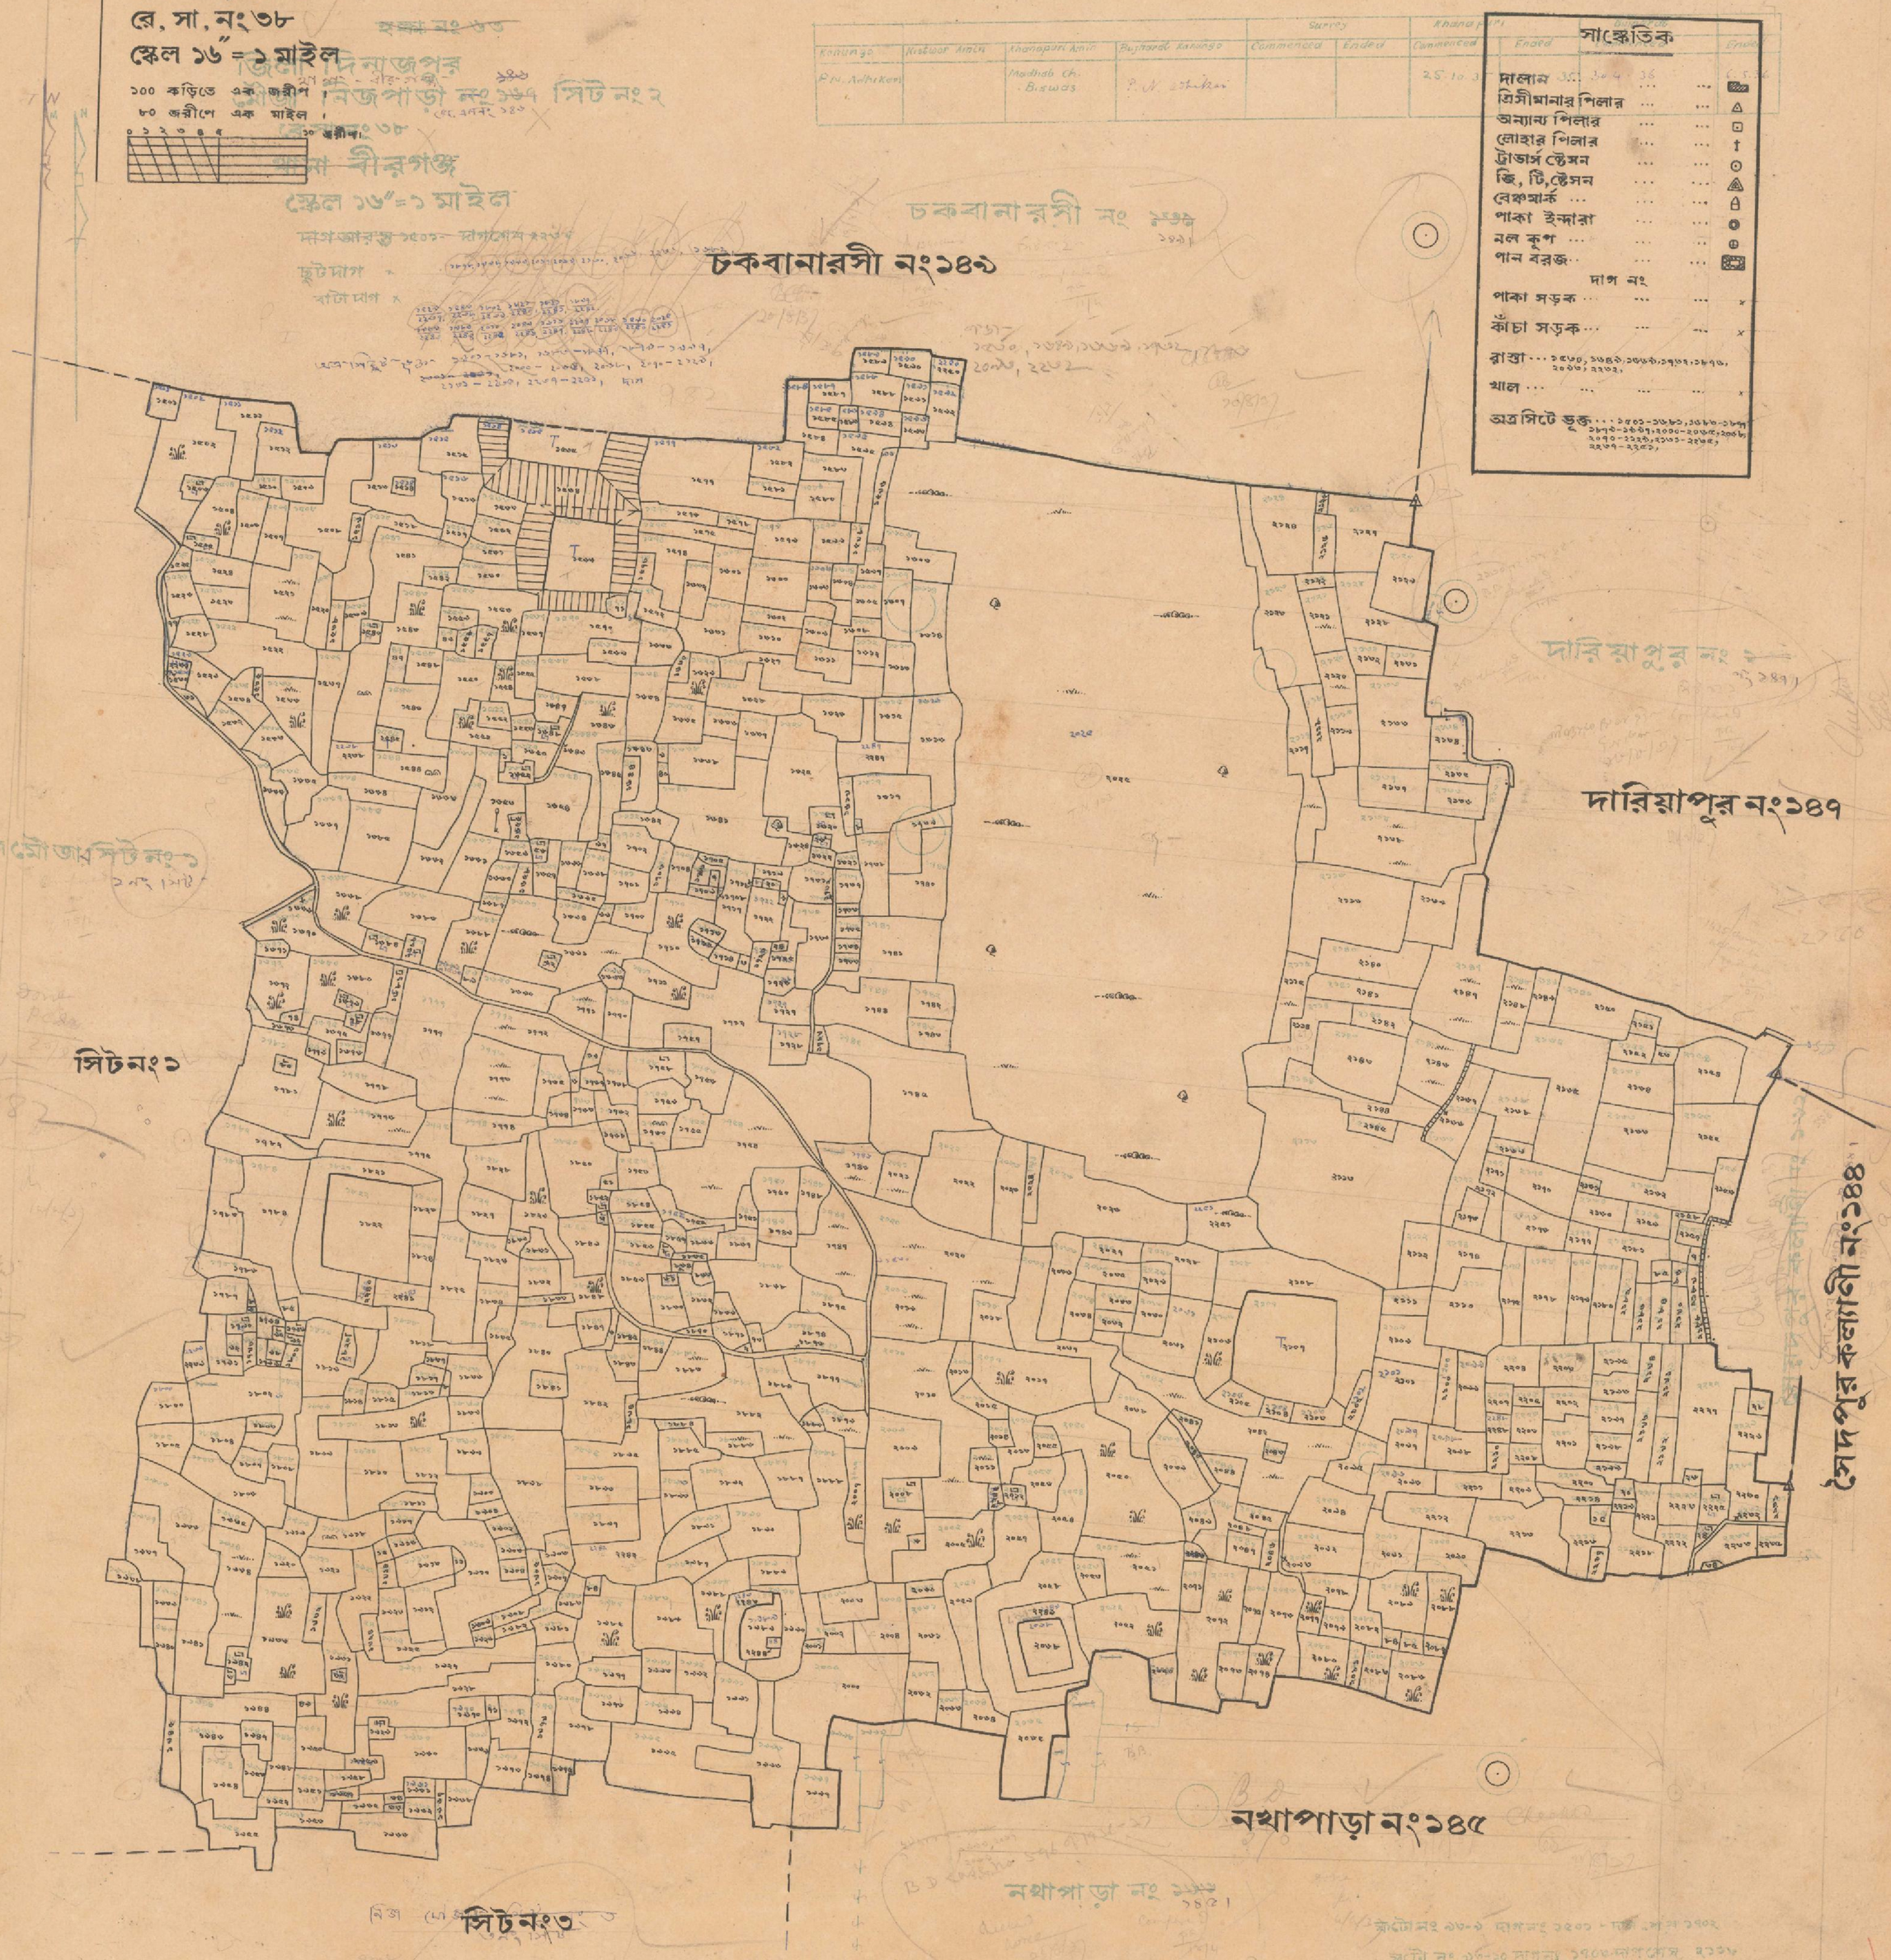

সাঙ্কেতিক

দালান	
ত্রিসীমানার পিলার	
অন্যান্য পিলার	
লোহার পিলার	
ট্রাভার্স ষ্টেসন	
জি, টি, ষ্টেসন	
বেঞ্চমার্ক	
পাকা ইন্দারা	
নল কূপ	
পান বরজ	
দাগ নং	
পাকা সড়ক	
কাঁচা সড়ক	
রাস্তা	২৫৬৩, ২৬৪৯, ২৬৬৯, ২৭৬৭, ২৮৭৬, ২০৬৩, ২২৬২,
খাল	
অত্রসিটে ভুক্ত	২৫০১-২৬৮১, ২৬৮৩-২৮৭৭, ২৮৭৯-২৮৯৭, ২০০৮-২০৬৫, ২০৬৮, ২০৭০-২২২৯, ২২৬১-২৫৬৫, ২২৬৭-২২৮১,

MADE BY THE AUTHORITY OF GOVERNMENT IN 1935-37

For Bell

SETTLEMENT OFFICER AND SUPERINTENDENT OF SURVEY

ADOPTED FOR THE PURPOSE OF OPERATION UNDER CHAPTER IV OF THE B.B.S.A.& T.ACT, 1950, WITHOUT CORRECTION.

SETTLEMENT OFFICER & SUPERINTENDENT OF SURVEY.