জিলা দিনাজপুর

থানা নবাবগঞ্জ

মৌজা হাতভাঙ্গি (HĀTBHANGI)

জে, এল, নং ১৯৫

রে, সা. নং ৫৩৬০, ৫৩৬৩

স্কেল ১৬" = ১ মাইল

১০০ কড়িতে এক জরীপ

৮০ জরীপে এক মাইল

Name of			Survey			Khanapuri		Report	
Zamindar	Raiyat	Raiyat	Commenced	Ended	Commenced	Ended	Commenced	Ended
Z. Islam	A. Razzak H. Rasul	A. Razzak H. Rasul	Z. Islam	21.2.35	2.3.35	21.2.35	2.3.35	16.5.35	21.5.35

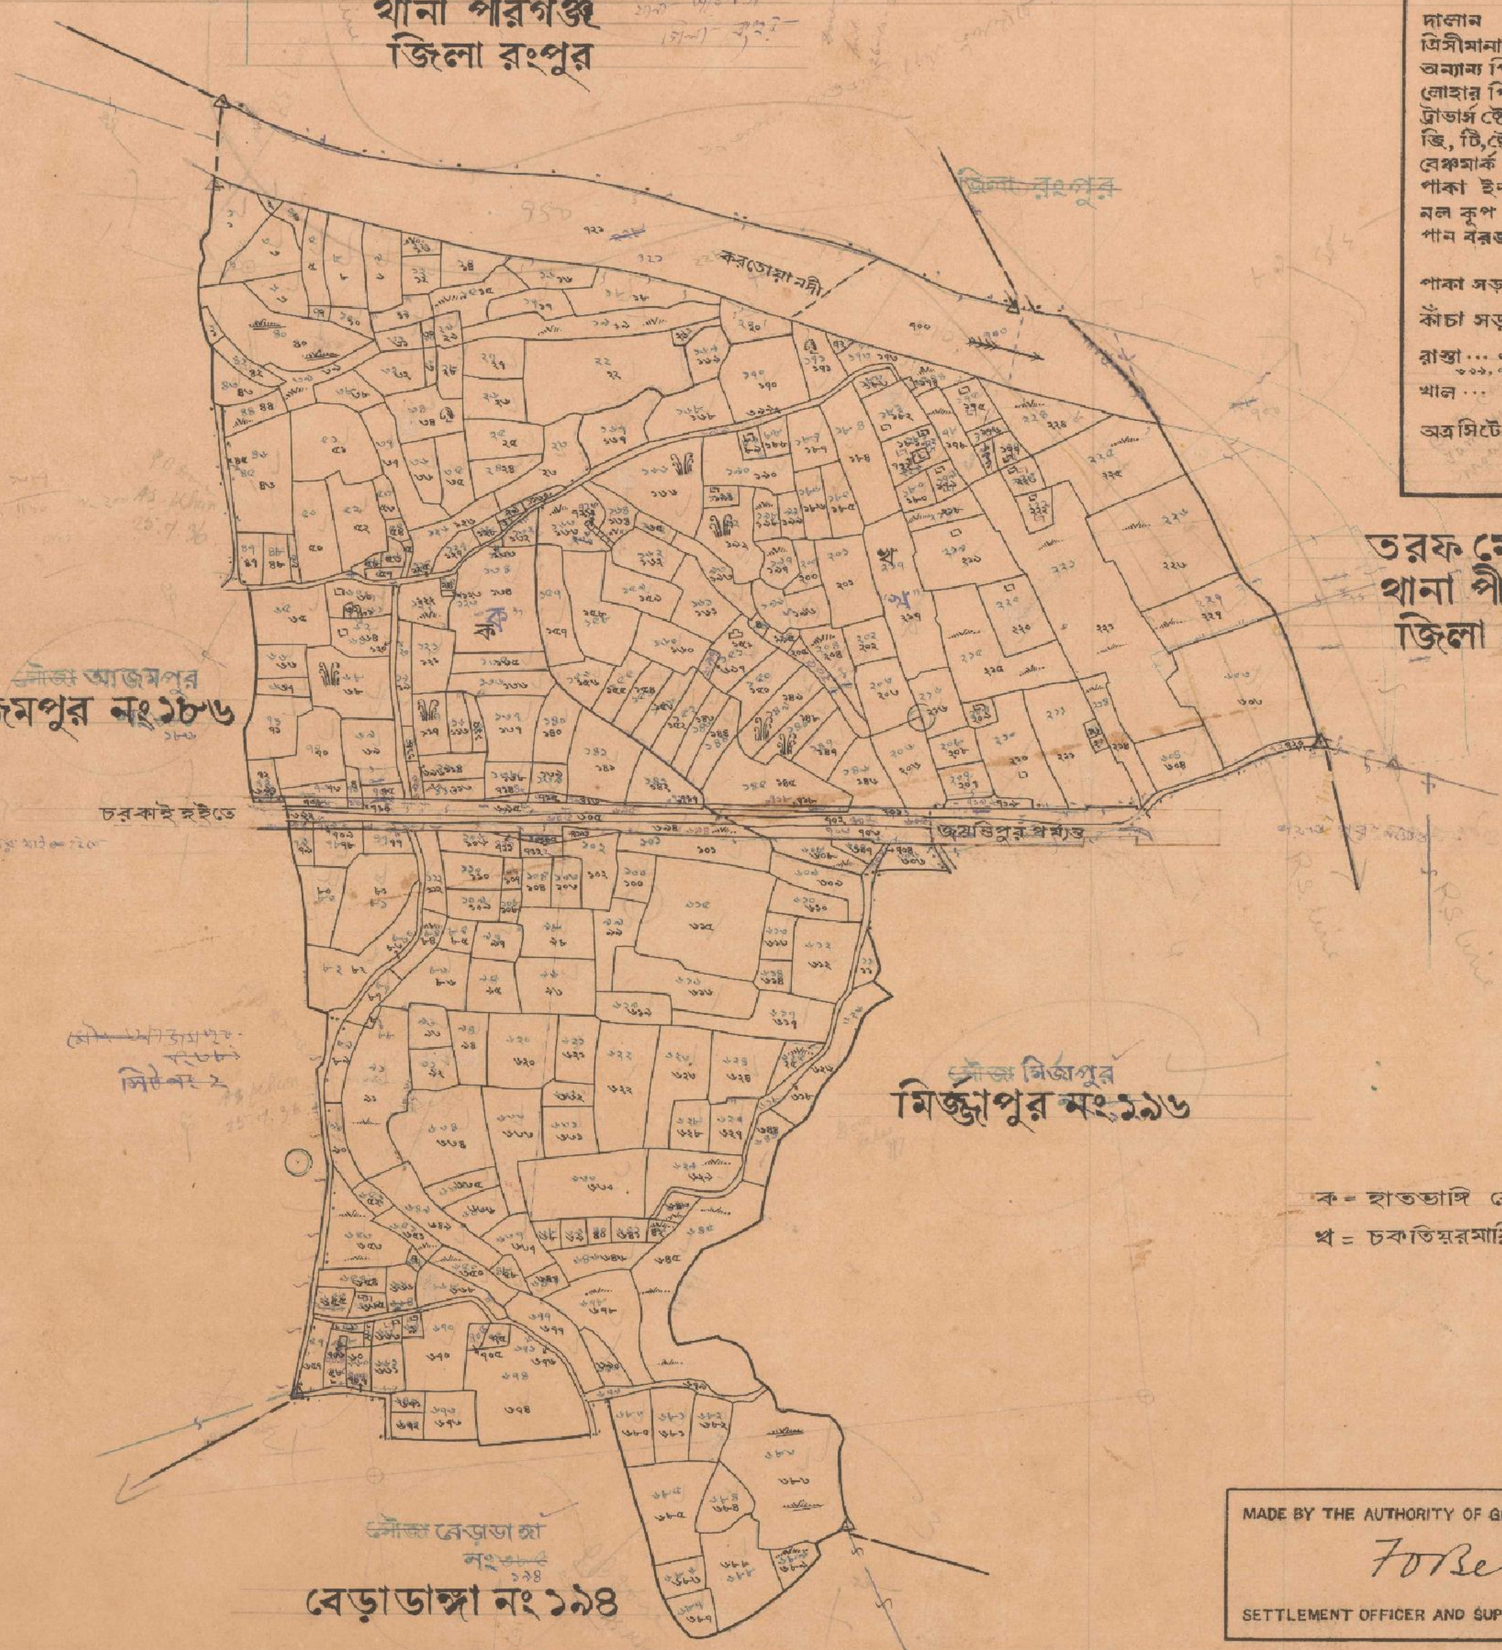

সাঙ্কেতিক

দালান ... ...
ত্রিসীমানার পিলার ... ...
অন্যান্য পিলার ... ...
লোহার পিলার ... ...
ট্রাভার্স ষ্টেসন ... ...
জি, টি, ষ্টেসন ... ...
বেঞ্চমার্ক ... ...
পাকা ইন্দারা ... ...
নল কূপ ... ...
পান বরজ ... ...

দাগ নং

পাকা সড়ক ...

কাঁচা সড়ক ... ৬০৫, ৭০২

রাস্তা ... ৪৫, ৮৩, ১২০, ১২৫, ৩১৮, ৩৭৬, ৩৭৯, ৩৯৯, ৭০৬, ৭৭৭, ৭২০

খাল ...

অত্র সিটে ভুক্ত ... ১-৪৮, ৬০-৭৫, ৭৭-১২৭, ৩০৬-৩৫৫, ৩৫৭-৩৬৩, ৩৬৫-৩৭৪, ৩৭৬-৭২৩

MADE BY THE AUTHORITY OF GOVERNMENT IN 1934-36

F. O'Bell

SETTLEMENT OFFICER AND SUPERINTENDENT OF SURVEY

NAME OF MOUZA	OLD J.L. NO	NEW J.L. NO	P. S.	DIST.
হাতভাঙ্গী	১৯৫	২৫৪	নবাবগঞ্জ	দিনাজপুর
আজমপুর	১৮৬	১৪৬	ঐ	ঐ
বেড়াডাঙ্গী	১৯৪	২৫৩	ঐ	ঐ
মির্জাপুর	১৯৬	২৫৫	ঐ	ঐ
তরফ মোজাইত	৩১	৩৬	পীরগঞ্জ	রংপুর
তিওরমারী	৩০	৩৪	ঐ	ঐ

ADOPTED FOR THE PURPOSE OF OPERATION UNDER CHAPTER IV OF THE B.B.S.A.& T.ACT, 1950, WITHOUT CORRECTION.

SETTLEMENT OFFICER & SUPERINTENDENT OF SURVEY.

(খ) চক তিওরমারি রেঃ সাঃ নং ৫৩৬৩

১৪৩-২২৭, ২২৯, ২৩০, ৩০৩, ৩০৪, ৩০৬, ৩০৭, ৩০৮, ৩১১, ৩১৮, ৩১৯, ৩৬৭-৭০৪, ৭১৮, ৭১৯, ৭২০, ৭২২, ৭২৩