জিলা দিনাজপুর

থানা বোচাগঞ্জ

মৌজা যশোহর সিট নং ২ (JASOHAR)

জে, এল, নং ১২৭

রে, সা, নং ৫১

স্কেল ১৬" = ১ মাইল

১০০ কড়িতে এক জরীপ ।

৮০ জরীপে এক মাইল ।

Kanungo	Khanapuri Amin	Khanapuri Begining	Khanapuri Ended	Muhayat Commencing	Muhayat Ended
S. Hossain	A. Gofur	[illegible]	[illegible]	16/8/36	18/8/36

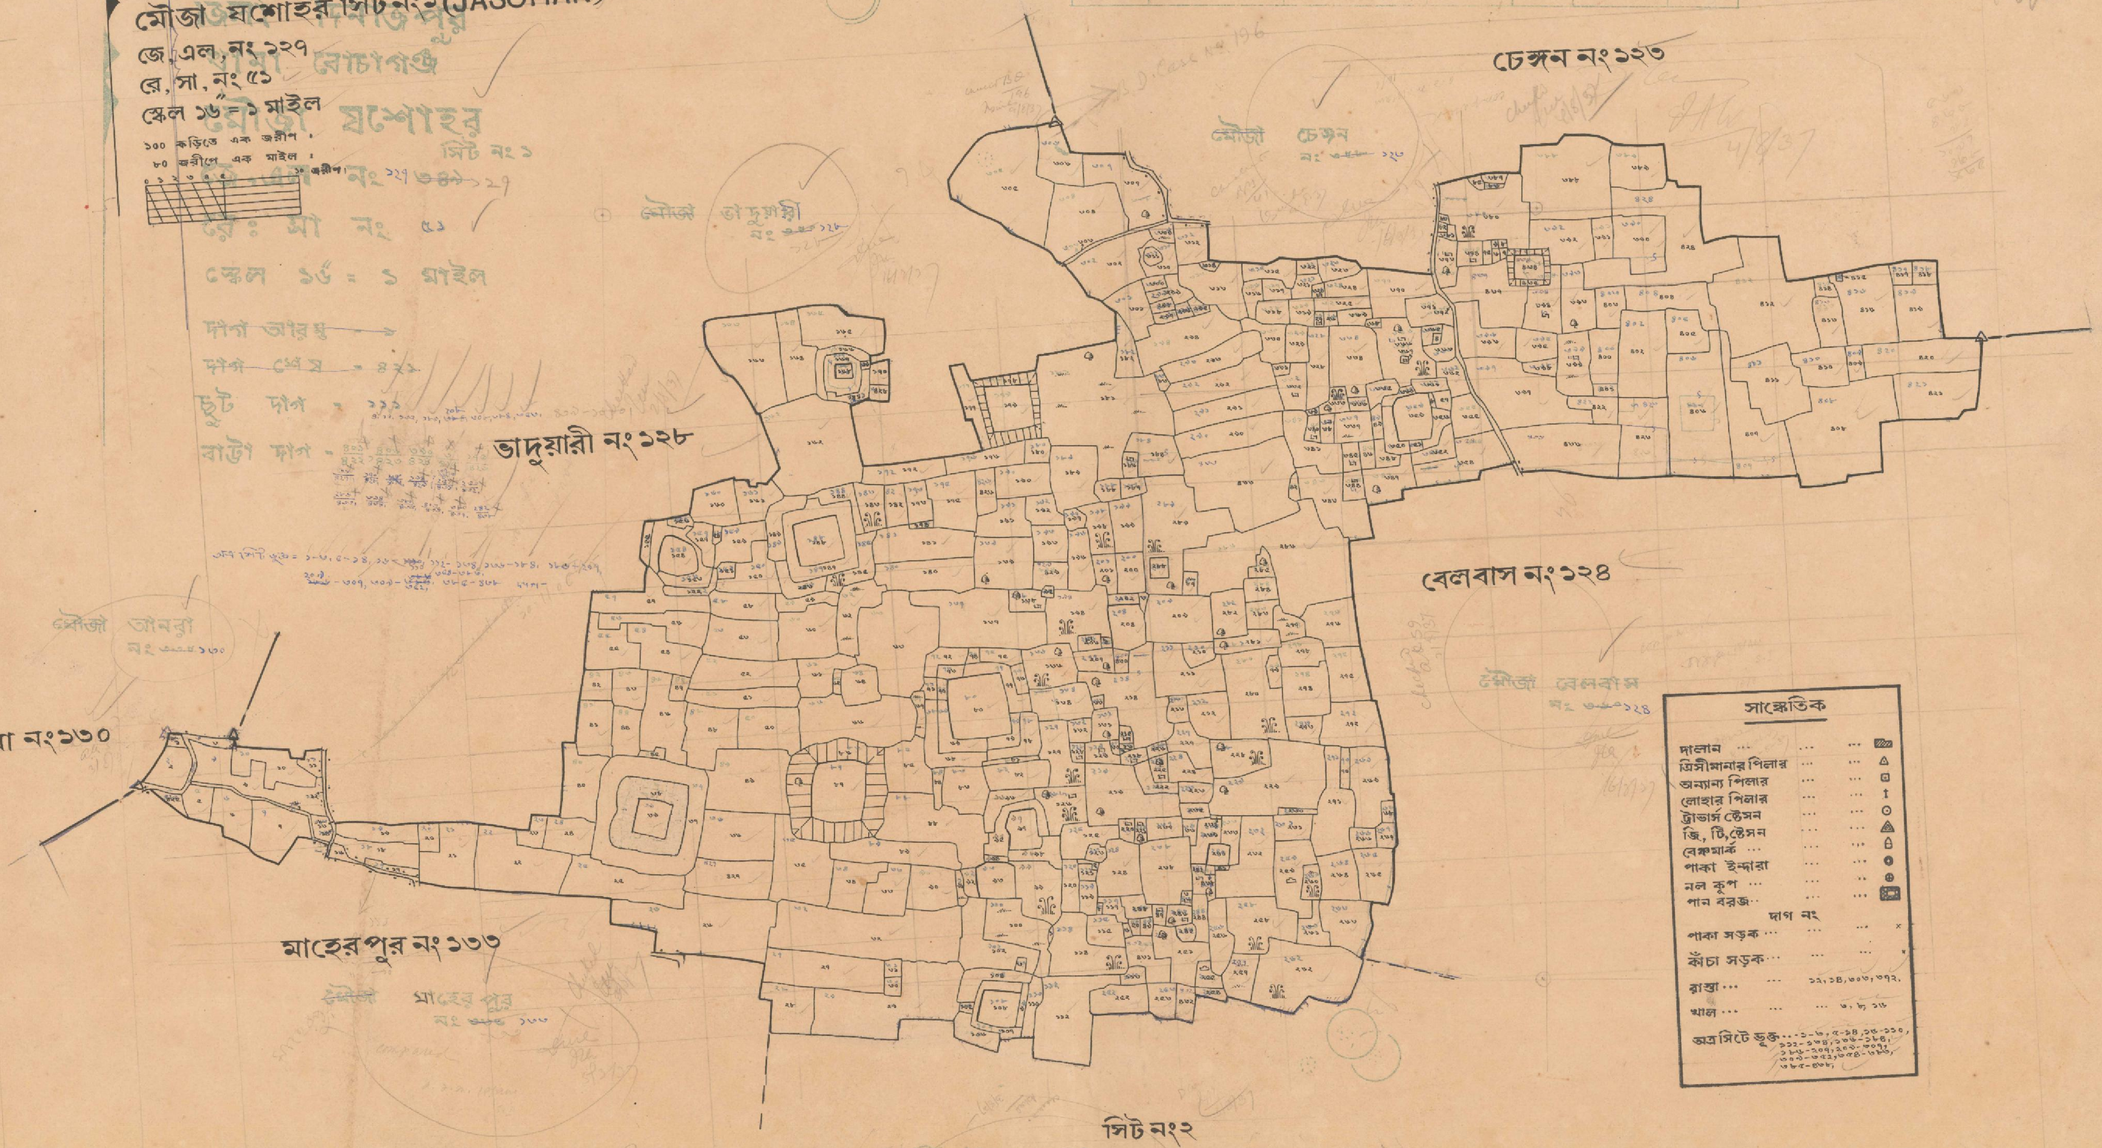

সাঙ্কেতিক

দালান	
ত্রিসীমানার পিলার	△
অন্যান্য পিলার	□
লোহার পিলার	↕
ট্রাভার্স ষ্টেসন	⊙
জি, টি, ষ্টেসন	△
বেঞ্চমার্ক	
পাকা ইন্দারা	
নল কূপ	⊕
পান বরজ	
দাগ নং	
পাকা সড়ক	×
কাঁচা সড়ক	
রাস্তা	১২, ১৪, ৩০৬, ৩৭২.
খাল	৬, ৮, ১৬
অত্রসিটে ভুক্ত	১-৬, ৫-১৪, ১৬-১১০, ১১২-১৭৪, ১৭৬-১৮৬, ১৮৯-২০৬, ২১০-২৭৭, ২৭৯-৩৭২, ৩৭৪-৩৮৬, ৩৮৮-৩৮৮,

MADE BY THE AUTHORITY OF GOVERNMENT IN 1935-37

F O Bell

SETTLEMENT OFFICER AND SUPERINTENDENT OF SURVEY

ফটো নং — দাগ নং

১৭৯-৫, ১—২৩০

১৭৭-৬ ২৩১—২৬২

১৭৮-৪, ২৬৫—৪২১

ADOPTED FOR THE PURPOSE OF OPERATION UNDER CHAPTER IV OF THE E.B.S.A.& T.ACT, 1950, WITHOUT CORRECTION.

SETTLEMENT OFFICER & SUPERINTENDENT OF SURVEY.