জিলা দিনাজপুর

থানা ফুলবাড়ী

মৌজা চৌরাইট (CHAURAIT)

জে, এল, নং ১৩১

রে, সা, নং ৫০৭১, ৫০৭২

স্কেল ১৬" = ১ মাইল

১০০ কড়িতে এক জরীপ।
৮০ জরীপে এক মাইল।

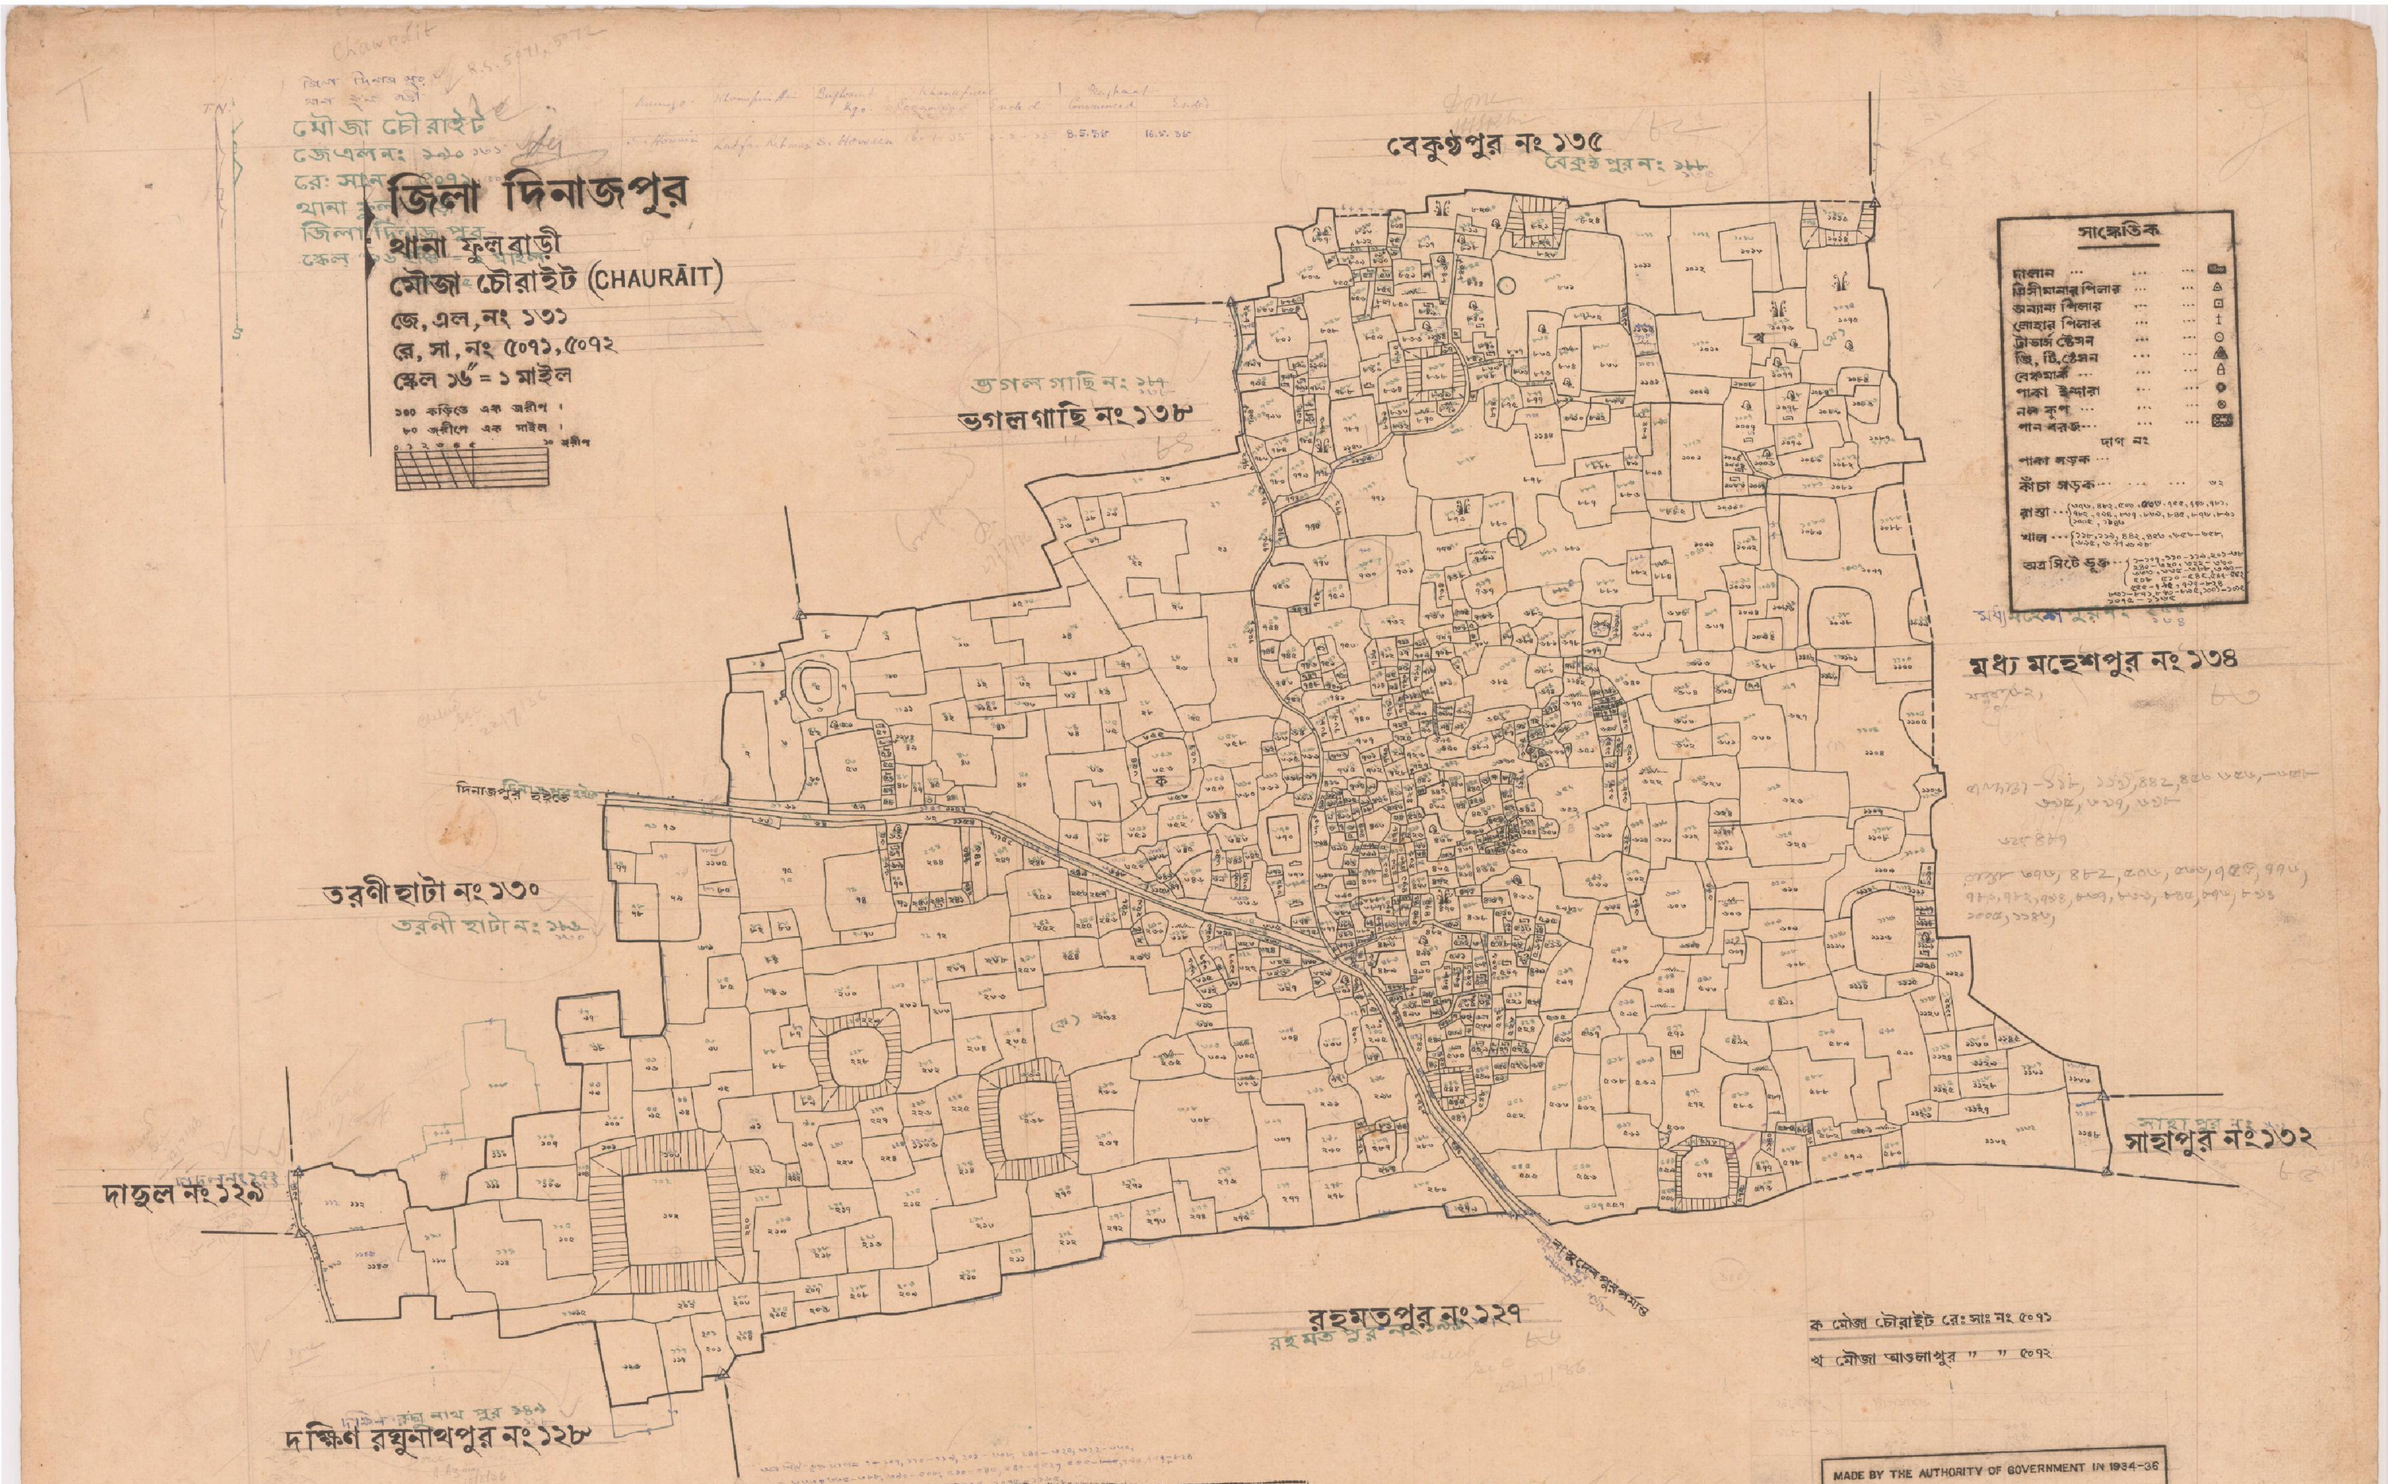

ক মৌজা চৌরাইট রেঃ সাঃ নং ৫০৭১

খ মৌজা আওলাপুর " " ৫০৭২

NAME OF MOUZA	OLD J.L. NO	NEW J.L. NO	P.S.	DIST
চৌরাইট	১৩১	৮১		
তরণী হাটা	১৩০	৮২		
দাদুল	১২৯	৮৩		
দক্ষিণ রঘুনাথ পুর	১২৮	২৩		
রহমত পুর	১২৭	৮৪		
সাহাপুর	১৩২	৮৫		
মধ্য মহেশ পুর	১৩৪	৮৩		
বেকুণ্ঠ পুর	১৩৫	৮২		
ভগলগাছি	১৩৮	৮১		

ADOPTED FOR THE PURPOSE OF OPERATION UNDER CHAPTER IV OF THE E.B.S.A.R. T. ACT, 1950, WITHOUT CORRECTION.

SETTLEMENT OFFICER & SUPERINTENDENT OF SURVEY.

MADE BY THE AUTHORITY OF GOVERNMENT IN 1934-36

F.O. Bell

SETTLEMENT OFFICER AND SUPERINTENDENT OF SURVEY