Name of Survey						Khana-puri Report			
Kanungo	Kanungo Amin	Khanapuri Amin	Kanungo	Consigned Cadd	Enclosed	Consigned Cadd	Enclosed	Consigned Cadd	Enclosed
		Sabyasachi Chifan	Gunamoy Roy					2.6.35	3.6.35

জিলা দিনাজপুর

থানা নবাবগঞ্জ

মৌজা ধানজুড়ী কালীসহর (DHĀNJURI-KĀLISAHAR) সিট নং ৩

জে, এল, নং ৪২

রে, সা, নং ৫৫৪৮

স্কেল ১৬" = ১ মাইল

১০০ কাঠিতে এক জরীপ।

৮০ জরীপে এক মাইল।

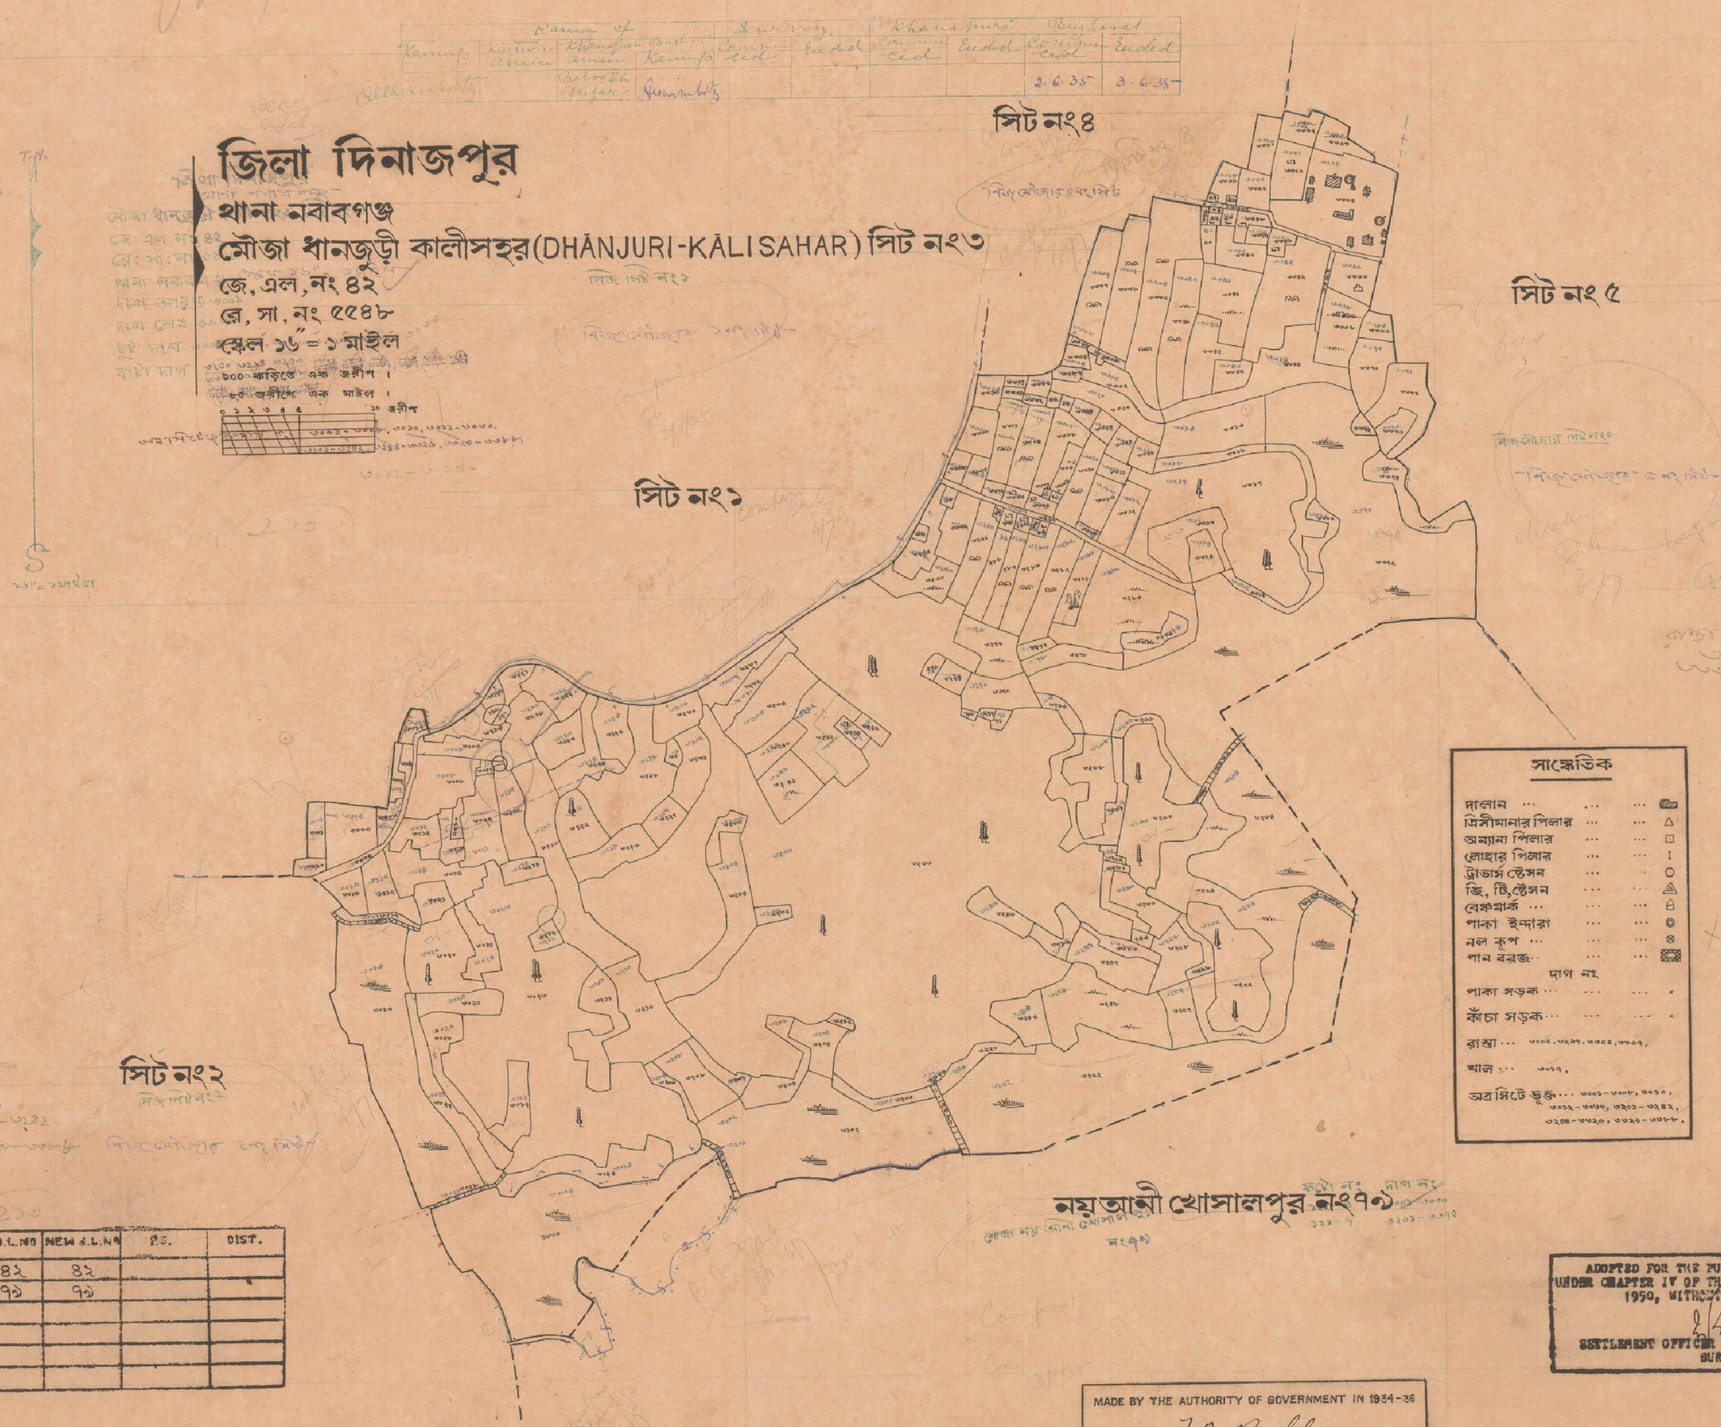

সাঙ্কেতিক

দালান	
ত্রিসীমানার পিলার	△
অন্যান্য পিলার	□
লোহার পিলার	I
ট্রাভার্স ষ্টেসন	○
জি, টি, ষ্টেসন	△
বেঞ্চমার্ক	
পাকা ইন্দারা	
নল কূপ	⊗
পান বরজ	

দাগ নং

পাকা সড়ক	
কাঁচা সড়ক	
রাস্তা ...	৩০০৪, ৩২৯৭, ৩৩৫৫, ৩৩৩৭,
খাল ...	৩০১৭,
অত্র সিটে ভুক্ত ...	৩০০১–৩০০৮, ৩০১০, ৩০১২–৩০১৬, ৩২০১–৩২৪২, ৩২৪৪–৩২৫০, ৩২৫২–৩৩৮৮,

NAME OF MOUZA	OLD J.L. NO	NEW J.L. NO	P.S.	DIST.
ধানজুড়ী কালীসহর	৪২	৪২		
নয়আনী খোসালপুর	৭১	৭১		

ADOPTED FOR THE PURPOSE OF OPERATION UNDER CHAPTER IV OF THE E.B.S.A.& T. ACT, 1950, WITHOUT CORRECTION.

SETTLEMENT OFFICER & SUPERINTENDENT OF SURVEY.

MADE BY THE AUTHORITY OF GOVERNMENT IN 1934-36

F.O. Bell

SETTLEMENT OFFICER AND SUPERINTENDENT OF SURVEY