জিলা দিনাজপুর

থানা ফুলবাড়ী

মৌজা শ্রীকৃষ্ণপুর (SRIKRISHNAPUR)

জে, এল, নং ১১৩

রে, সা, নং ৪৭১৩, ৫০৫২

স্কেল ১৬" = ১ মাইল

১০০ কড়িতে এক জরীপ।
৮০ জরীপে এক মাইল।

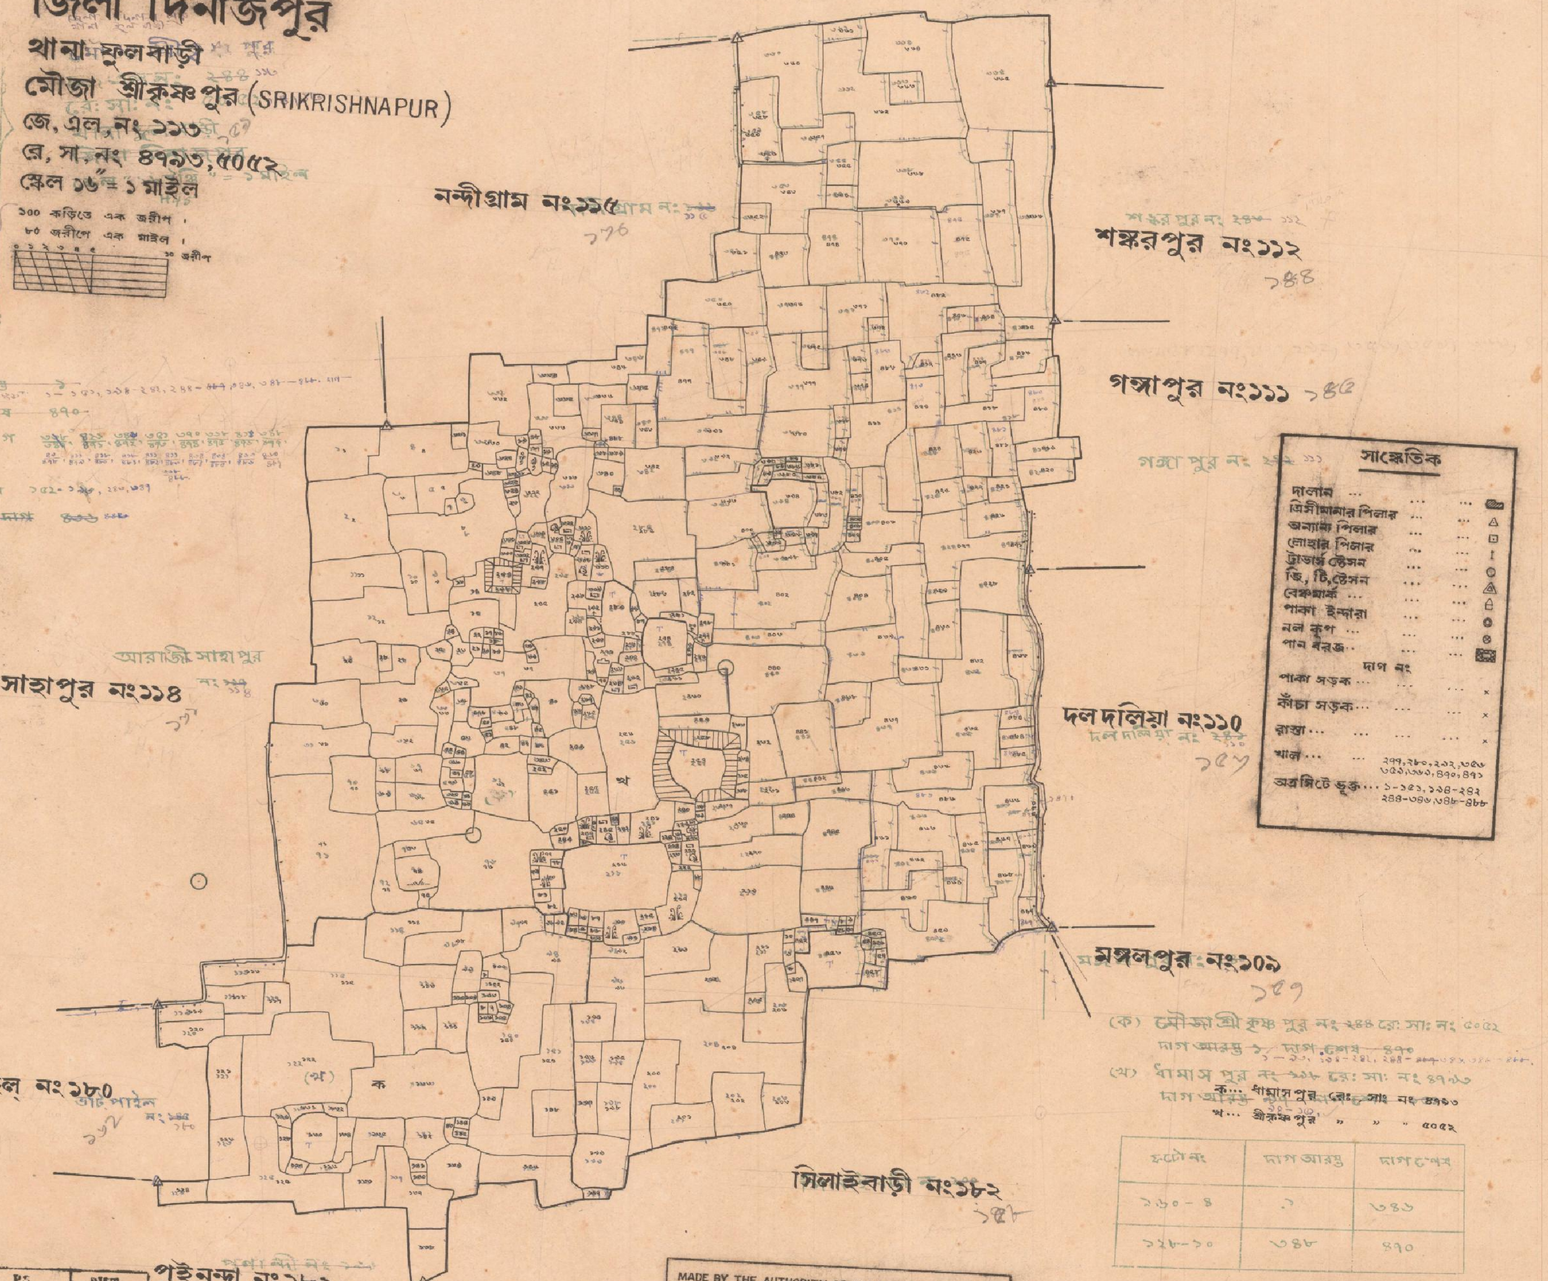

সাঙ্কেতিক

দালান ...	
মিসীমানার পিলার ...	△
অন্যান্য পিলার ...	▷
লোহার পিলার ...	I
ট্রাভার্স ষ্টেসন ...	○
জি, টি, ষ্টেসন ...	△
বেঞ্চমার্ক ...	△
পাকা ইন্দারা ...	⊙
নল কূপ ...	⊙
পান বরজ ...	
দাগ নং	
পাকা সড়ক ...	×
কাঁচা সড়ক ...	×
রাস্তা ...	×
খাল ...	১৭৭, ২৮০, ২৯২, ৩৫৬, ৩৫৯, ৩৬৬, ৪৭৮, ৪৭১
অব্রিটে ভুক্ত ...	১-১৫১, ১৬৪-২৪২, ২৪৪-৩৬৬, ৩৪৮-৪৮৮

(ক) মৌজা শ্রী কৃষ্ণ পুর নং ১১৪ রে: সা: নং ৫০৫২
দাগ আরম্ভ ১, দাগ শেষ ৪৭০
(খ) ধামাস পুর নং ১১৮ রে: সা: নং ৪৭১৩
ক... ধামাস পুর রে: সা: নং ৪৭১৩
খ... শ্রীকৃষ্ণ পুর " " " ৫০৫২

প্লটো নং	দাগ আরম্ভ	দাগ শেষ
১৬০-৪	১	৩৪৬
১২৮-১০	৩৪৮	৪৭০

No.	NAME OF MOUZA	OLD J.L.No	NEW J.L.No	P.S.	DIST.
	শ্রীকৃষ্ণপুর	১১৩	১৫৯		
	নন্দিগ্রাম	১১৫	১৬০		
	আরাজিসাহাপুর	১১৪	১৬১		
	ভাটপাইল	১৮০	১৬২		
	পুইনন্দা	১৮১	১৬৩		
	সিলাইবাড়ী	১৮২	১৬৮		
	মঙ্গলপুর	১০৯	১৫৭		
	দলদলিয়া	১১০	১৫৬		
	গঙ্গাপুর	১১১	১৪৫		
	শঙ্করপুর	১১২	১৪৪		
	খড়মপুর	১২২	১৪৩		

MADE BY THE AUTHORITY OF GOVERNMENT IN 1934-36

SETTLEMENT OFFICER AND SUPERINTENDENT OF SURVEY

ADOPTED FOR THE PURPOSE OF OPERATION UNDER CHAPTER IV OF THE E.B.S.A.& T. ACT, 1950, WITHOUT CORRECTION.

SETTLEMENT OFFICER & SUPERINTENDENT OF SURVEY.