Halka No 46

Kanungo	Kiswar Amin	Khanapuri Amin	Bujharat Kanungo	Survey		Khanapuri		Bujharat	
				Commenced	Ended	Commenced	Ended	Commenced	Ended
A.K. Mukharjee		Kalimuddi Ajahar Ali Ashraf Ali				23.5.35	14.8.35	15.5.35	24.5.35

জিলা দিনাজপুর
থানা ফুলবাড়ী
মৌজা অম্রবাড়ী (AMRABARI)
জে, এল, নং ৬৫
রে, সা, নং ৫১১০
স্কেল ১৬" = ১ মাইল

১০০ কড়িতে এক জরীপ।
৮০ জরীপে এক মাইল।

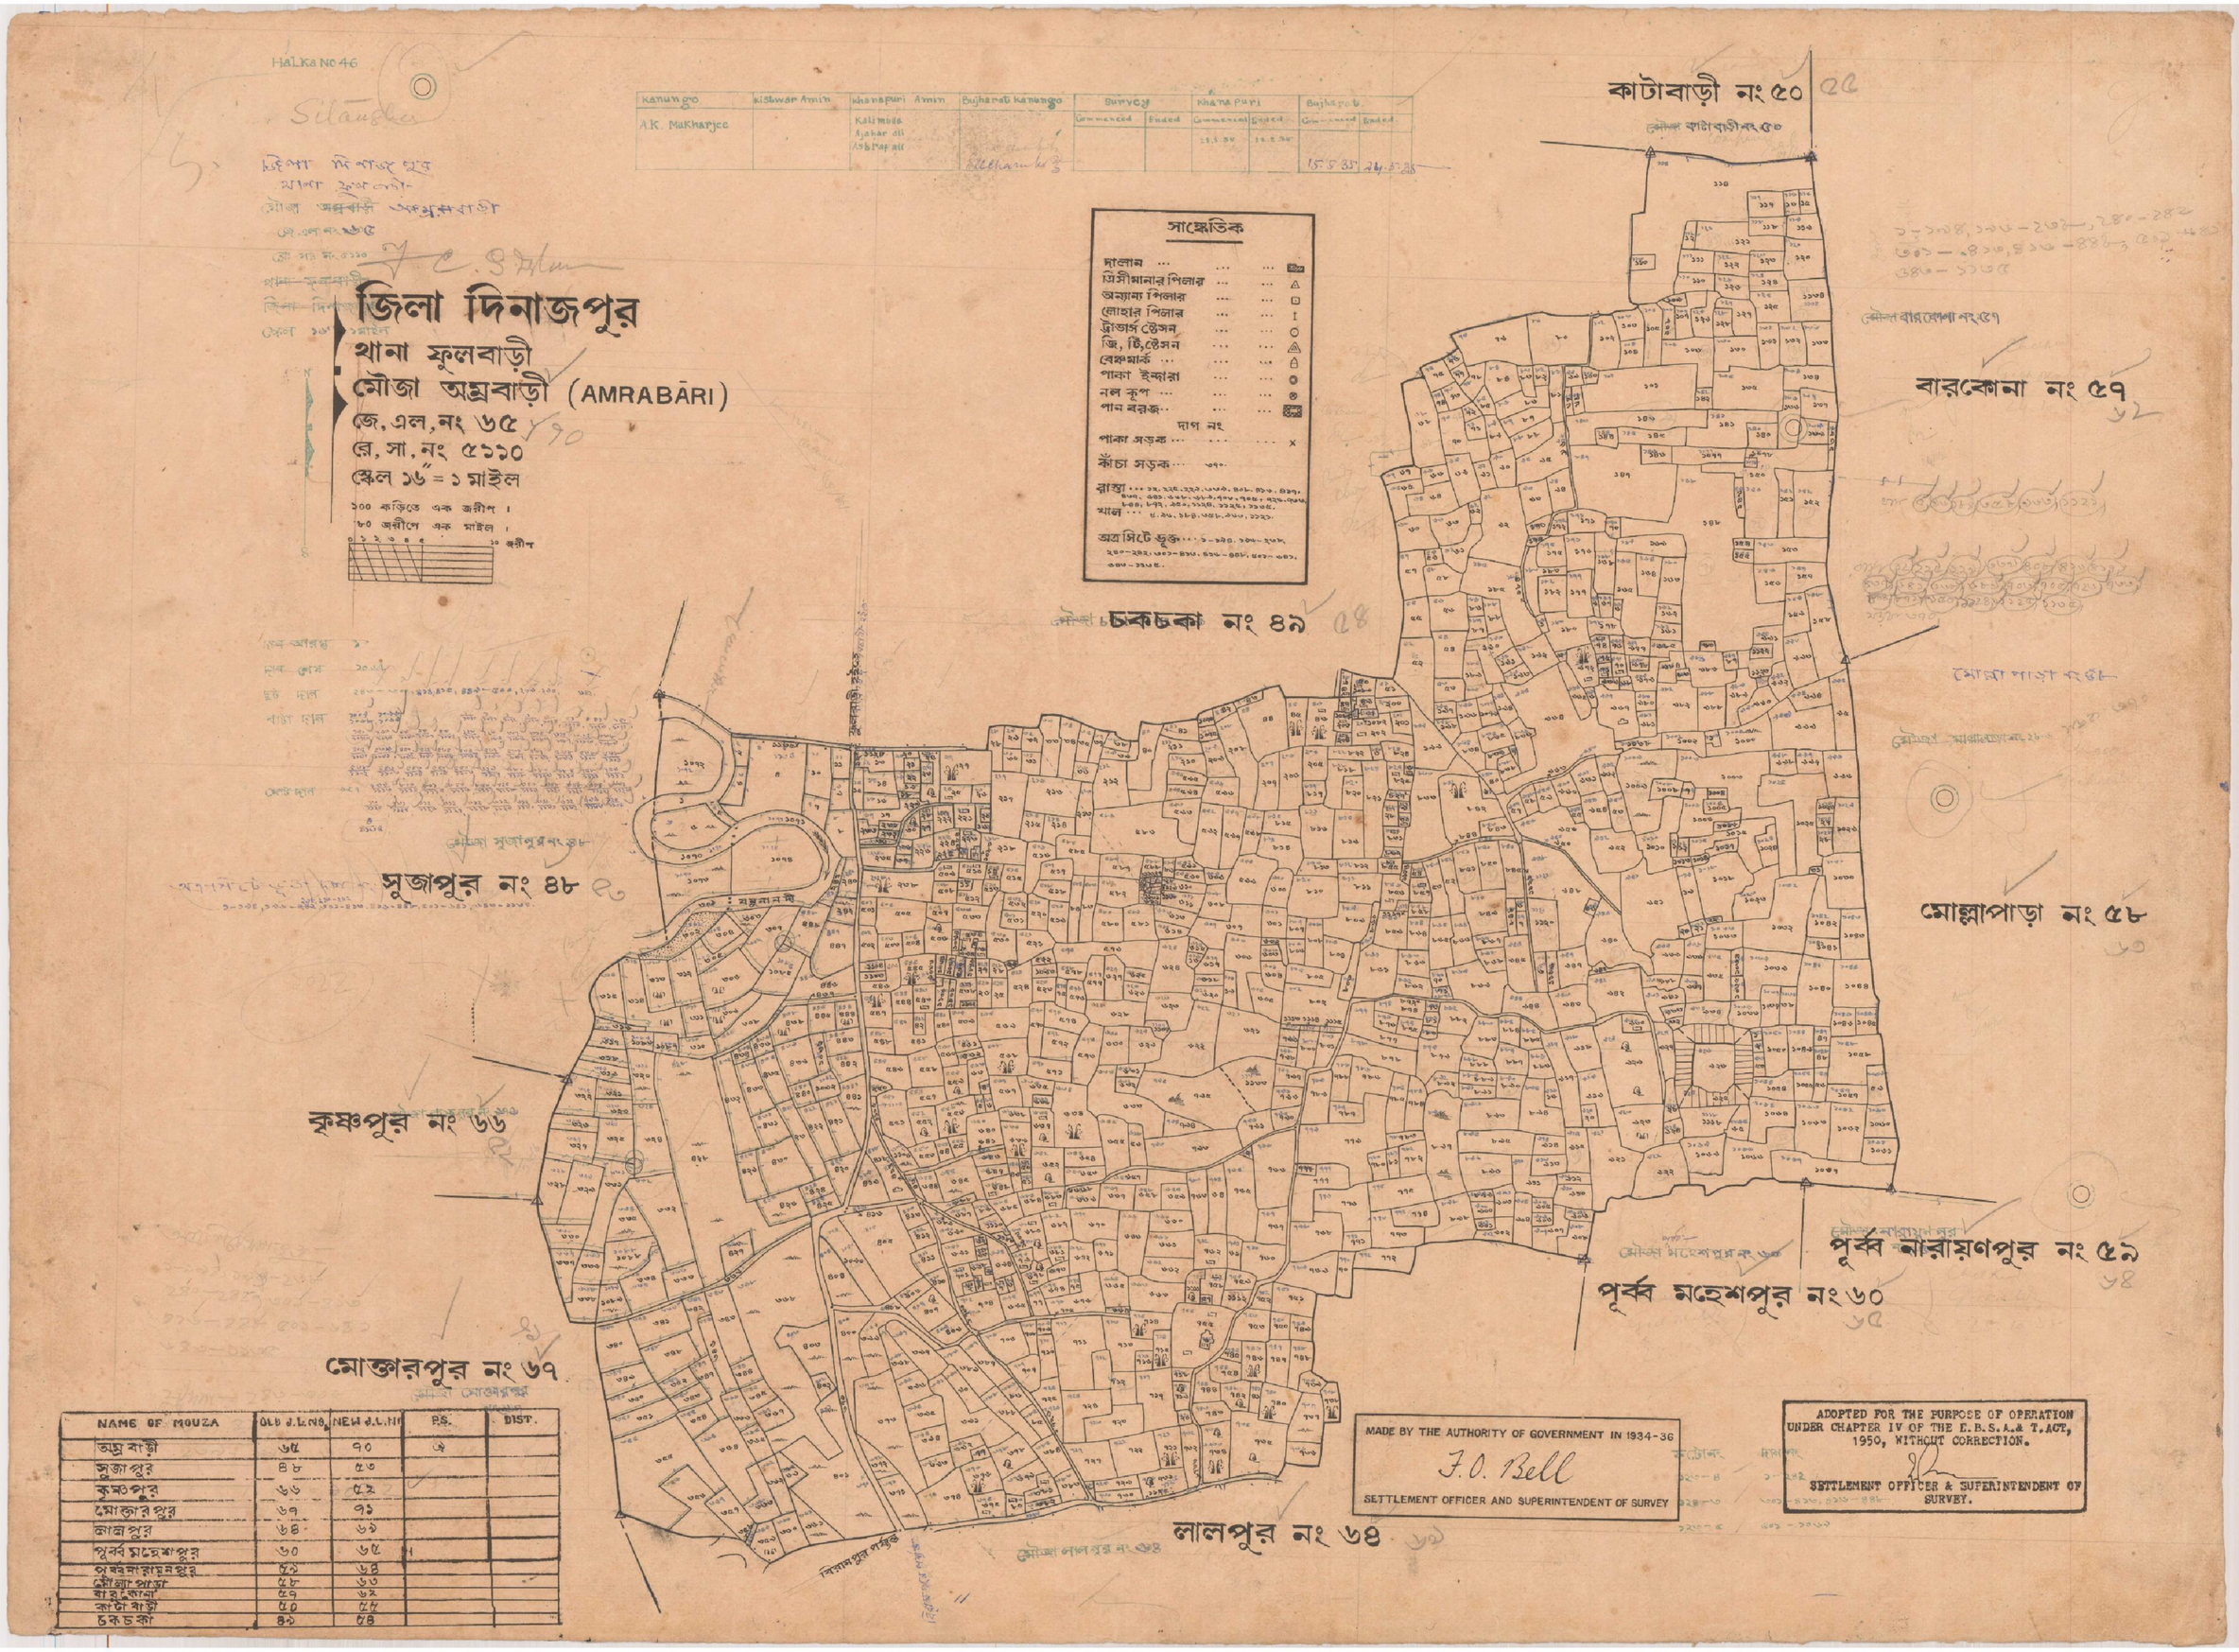

NAME OF MOUZA	OLD J.L.NO.	NEW J.L.NO.	P.S.	DIST.
অম্রবাড়ী	৬৫	৭০		
সুজাপুর	৪৮	৫৩		
কৃষ্ণপুর	৬৬	৫২		
মোক্তারপুর	৬৭	৭১		
নালপুর	৬৪	৬৯		
পূর্ব্ব মহেশপুর	৬০	৬৫		
পূর্ব্বনারায়নপুর	৫৯	৬৪		
মোল্লাপাড়া	৫৮	৬৩		
বারকোনা	৫৭	৬২		
কাটাবাড়ী	৫০	৫৫		
চকচকা	৪৯	৫৪		

MADE BY THE AUTHORITY OF GOVERNMENT IN 1934-36
F.O. Bell
SETTLEMENT OFFICER AND SUPERINTENDENT OF SURVEY

ADOPTED FOR THE PURPOSE OF OPERATION UNDER CHAPTER IV OF THE E.B.S.A.& T.ACT, 1950, WITHOUT CORRECTION.
SETTLEMENT OFFICER & SUPERINTENDENT OF SURVEY.