# জিলা দিনাজপুর

থানা বোচাগঞ্জ

মৌজা মোল্লাপাড়া সিট নং২ (MOLLĀPĀRĀ)

জে, এল, নং ১০১

রে, সা, নং ৭১

স্কেল ১৬" = ১ মাইল

১০০ কড়িতে এক জরীপ।
৮০ জরীপে এক মাইল।

| Kanango | Kistwar Amin | Khanapuri Amin | Bujharat K.go. | Kistwar Commenced | Kistwar Ended | Khanapuri Commenced | Khanapuri Ended | Bujharat Commenced | Bujharat Ended |
|---|---|---|---|---|---|---|---|---|---|
| 1 | 2 | 3 | 4 | 5 | 6 | 7 | 8 | 9 | 10 |
| S. K. Chakraborty. | [illegible] | [illegible] Ahammed. | Sekh [illegible] | [illegible] | [illegible] | [illegible] 35. | 19.12.35. | 13.4.36 | 15.4.36 |

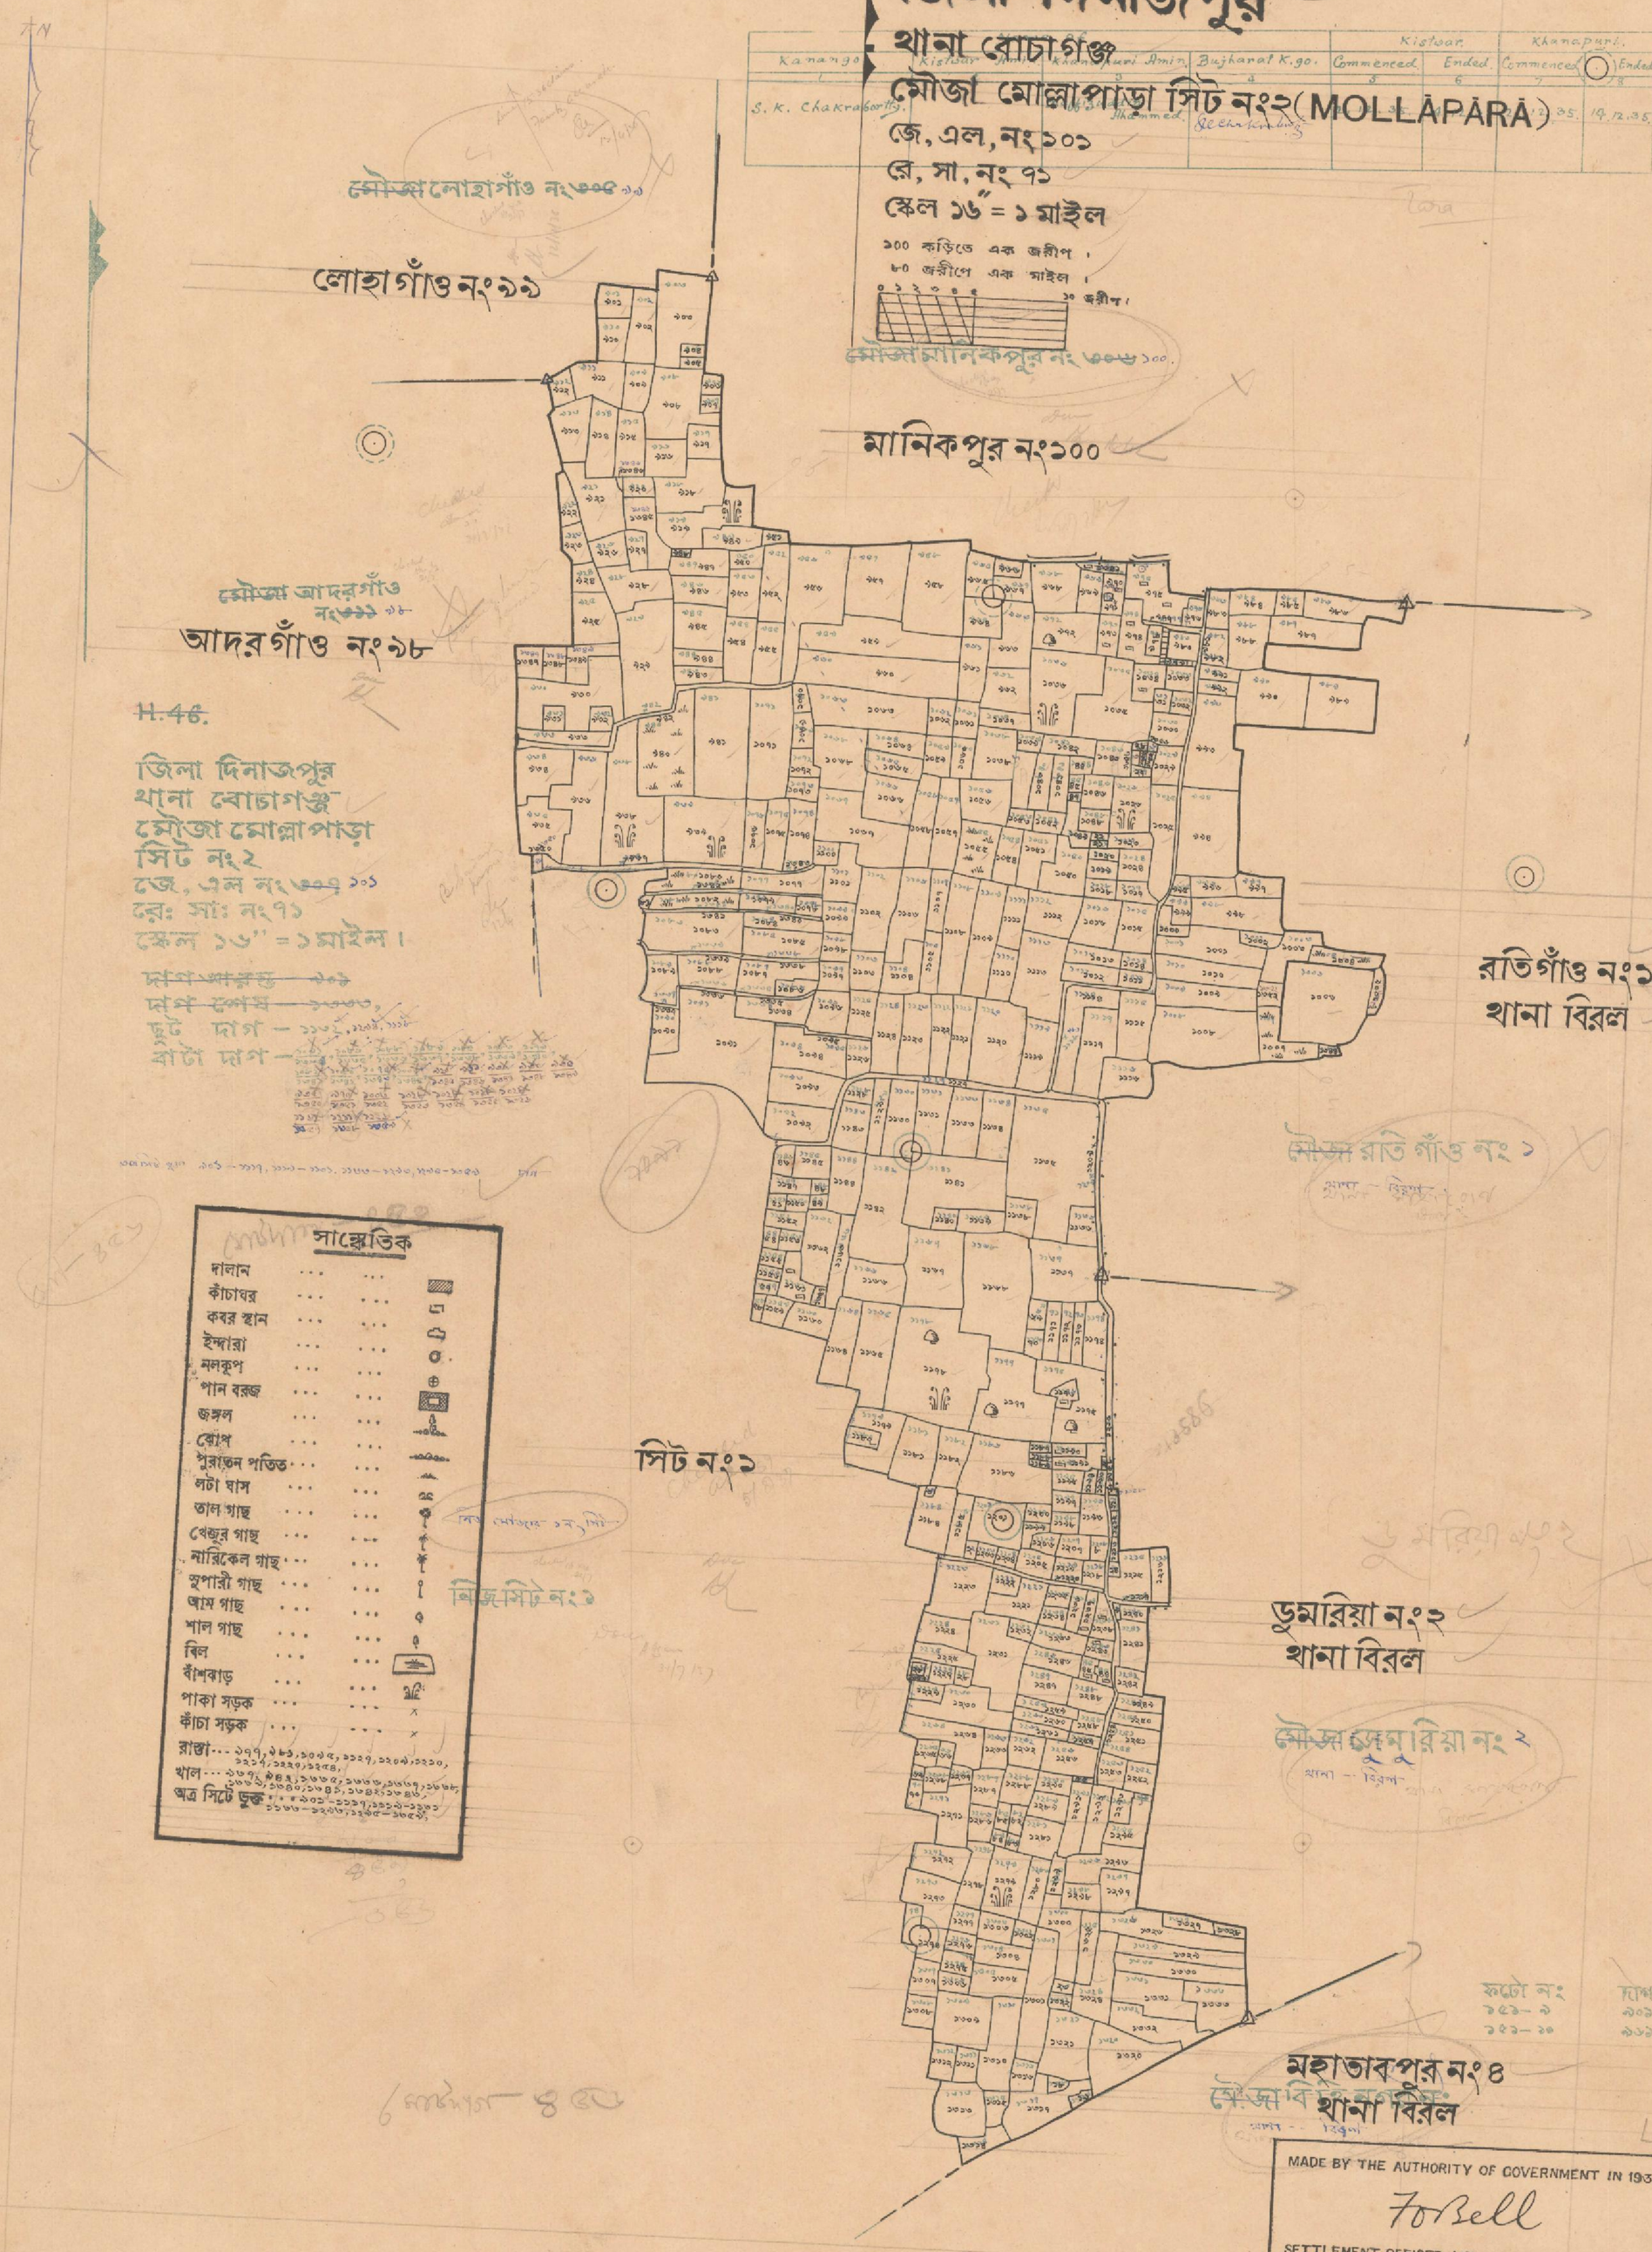


H. 46.

জিলা দিনাজপুর
থানা বোচাগঞ্জ
মৌজা মোল্লাপাড়া
সিট নং ২
জে, এল নং ১০১
রে: সাঃ নং ৭১
স্কেল ১৬" = ১ মাইল।

দাগ আরম্ভ —
দাগ শেষ —
ছুট দাগ —
বাটা দাগ —

## সাঙ্কেতিক

| | |
|---|---|
| দালান | |
| কাঁচাঘর | |
| কবর স্থান | |
| ইন্দারা | |
| নলকূপ | |
| পান বরজ | |
| জঙ্গল | |
| ঝোপ | |
| পুরাতন পতিত | |
| লটা ঘাস | |
| তাল গাছ | |
| খেজুর গাছ | |
| নারিকেল গাছ | |
| সুপারী গাছ | |
| আম গাছ | |
| শাল গাছ | |
| বিল | |
| বাঁশঝাড় | |
| পাকা সড়ক | |
| কাঁচা সড়ক | |

রাস্তা ... ১৭৭, ১৮১, ১০০৫, ১১২৭, ১২০৮, ১২১০, ১২১৭, ১২২৭, ১২৭৪,
খাল ... ১৬৭, ১৮৪, ১৬৩৫, ১৬৩৬, ১৬৩৭, ১৬৩৮, ১৬৪০, ১৬৪১, ১৬৪২, ১৬৪৬,
অত্র সিটে ভুক্ত ... ১২০২–১২১৭, ১২১৯–১২৬১, ১২৬৬–১২৬৭, ১২৬৫–১৬৫৩,

MADE BY THE AUTHORITY OF GOVERNMENT IN 1935-37

F. O. Bell

SETTLEMENT OFFICER AND SUPERINTENDENT OF SURVEY

ADOPTED FOR THE PURPOSE OF OPERATION UNDER CHAPTER IV OF THE E.B.S.A.& T.ACT, 1950, WITHOUT CORRECTION.

SETTLEMENT OFFICER & SUPERINTENDENT OF SURVEY.