T.S. 205

জিলা দিনাজপুর
থানা ফুলবাড়ী
মৌজা আমাইল
জে.এল নং ২০৫
রেঃসাঃ নং ৪৭৬২, ৪৬৭৬

জিলা দিনাজপুর

থানা ফুলবাড়ী

মৌজা আমাইল (ĀMĀIL)

জে, এল, নং ২০৫

রে. সা. নং ৪৬৫৬, ৪৭৬২

স্কেল ১৬ = ১ মাইল

১০০ কড়িতে এক জরীপ।

৮০ জরীপে এক মাইল।

				Survey		Khanapuri		Bujharat
			Bujharat Kanungo	commenced	Ended	commenced	Ended	commenced
N.M. Chakrabortty	Khanapur Amin	Dwarakanath Nag	N.M. Chakrabortty					

সাঙ্কেতিক

- দালান ... ...
- ত্রিসীমানার পিলার ... ... △
- অন্যান্য পিলার ... ... ⊡
- লোহার পিলার ... ... ↕
- ট্রাভার্স ষ্টেসন ... ... ○
- জি, টি, ষ্টেসন ... ... △
- বেঞ্চমার্ক ... ...
- পাকা ইন্দারা ... ... ●
- নল কূপ ... ...
- পান বরজ ... ...

দাগ নং

- পাকা সড়ক ... ... ×
- কাঁচা সড়ক ... ... ×
- রাস্তা ...
- খাল ...
- অত্র সিটে ভুক্ত ...

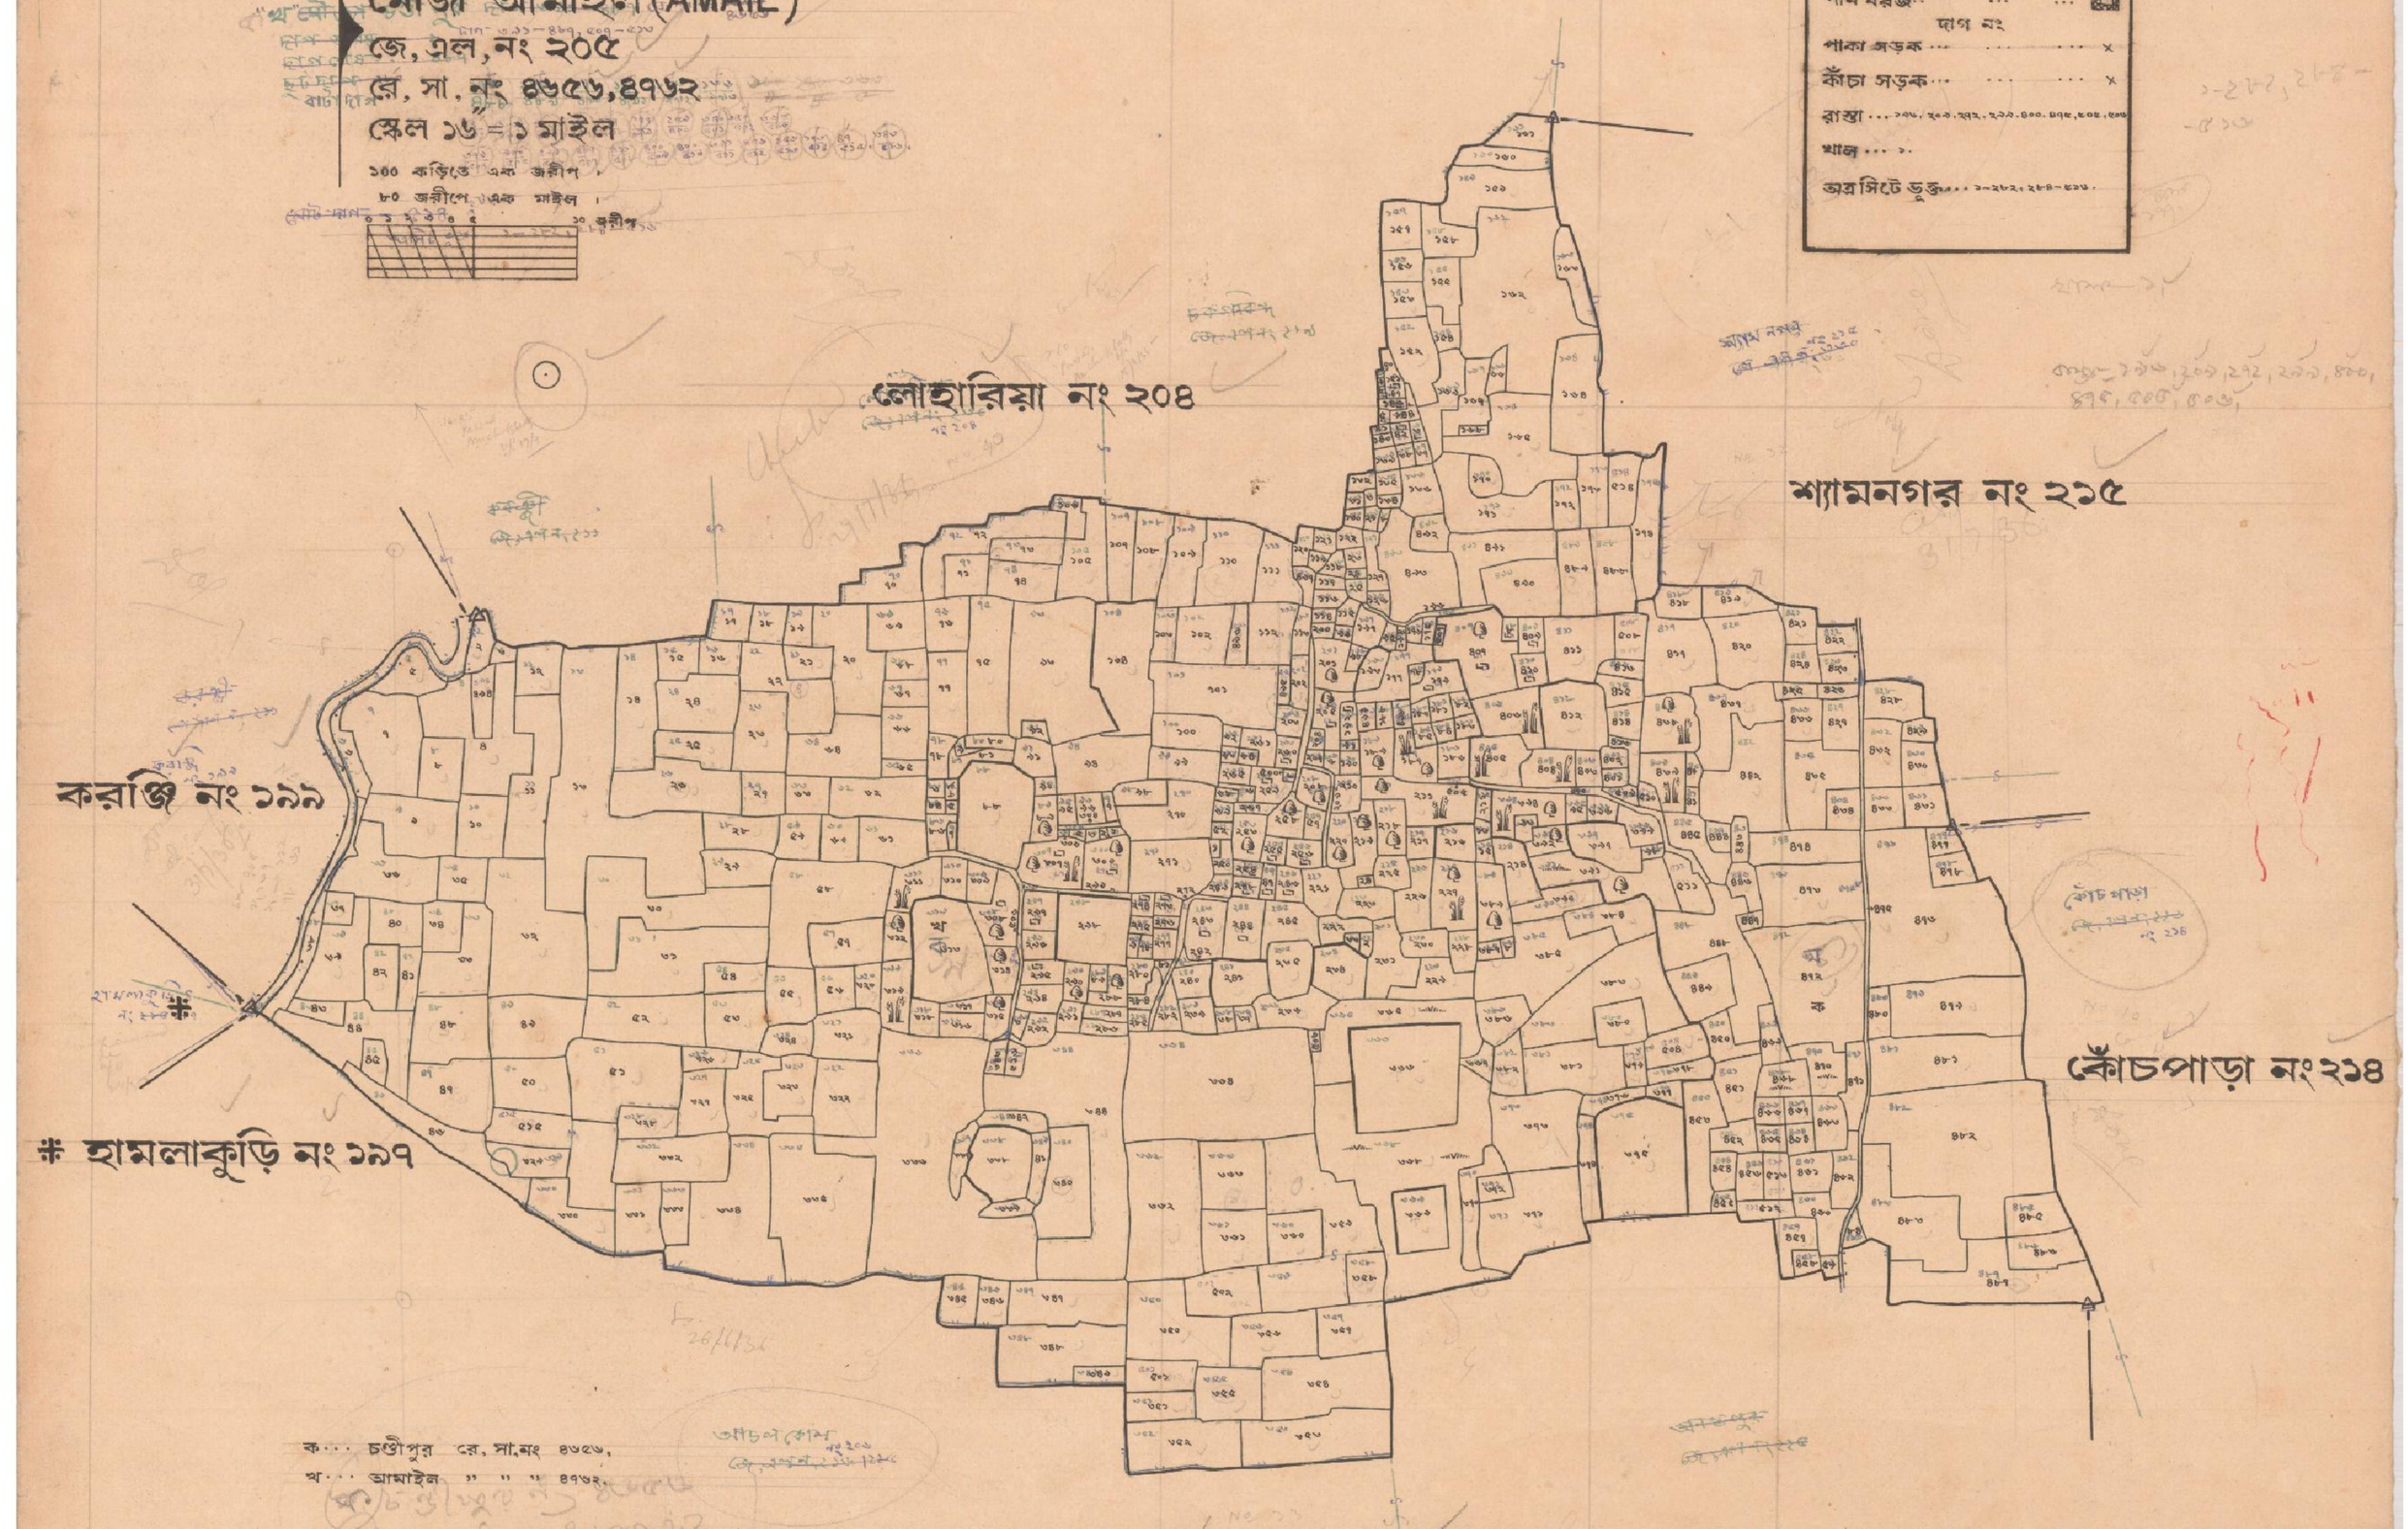

ক... চণ্ডীপুর রে. সা. নং ৪৩৫৬,
খ... আমাইল " " " ৪৭৬২,

NAME OF MOUZA	OLD J.L.NO	NEW J.L.NO	P.S.	DIST.
আমাইল	২০৫	২০৬		
লোহারিয়া	২০৪	২০২		
করঞ্জি	১৯৯	২০৪		
হামলা কুড়ি	১৯৭	২০৭		
আচল কোল	২০৬	২০৮		
কোঁচ পাড়া	২১৪	২১৪		
শ্যাম নগর	২১৫	২০১		

MADE BY THE AUTHORITY OF GOVERNMENT IN 1934-36

F.O. Bell

SETTLEMENT OFFICER AND SUPERINTENDENT OF SURVEY

ADOPTED FOR THE PURPOSE OF OPERATION UNDER CHAPTER IV OF THE E.B.S.A.& T.ACT, 1950, WITHOUT CORRECTION.

SETTLEMENT OFFICER & SUPERINTENDENT OF SURVEY.