জিলা দিনাজপুর

থানা ফুলবাড়ী

মৌজা একইর (EKAIR) সিট নং ২

জে, এল, নং ১০৮

রে, সা, নং ৪৭৮৩, ৪৭৮৮, ৫০৫৭

স্কেল ১৬" = ১ মাইল

১০০ কড়িতে এক জরীপ,
৮০ জরীপে এক মাইল,

Name of Kistwar union	Name of Khanapara union	Name of Bujhara-Kamungo	Survey Commenced	Survey Ended	Khanapara Commenced	Khanapara Ended	Bujhara Commenced	Bujhara Ended
Krishna Prasad Majumder	Krishna Prasad Majumder	Jivallal	1-3-35	2-3-35	3-3-35	10-3-35	13.6.35	15.6.35
3	4		5	6				

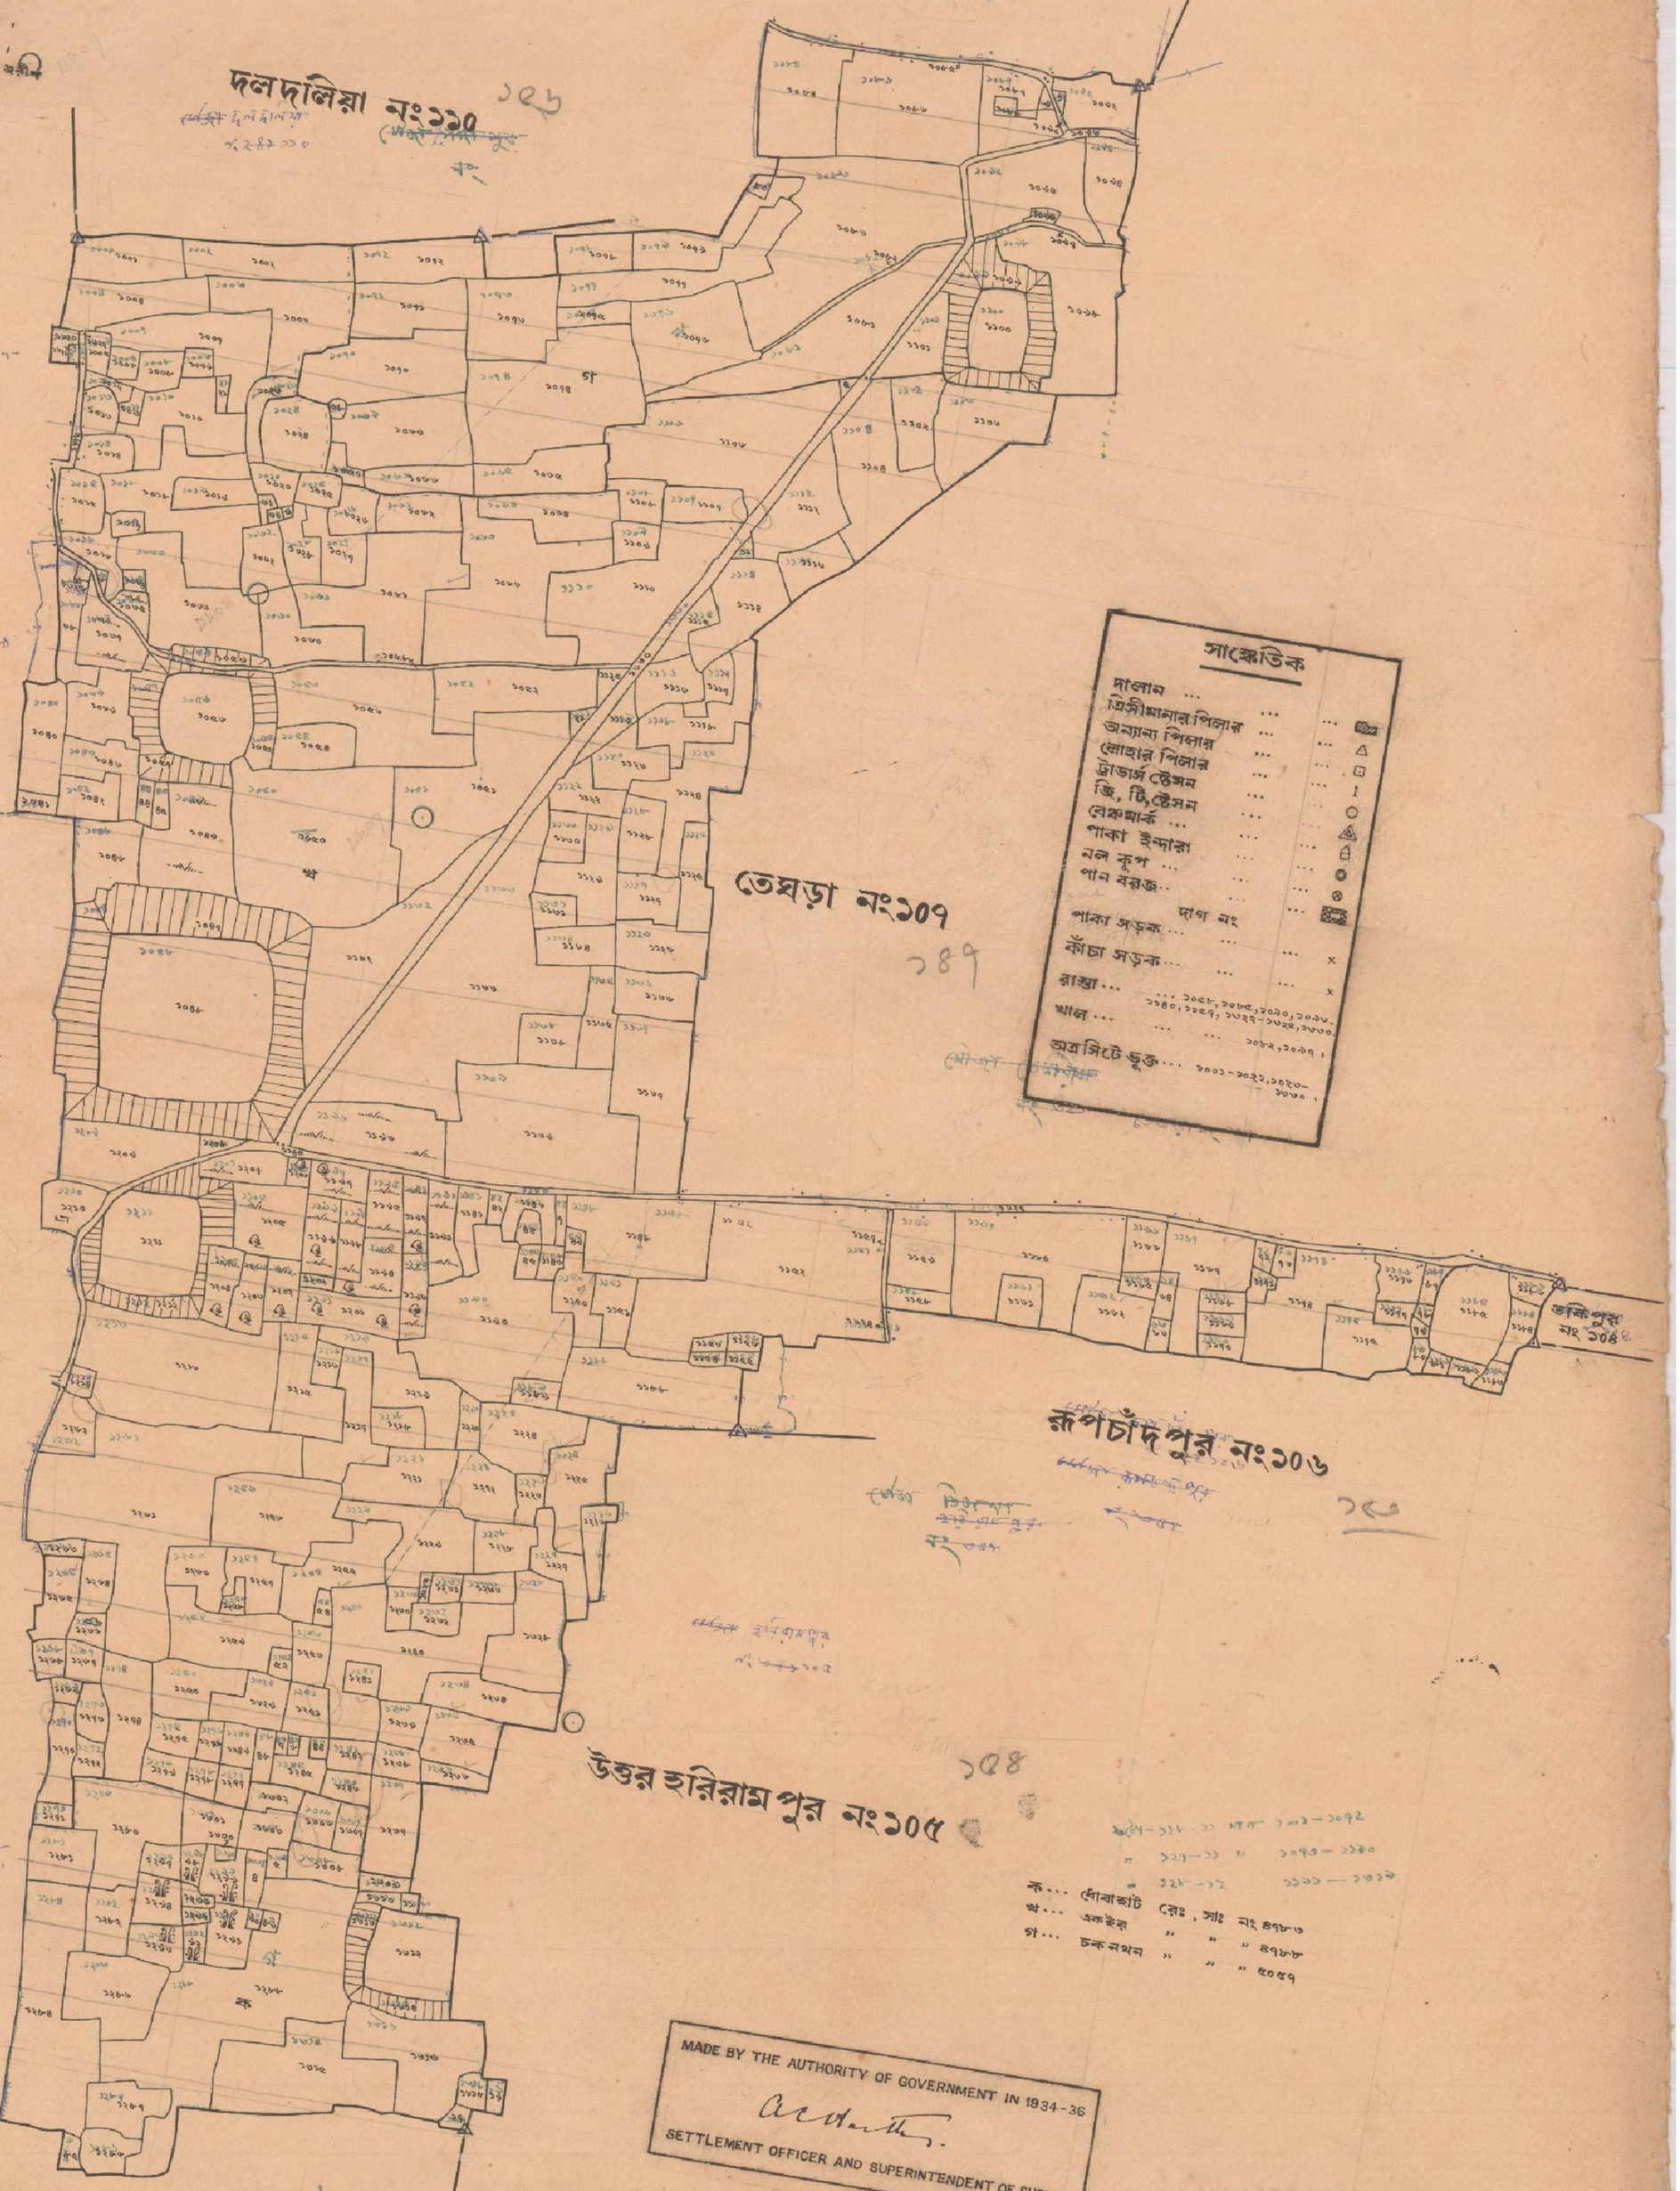

ক... মৌবাহাট রেঃ, সাঃ নং ৪৭৮৩
খ... একইর " " " ৪৭৮৮
গ... চকনথন " " " ৫০৫৭

MADE BY THE AUTHORITY OF GOVERNMENT IN 1934-36

SETTLEMENT OFFICER AND SUPERINTENDENT OF SURVEY

NAME OF MOUZA	OLD J.L.NO	NEW J.L.NO	P.S.	DIST.
একইর	১০৮	১৫৫	ঐ	
দলদলিয়া	১১০	১৫৬		
মঙ্গলপুর	১০৯	১৫৭		
ধনসা	১৮৪	১৭৯		
উত্তরহরিরামপুর	১০৫	১৫৪		
রূপচাঁদপুর	১০৬	১৫৩		
তেঘড়া	১০৭	১৪৭		
কামালপুর	১৪	১৪৬		

ADOPTED FOR THE PURPOSE OF OPERATION UNDER CHAPTER IV OF THE E.B.S.A.& T.ACT, 1950, WITHOUT CORRECTION.

SETTLEMENT OFFICER & SUPERINTENDENT OF SURVEY.