NAME OF				SURVEY		KHANAPURI		BUJHARAT	
KANUNGO	PATWAR AMIN	KHANAPURI AMIN	BUJHARAT KANUNGO	COMMENCED	ENDED	COMMENCED	ENDED	COMMENCED	ENDED
J.C. Bhattacharjee		Jatindra K Majumdar	J.C. Bhattacharjee			30.6.35	3.2.35	15.6.35	15.6.35

জিলা দিনাজপুর

থানা নবাবগঞ্জ

মৌজা বলরামপুর (BALARĀMPUR)

জে, এল, নং ১১৯/১০৩

রে, সা, নং ৪৫১৩, ৪৬৩৪

স্কেল ১৬" = ১ মাইল

১০০ কড়িতে এক জরীপ।
৮০ জরীপে এক মাইল।

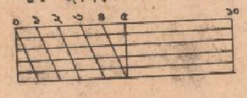

চড়াইভিটা নং ৮২/৬২

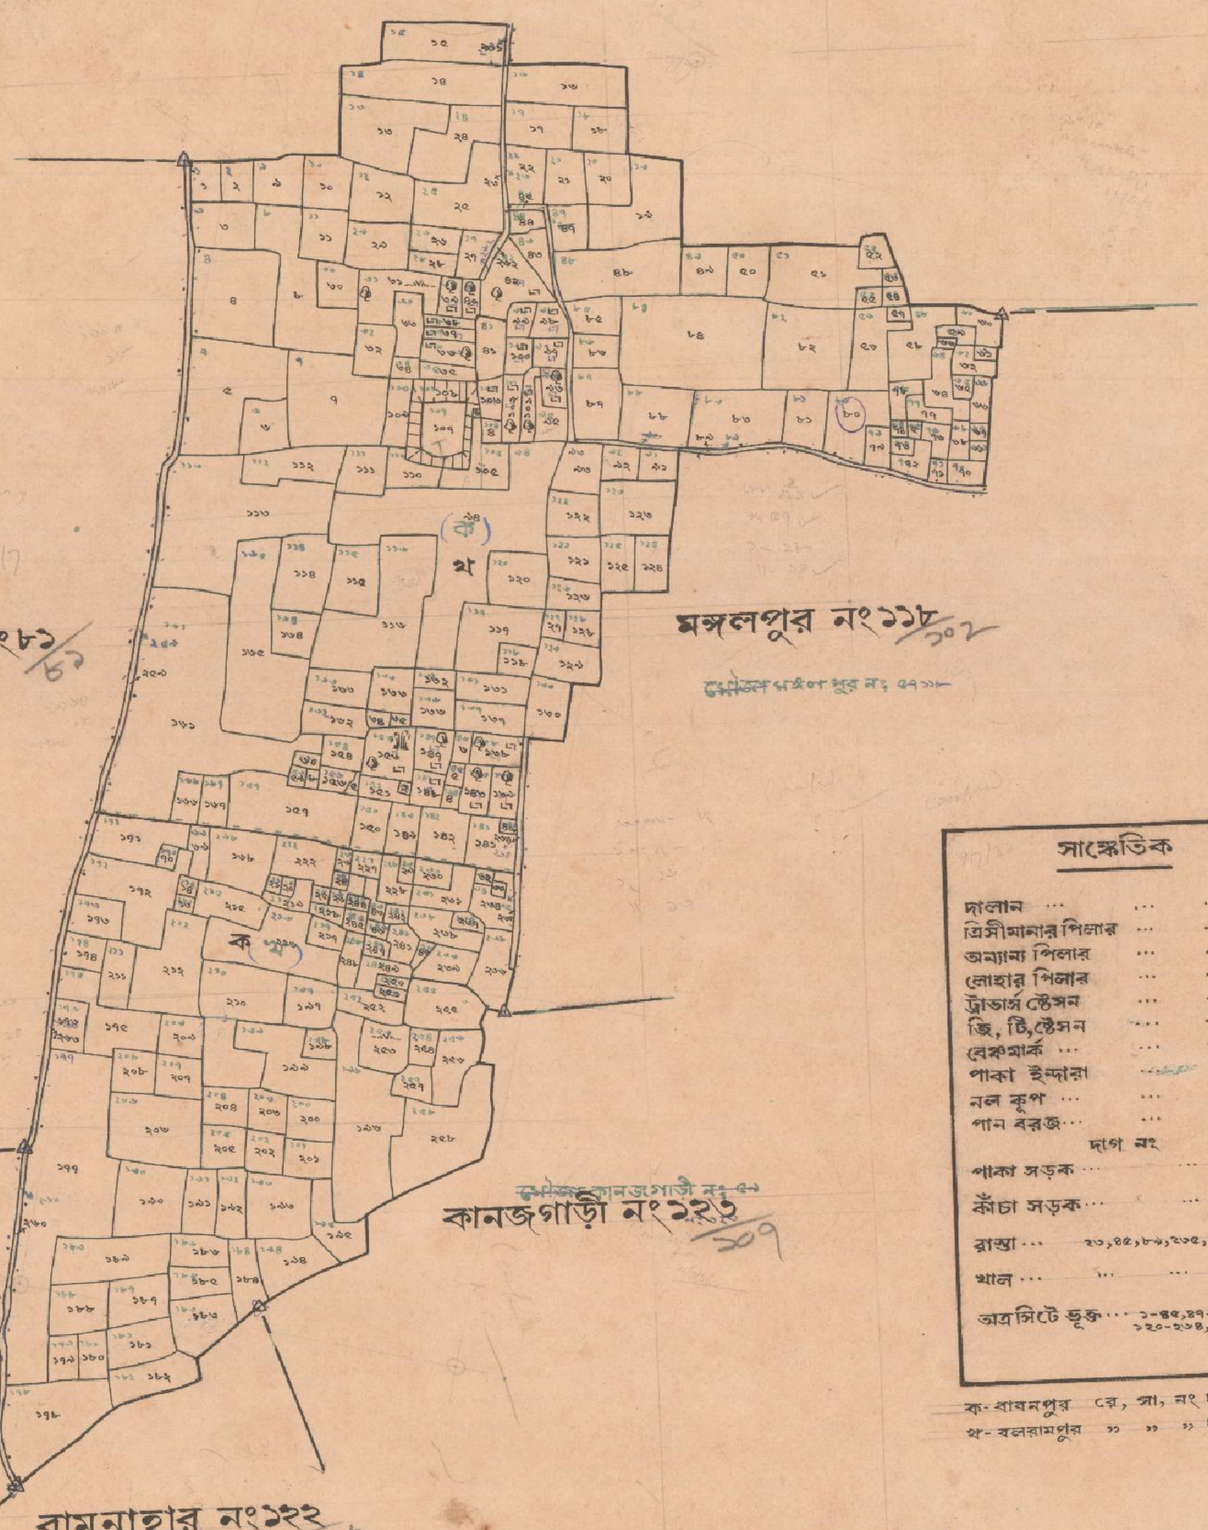

(ক) বলরামপুর রেঃ সাঃ ৪৬৩৪
দাগ ১- ১৬৭, ২৫১, ২৩১, ২৬২, ২৫৪
(খ) বাবন পুরা রেঃ সাঃ ৪৫১৩
দাগ ১৬৮- ২৫৮, ২৩০ ১৬৭

সাঙ্কেতিক

দালান ...	...
ত্রিসীমানার পিলার ...	...
অন্যান্য পিলার ...	...
লোহার পিলার ...	...
ট্রাভার্স ষ্টেসন ...	...
জি, টি, ষ্টেসন ...	...
বেঞ্চমার্ক ...	...
পাকা ইন্দারা ...	...
নল কূপ ...	...
পান বরজ ...	...
দাগ নং	
পাকা সড়ক ...	...
কাঁচা সড়ক ...	...
রাস্তা ...	২৩, ৪৫, ৮৯, ২০৫, ২৫২-২৩৪,
খাল ...	...
অত্রসিটে ভূক্ত ...	১-৪৫, ৪৭-৮৯, ৯১-১১৮, ১২০-২৩৪,

ক- বাবনপুর রে, সা, নং ৪৫১৩
খ- বলরামপুর " " " ৪৬৩৪

দাগআঃ	দাগশেষ
১	২৫৮
ছুটদাগ	বাটাদাগ
১৬১, ১৭৭, ১৮, ২৪, ১৯৯, ১৯১, ২৫৯, ২৩০, ২৩১, ২৩২, ২৩৩, ২৩৪	

অত্রসিটে ভূক্ত ১-৪৫, ৪৭-৮৯, ৯১-১১৮, ১২০-২৩৪.

MADE BY THE AUTHORITY OF GOVERNMENT IN 1934-36

SETTLEMENT OFFICER AND SUPERINTENDENT OF SURVEY

NAME OF MOUZA	OLD J.L.NO	NEW J.L.NO	PS.	DIST.
বলরামপুর	১১৯	১০৩		
চরকাই	৮১	৮১		
জোলাগাড়ী	১২০	১০৪		
বামনাহার	১২২	১০৬		
কানজগাড়ী	১২৬	১০৭		
মঙ্গলপুর	১১৮	১০২		
চড়াইভিটা	৮২	৮২		

ADOPTED FOR THE PURPOSE OF OPERATION UNDER CHAPTER IV OF THE B.B.S.A.& T.ACT, 1950, WITHOUT CORRECTION.

SETTLEMENT OFFICER & SUPERINTENDENT OF SURVEY.