জিলা দিনাজপুর

থানা বোচাগঞ্জ

মৌজা কড়ই (KARAI)

জে, এল, নং ১৫

রে, সা, নং ২২১

স্কেল ১৬" = ১ মাইল

১৫০ কড়িতে এক জরীপ।
৮০ জরীপে এক মাইল।

০ ১ ২ ৩ ৪ ৫ ১০ জরীপ

Name of				Survey		Khanapuri		Dakhal
Tauzia	Nalwar Amin	Khanapuri Amin	Boyharat Kazi	Commenced	Ended	Commenced	Ended	Ca
D. C. Sen	M. Ahammad	M. Ahammad	Abdul Haq Sarkar	2-11-35	6-11-35	7-12-35	20-2-35	

জিলা দিনাজপুর
থানা বোচাগঞ্জ
মৌজা কড়ই
জে.এল. নং ~~২২৬~~ ১৫
রে, সা, নং ২২১
~~সার্কেল নং ২~~
স্কেল ১৬"=১ মাইল।

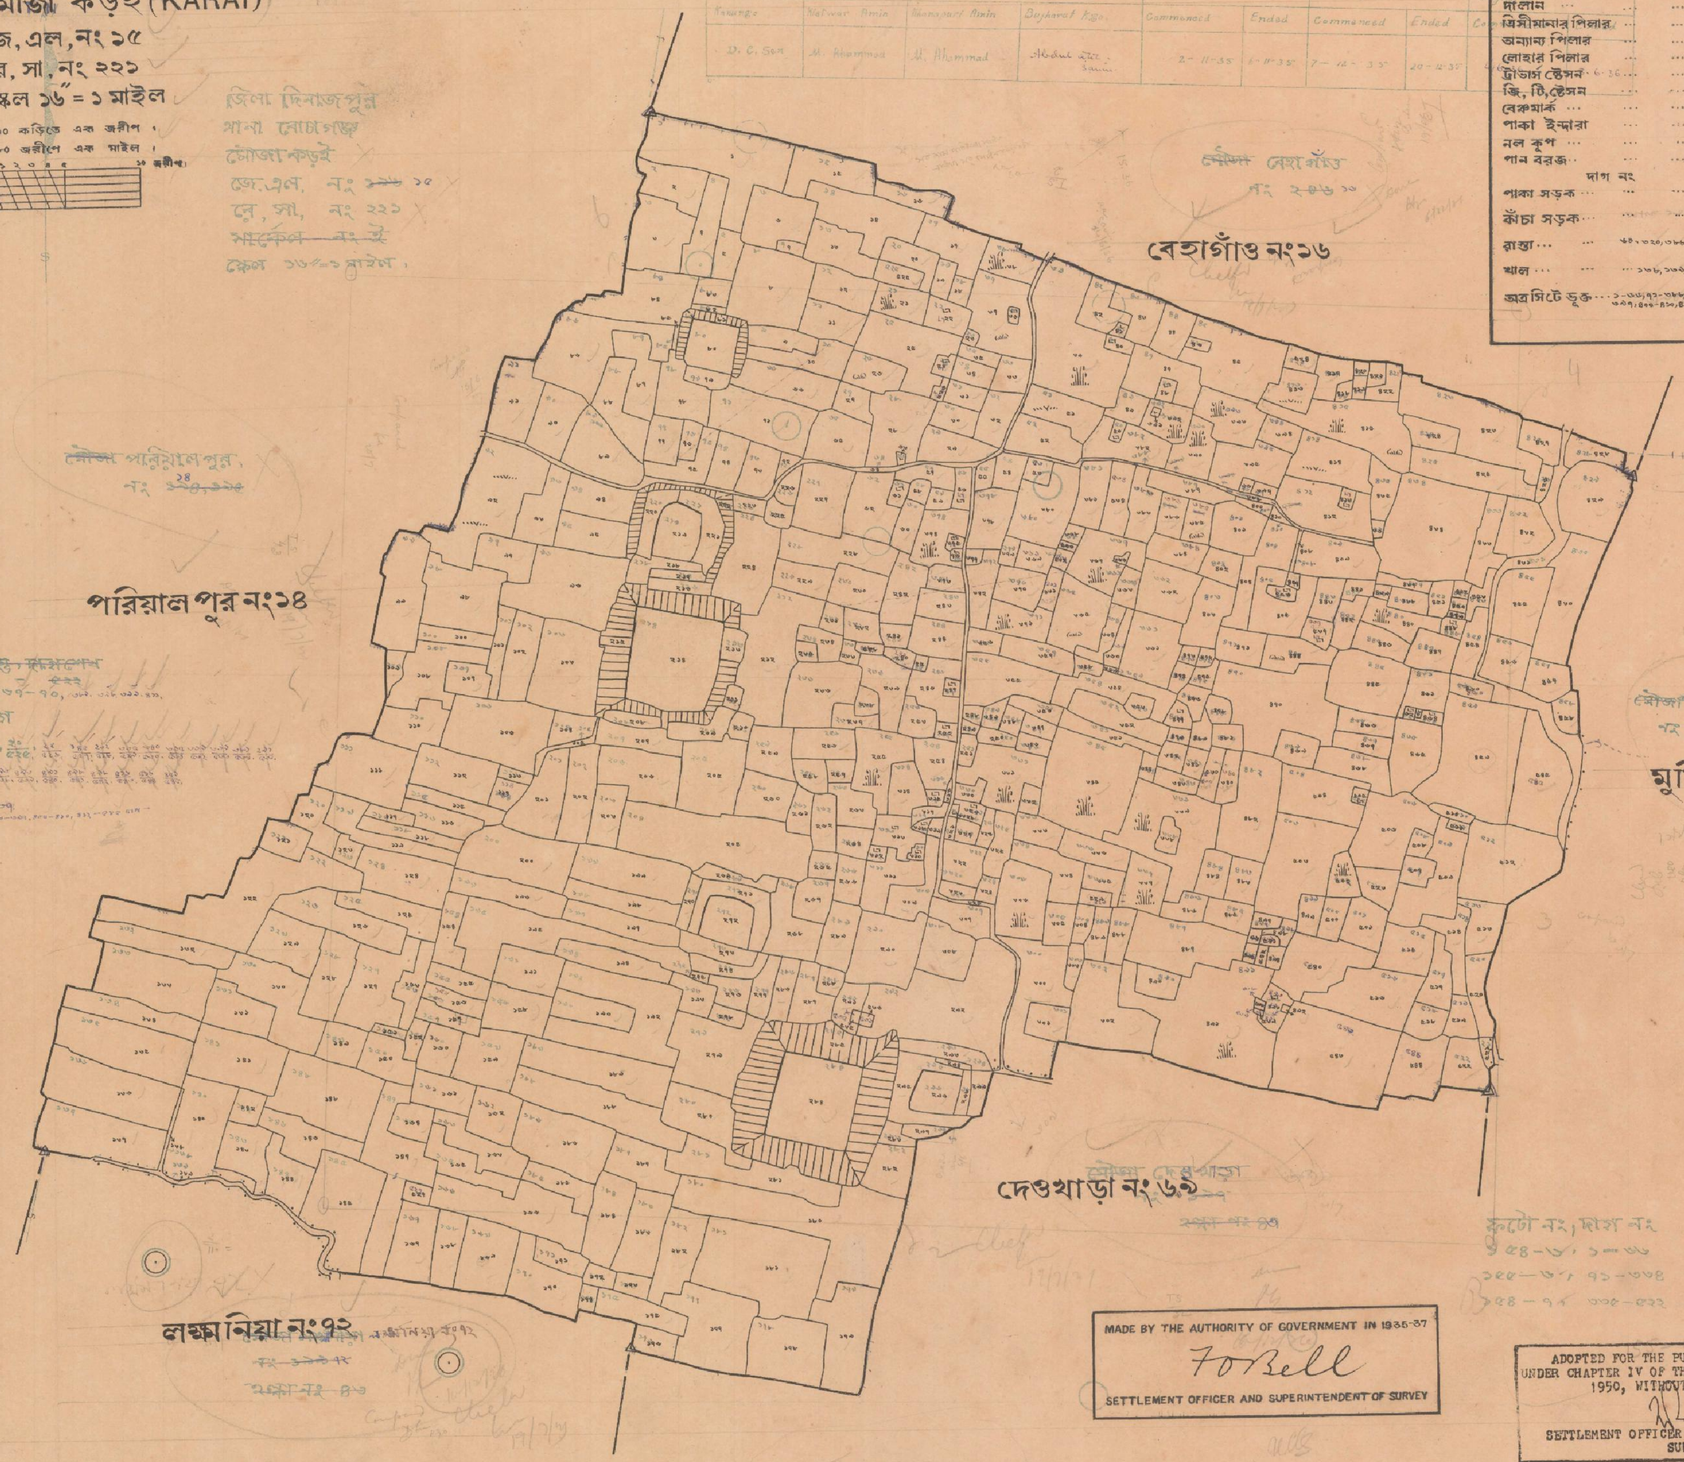

সাঙ্কেতিক

দালান	
বিসীমানার পিলার	△
অন্যান্য পিলার	⊡
লোহার পিলার	I
ট্রাভার্স ষ্টেসন	⊙
জি, টি, ষ্টেসন	⚠
বেঞ্চমার্ক	
পাকা ইন্দারা	
নল কূপ	
পান বরজ	

দাগ নং

পাকা সড়ক	
কাঁচা সড়ক	
রাস্তা	৬৮১, ৩২৩, ৩৮৮, ৪০৮,
খাল	১৩৬, ১৩৬, ৪১১
অব্রসিটে ভুক্ত	১-৩৩, ৪২-৩৮৬, ৩৩৩-৩৫৭, ৪০০-৪১০, ৪১২-৪৪৪

~~মৌজা বেহাগাঁও~~
~~নং ২৩৬ ১৬~~

~~মৌজা পারিয়াল পুর,~~
~~নং ২৩৩, ২১৮~~

মৌজা মুশিদহাট
নং ২০৮-৬৮

~~দাগ তালিকা, কিস্তাপন~~
ছুট দাগ ৩৭-৭০, ...
নাটা দাগ
৫০৬, ৫৭, ৫৮, ...

কুটো নং, দাগ নং
৫৪-৬, ১-৩৬
১৫৫-৩৭, ৭১-৩৩৪
৫৪-৭৮ ৩৩৫-৫২২

MADE BY THE AUTHORITY OF GOVERNMENT IN 1935-37
F O Bell
SETTLEMENT OFFICER AND SUPERINTENDENT OF SURVEY

ADOPTED FOR THE PURPOSE OF OPERATION UNDER CHAPTER IV OF THE E.B.S.A.& T.ACT, 1950, WITHOUT CORRECTION.
SETTLEMENT OFFICER & SUPERINTENDENT OF SURVEY.