জিলা দিনাজপুর

থানা বোচাগঞ্জ

মৌজা ফুট্‌কীবাড়ী সিট নং ১ (PHUTKIBÀRI)

জে, এল, নং ১

রে, সা, নং ৩৬৮

স্কেল ১৬" = ১ মাইল

১০০ কড়িতে এক জরীপ ।

৮০ জরীপে এক মাইল ।

Name of						Survey		Khanapuri	
Kanungo	Kistwar	Amin	Khanapuri Amin	Bujharat Bgo		Commenced	Ended	Commenced	Ended
D. C. Sen	Girindra N. Chakrabortty		Girindra N. Chakrabortty	R. N. Chakrabortty. SI.		18-12-35	20-12-35	21-12-35	27-[illegible]

সাঙ্কেতিক

দালান		
সিমানার পিলার		
অন্যান্য পিলার		
লোহার পিলার		
ট্রাভার্স ষ্টেসন	28.5.36	
জি, টি, ষ্টেসন		
বেঞ্চমার্ক		
পাকা ইন্দারা		
নল কূপ		
পান বরজ		
দাগ নং		
পাকা সড়ক		x
কাঁচা সড়ক		১৯০
রাস্তা		২০৭
খাল		২
অত্র সিটে ভুক্ত	১-৫০, ৫২-৭০, ৭২-২২২, ২২৪-২৩২, ২৩৪-২৪৭.	

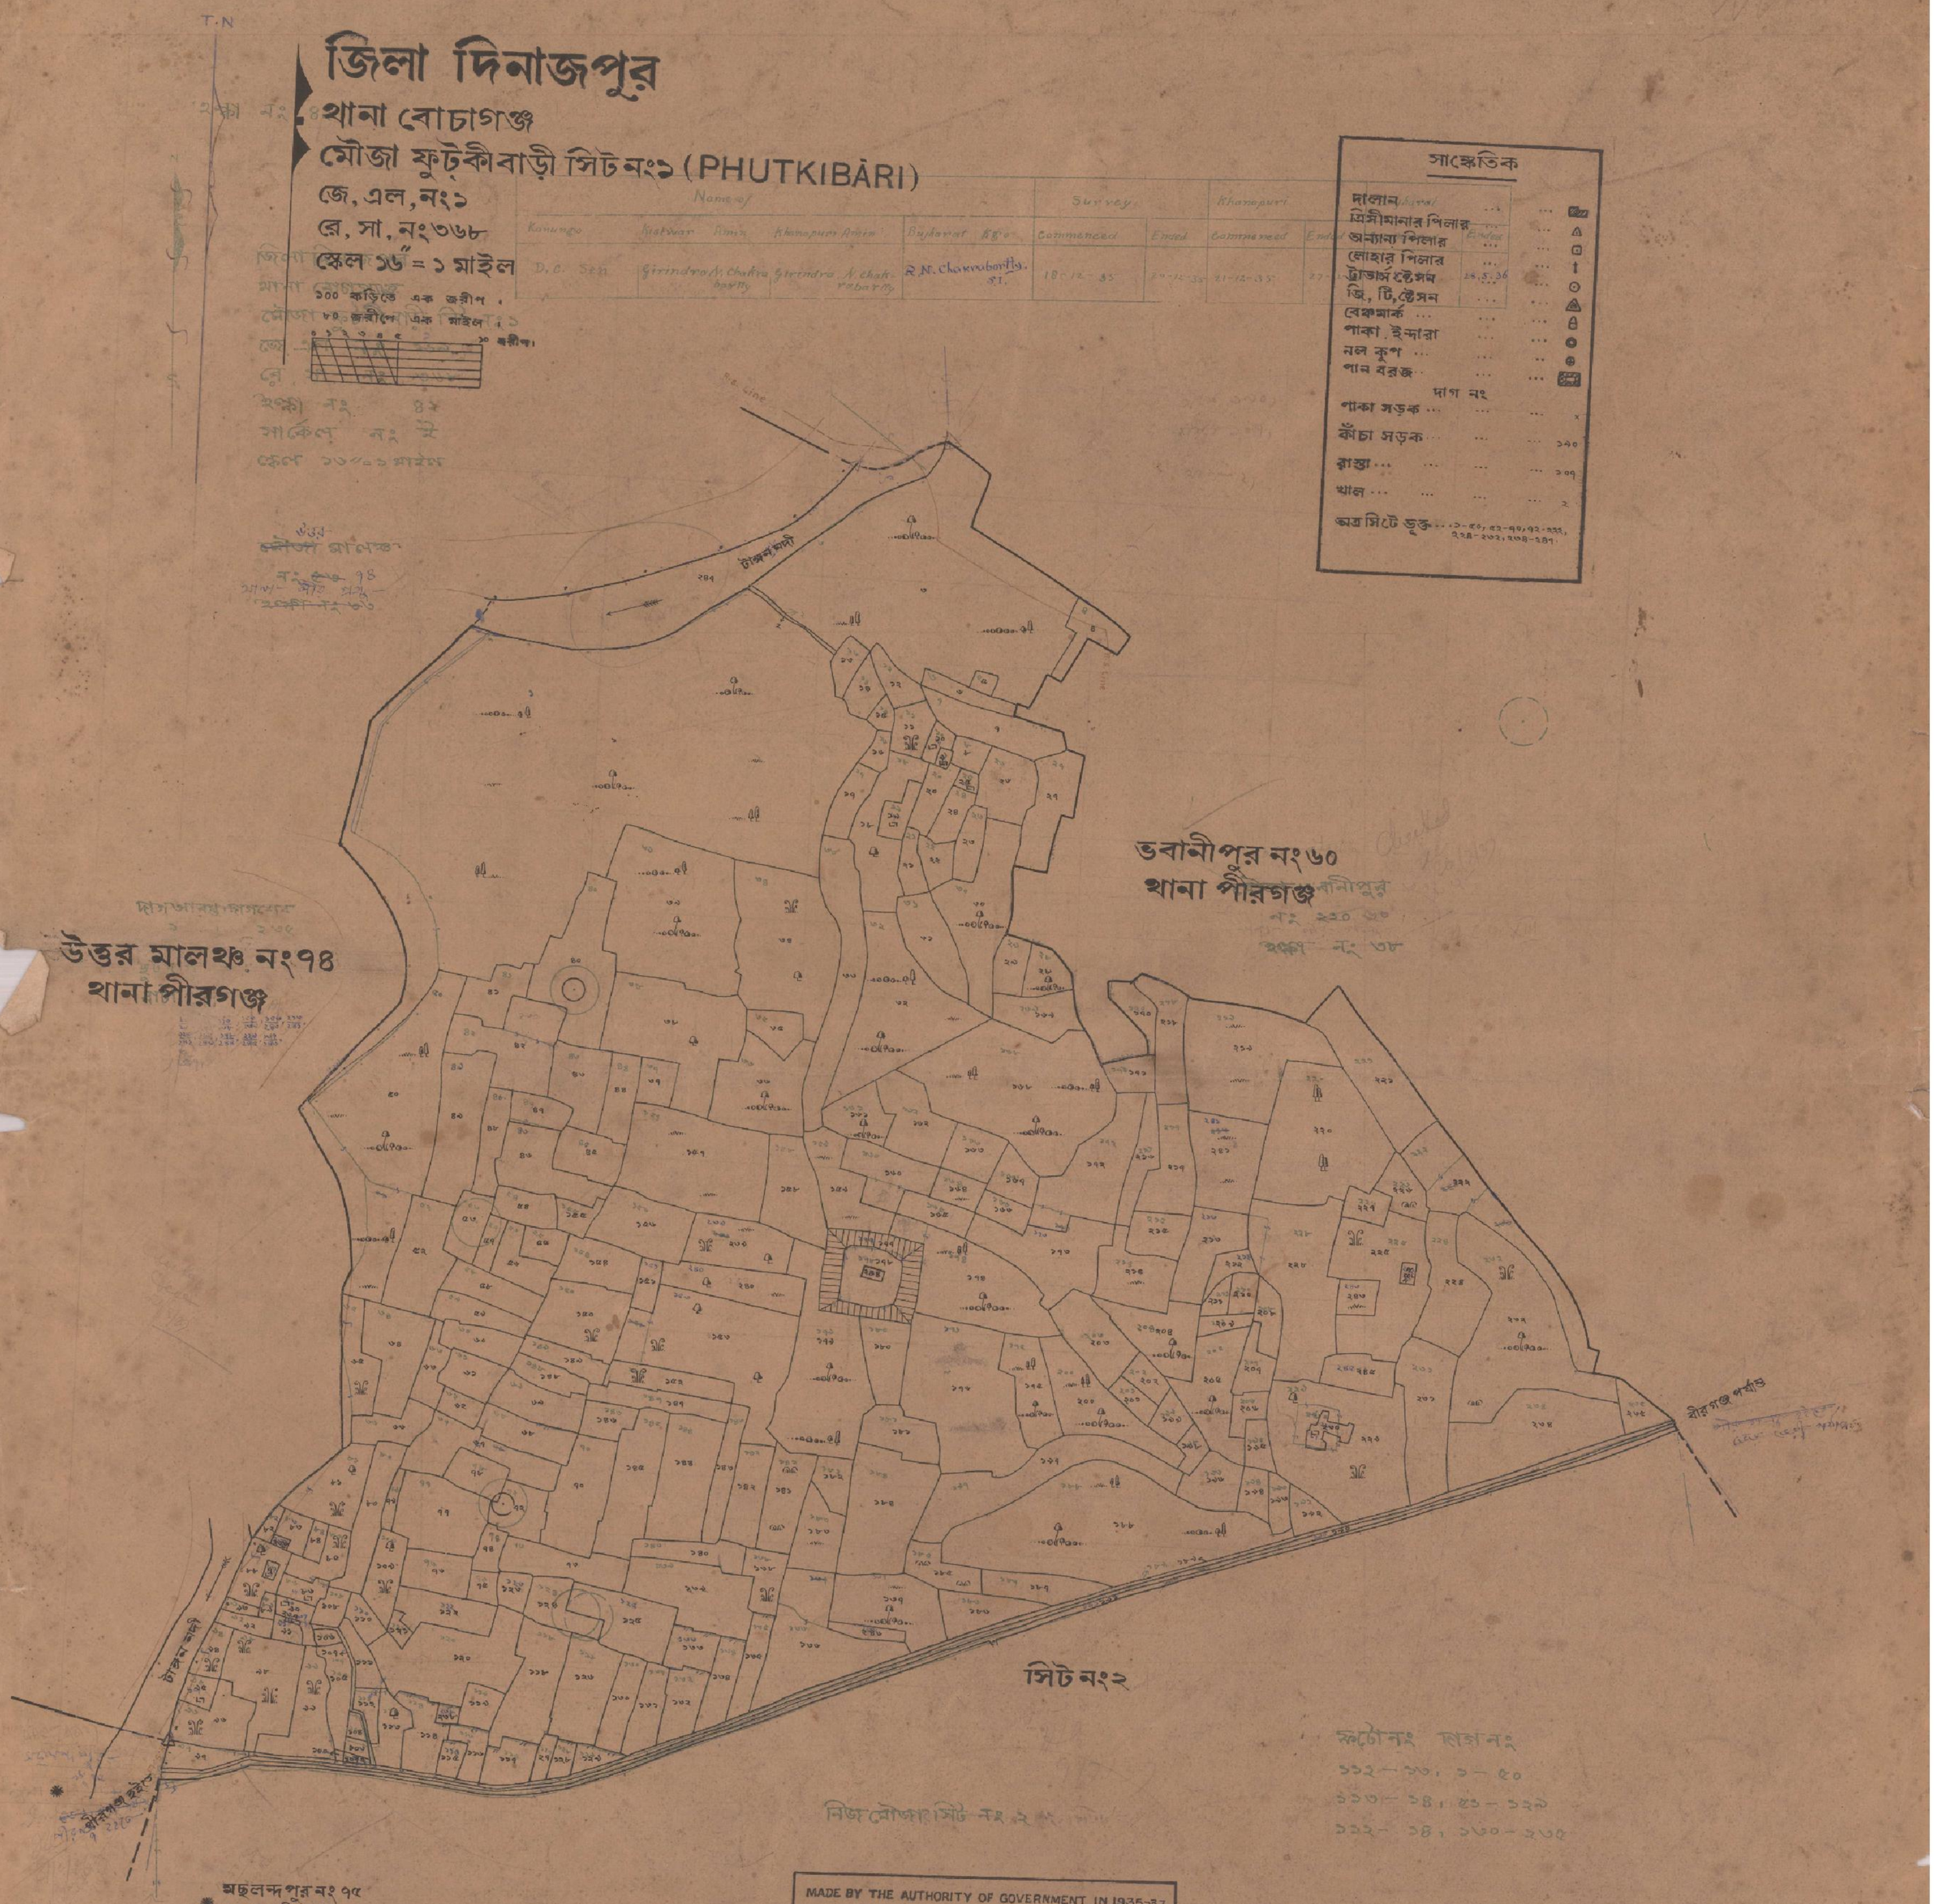

MADE BY THE AUTHORITY OF GOVERNMENT IN 1935-37

F. O. Bell

SETTLEMENT OFFICER AND SUPERINTENDENT OF SURVEY

ADOPTED FOR THE PURPOSE OF OPERATION UNDER CHAPTER IV OF THE E.B.S.A.& T.ACT, 1950, WITHOUT CORRECTION.

SETTLEMENT OFFICER & SUPERINTENDENT OF SURVEY.