Name of			Khanapuri		Bujharat	
Kanungo	Khanapuri Amin	Bujharat Kanungo	Commenced	Ended	Commenced	Ended
S. Hossain	Abdul Gani	S. Hossain	22.1.35	23.2.35	9.5.35	12.5.35

মৌজা নন্দী গ্রাম
জে এল নং ১১৫
রে: সা: নং ৫০৪৯
থানা ফুল বাড়ী
জিলা দিনাজপুর
স্কেল ১৬ ইঞ্চি = ১ মাইল

জিলা দিনাজপুর

থানা ফুলবাড়ী
মৌজা নন্দীগ্রাম (NANDIGRAM)
জে, এল, নং ১১৫
রে, সা, নং ৫০৪৯
স্কেল ১৬" = ১ মাইল

১০০ কড়িতে এক জরীপ।
৮০ জরীপে এক মাইল।
০ ১ ২ ৩ ৪ ৫ ১০ জরীপ

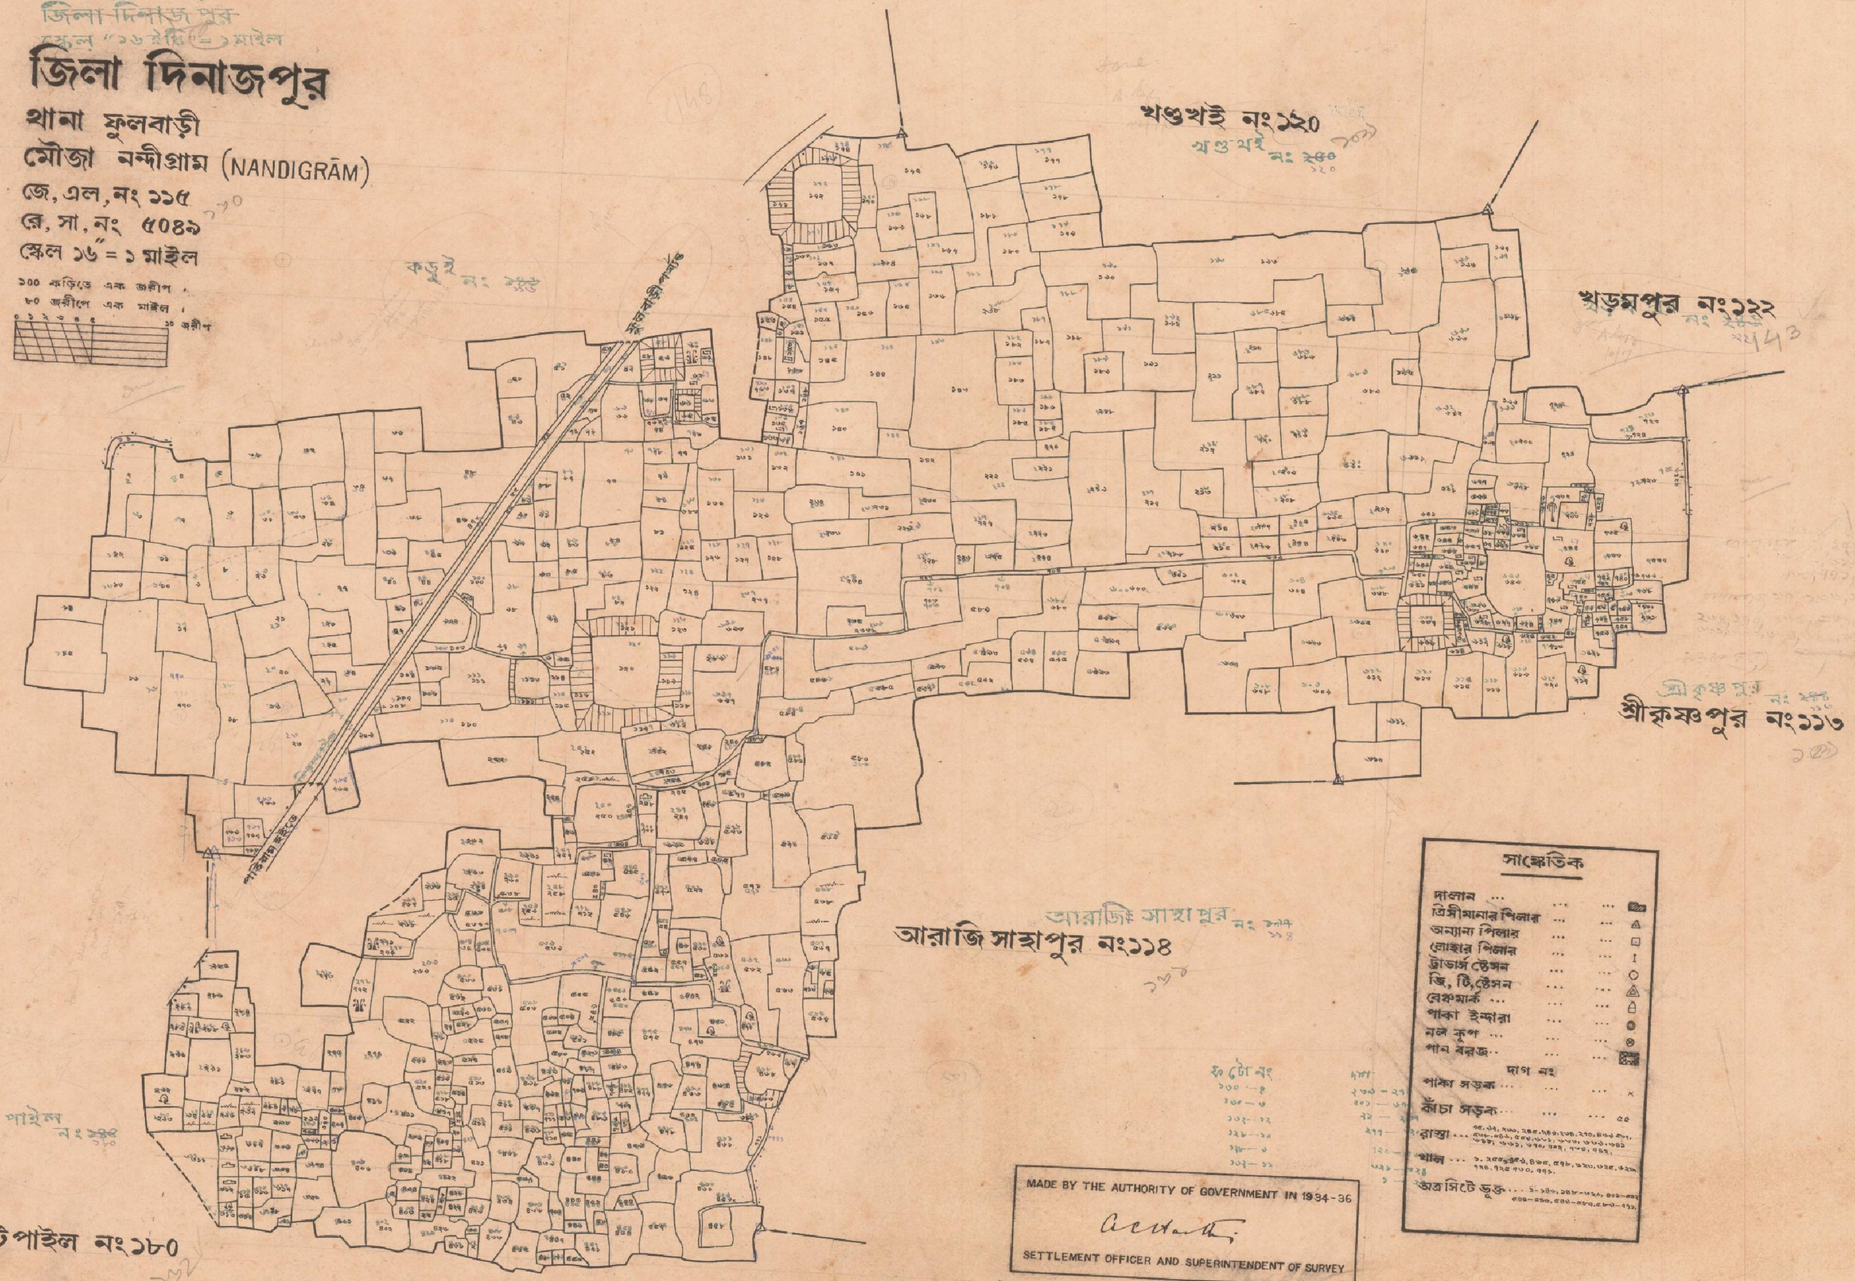

সাঙ্কেতিক

দালান ...
ত্রিশ্রেণীমানের পিলার
অন্যান্য পিলার
লোহার পিলার
ট্রাভার্স ষ্টেসন
জি, টি, ষ্টেসন
বেঞ্চমার্ক ...
পাকা ইন্দারা
নল কূপ ...
পান বরজ ...

দাগ নং

পাকা সড়ক ...
কাঁচা সড়ক ...
রাস্তা ...
খাল ...
অত্র সিটে ভুক্ত ...

MADE BY THE AUTHORITY OF GOVERNMENT IN 1934-36

SETTLEMENT OFFICER AND SUPERINTENDENT OF SURVEY

NAME OF MOUZA	OLD J.L.NO	NEW J.L.NO	P.S.	DIST.
নন্দিগ্রাম	১১৫	১১০		
কড়ুই	১১৬	১৭২		
ভাটপাইল	১৮০	১৩২		
আরাজিসাহাপুর	১১৪	১৩১		
শ্রীকৃষ্ণপুর	১১৩	১৫৯		
খড়মপুর	১২২	১৪৬		
খণ্ডখই	১২০	১০৯		

ADOPTED FOR THE PURPOSE OF OPERATION UNDER CHAPTER IV OF THE E.B.S.A.& T.ACT, 1950, WITHOUT CORRECTION.

SETTLEMENT OFFICER & SUPERINTENDENT OF SURVEY.