জিলা দিনাজপুর

থানা বীরগঞ্জ

মৌজা মদন সাঁকো সিট নং ২ (MADAN SANKO)

জে, এল, নং ১৪

রে, সা, নং ১৫১, ১৫৩

স্কেল ১৬" = ১ মাইল

১০০ কড়িতে এক জরীপ ।

৮০ জরীপে এক মাইল ।

Mauza	Kanungo	Kistwar Amin	Khanapuri Amin	Bijharat Kanungo	Survey		Bijharat	
Madansanko	S. D. De	M. K. Chanda	M. K. Chunder	Md. M. K. Allisani c.s.g.	Commenced	Ended	Commenced	Ended
					4.12.35	5.12.35	10.4.36	12.4.36

সাঙ্কেতিক

দালান ...	Khanapuri ...	Bijharat
ত্রিসীমানার পিলার ...	...	△
অন্যান্য পিলার ...	...	⊡
লোহার পিলার ...	...	‡
ট্রাভার্স ষ্টেসন ...	...	○
জি, টি, ষ্টেসন ...	...	⊿
বেঞ্চমার্ক ...	...	⊟
পাকা ইন্দারা ...	...	⊙
নল কূপ ...	...	⊕
পান বরজ ...	...	▦

দাগ নং

পাকা সড়ক ...	×
কাঁচা সড়ক ...	×
রাস্তা ...	৬৫০, ৬৭২, ৬৭৩, ৬৭৫, ৭৪২, ৭৯৮, ৮২৪, ৮২৫, ৮৩১, ৮৫৫, ৮৮০, ৮৯০, ৮৯২, ৮৯৮,
খাল ...	৮৬২, ৮৭০, ৮৭৯, ৮৮৩.
অত্র সিটে ভুক্ত ...	৫৩৮–৫৬০, ৫৬৮–৬১৯, ৬২২, ৬৩২, ৬৫৪–৬৯৮, ৭০০–৭১১, ৭২৩–৮৭০, ৮৭২–৮৯৩,

ক ... শিবরামপুর আরাজি রেঃ সাঃ নং ১৫১

খ ... মদন সাঁকো রেঃ সাঃ নং ১৫৩

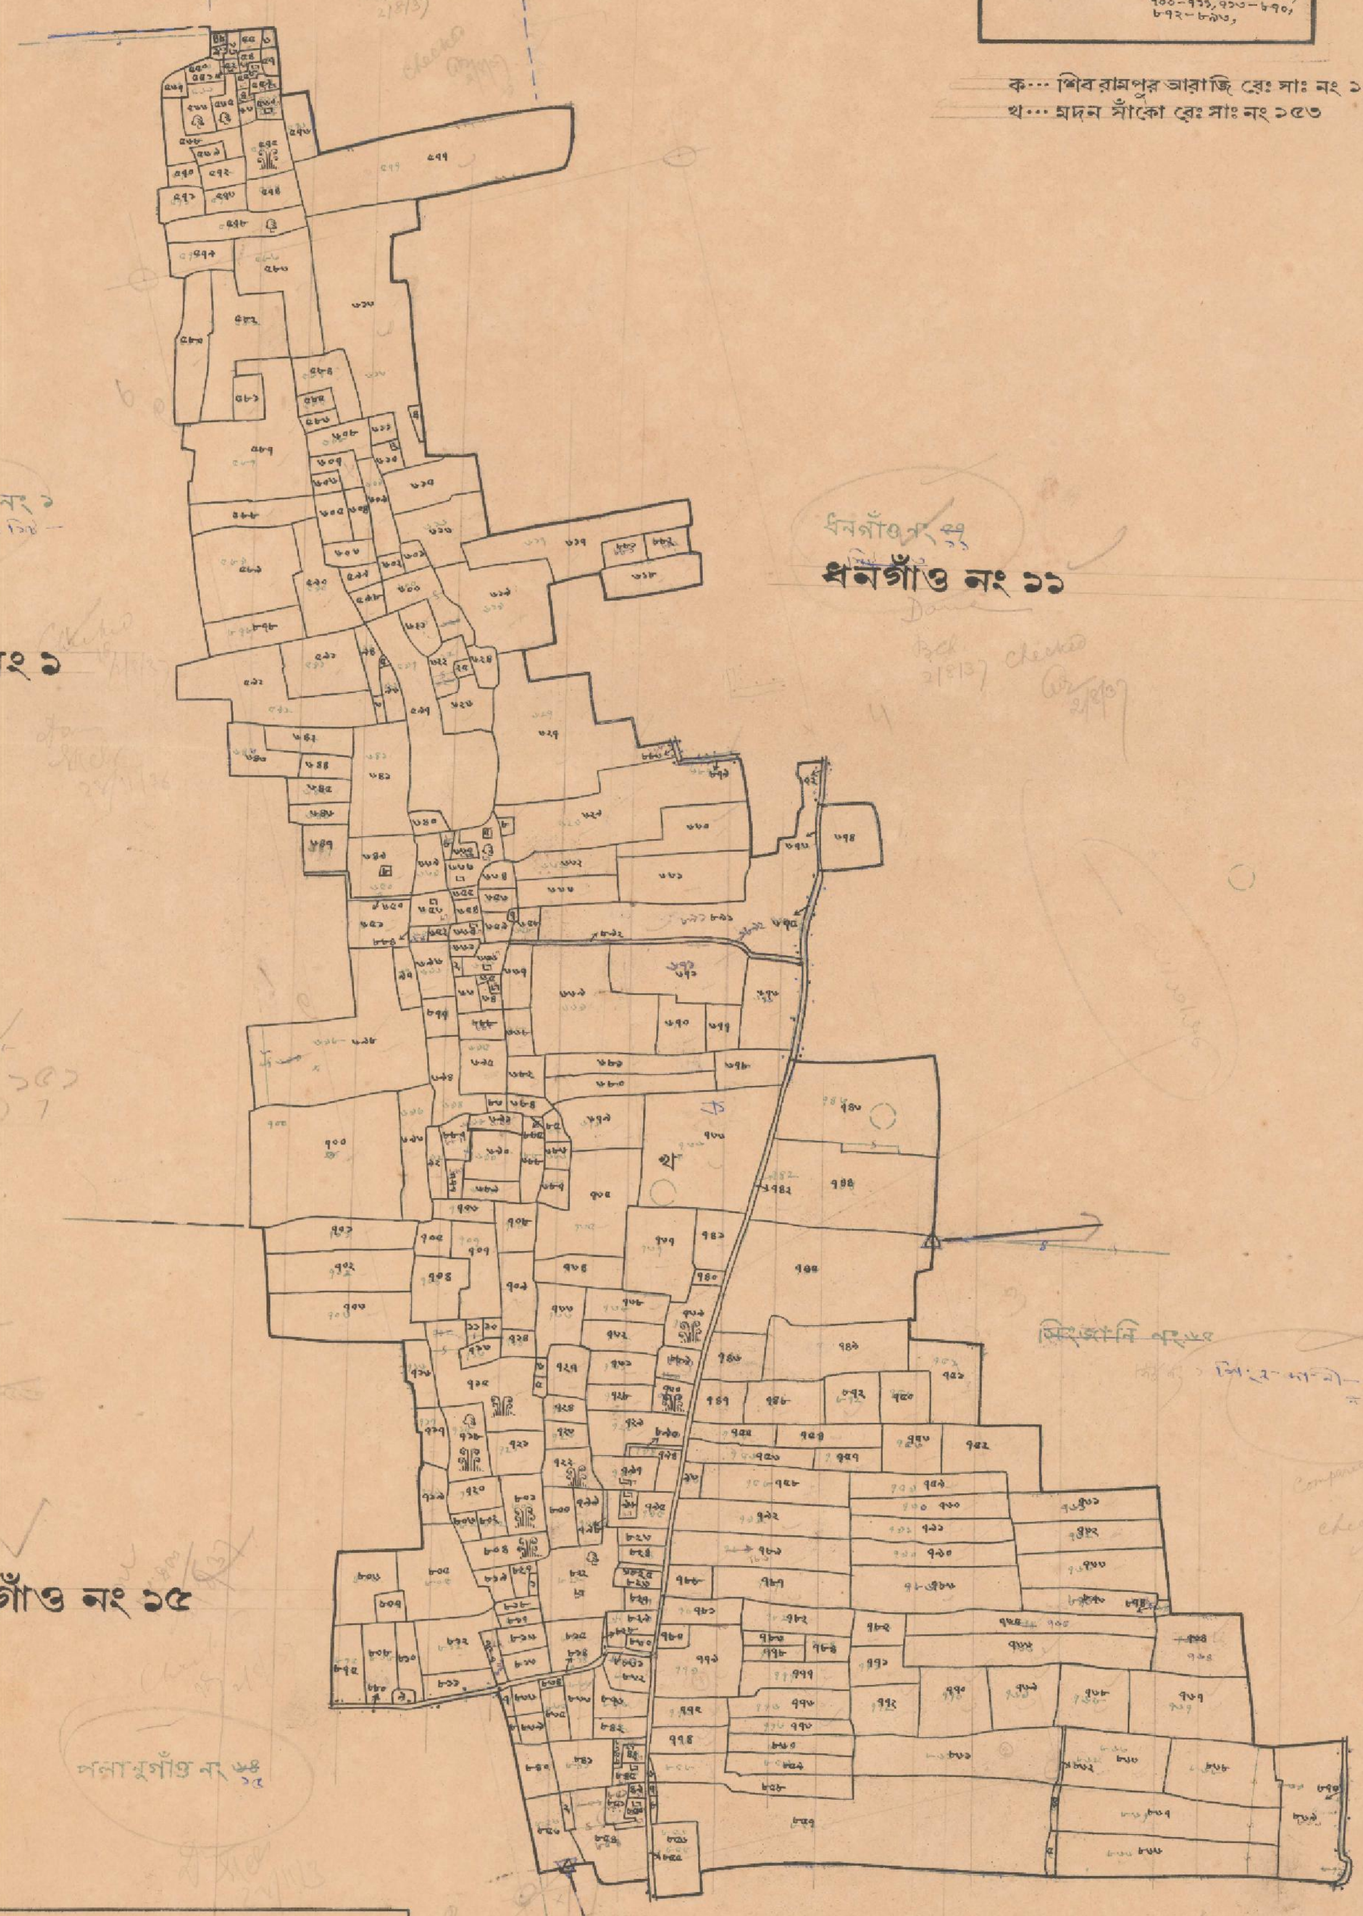

সিট নং ১

ধনগাঁও নং ১১

পালানুগাঁও নং ১৫

সিংহজানী নং ১০

MADE BY THE AUTHORITY OF GOVERNMENT IN 1935-37

F O Bell

SETTLEMENT OFFICER AND SUPERINTENDENT OF SURVEY

ADOPTED FOR THE PURPOSE OF OPERATION UNDER CHAPTER IV OF THE E.B.S.A.& T.ACT, 1950, WITHOUT CORRECTION.

SETTLEMENT OFFICER & SUPERINTENDENT OF SURVEY.