Nom: of				Survey		Khanapuri		Bujharat	
Kanungo	Amin	Khana. Pura Am	Bujharat, Kgo.	Commenced	Ended	Commenced	Ended	Commenced	Ended
Ue. Chakraborty	Anban ali	Anban ali	Lutfalkarim	3.2.35	10.2.35	16.2.35	28.2.35	16.6.35	17.6.35

জিলা দিনাজপুর

থানা নবাবগঞ্জ

মৌজা বড় জালালপুর (BARA JALALPUR) সিট নং২

জে, এল, নং ৭৬

রে, সা, নং ৪৬১৭

স্কেল ১৬" = ১ মাইল

১০০ কড়িতে এক জরীপ ।
৮০ জরীপে এক মাইল ।

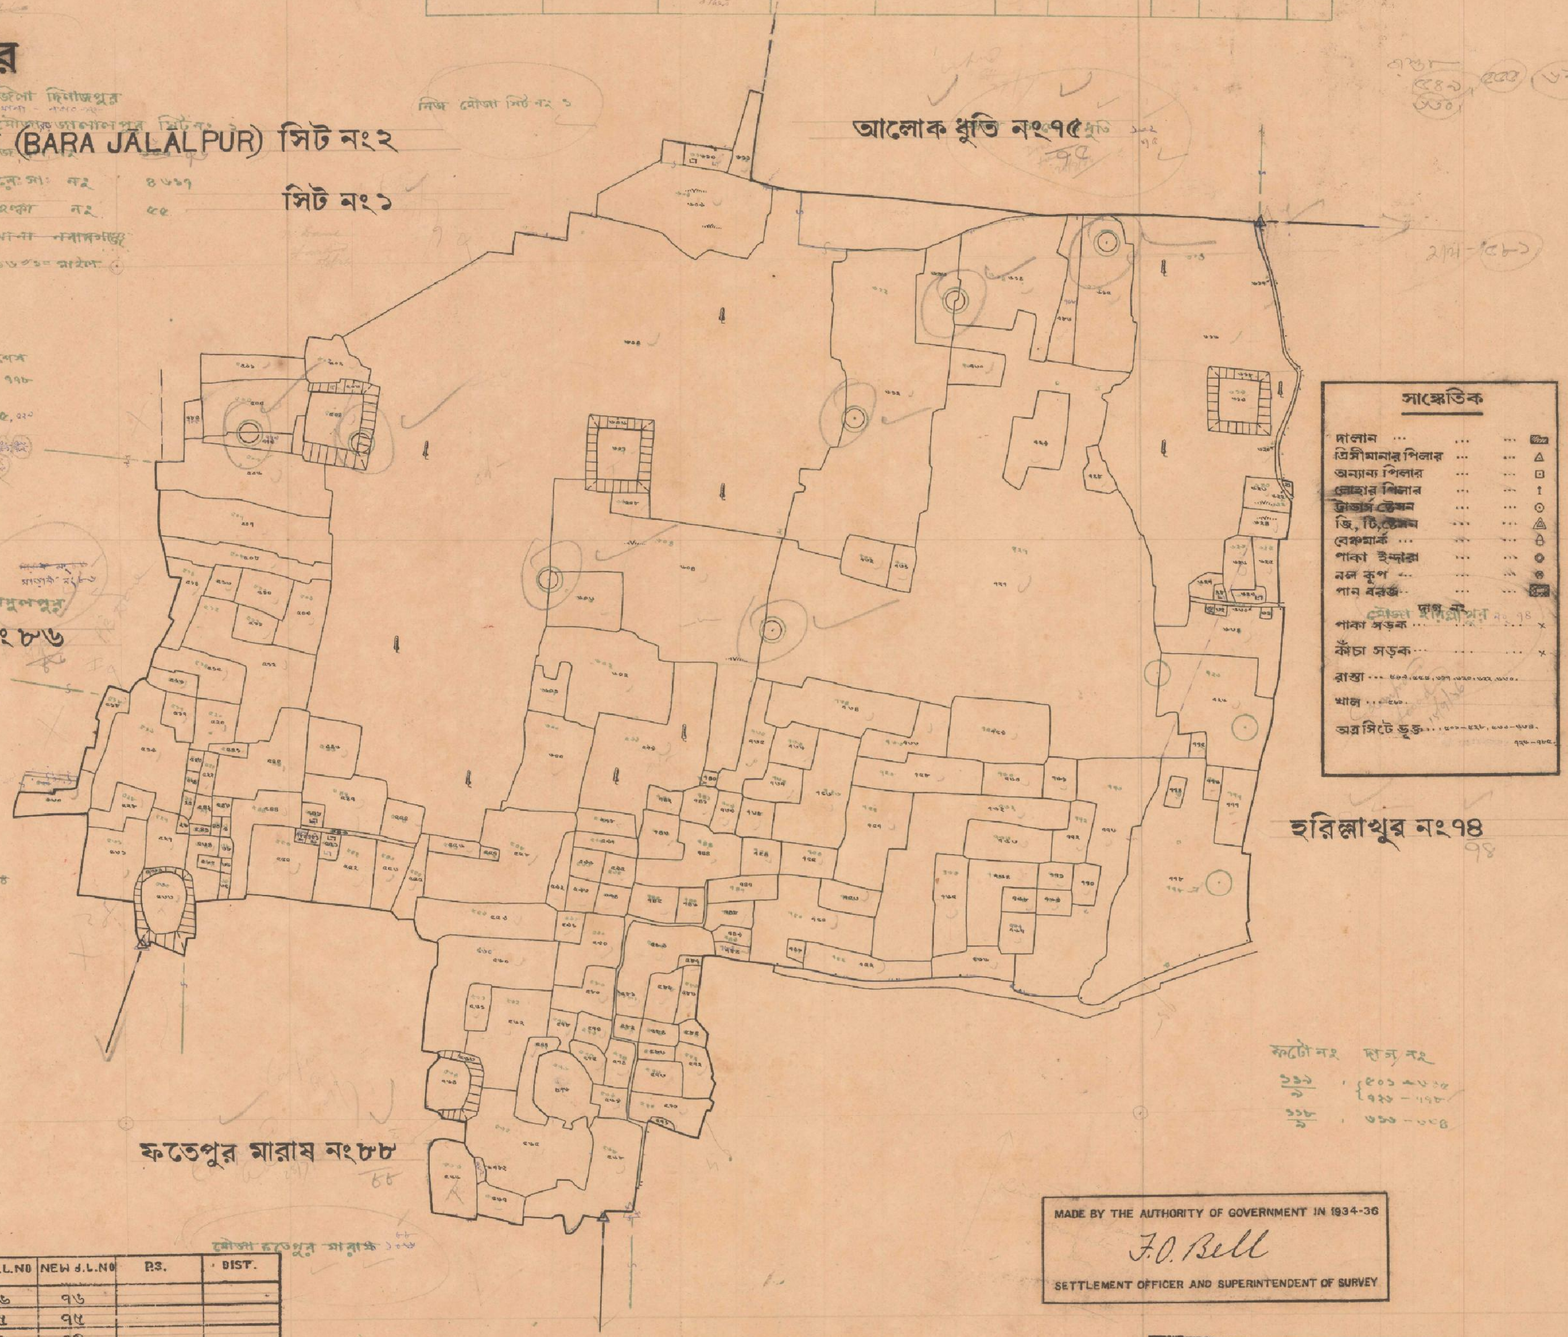

সাঙ্কেতিক

দালান ...	
ত্রিসীমানার পিলার ...	△
অন্যান্য পিলার ...	⊡
লোহার পিলার ...	↑
ট্রাভার্স ষ্টেশন ...	⊙
জি, টি, ষ্টেশন ...	△
বেঞ্চমার্ক ...	
পাকা ইন্দারা ...	
নল কূপ ...	
পান বরজ ...	
দাগ নং	
পাকা সড়ক ...	×
কাঁচা সড়ক ...	×
রাস্তা ...	
খাল ...	
অরগিটে ভূক্ত ...	

NAME OF MOUZA	OLD J.L.NO	NEW J.L.NO	P.S.	DIST.
বড় জালালপুর	৭৬	৭৬		
আলোকধুতি	৭৫	৭৫		
হরিল্লাখুর	৭৪	৭৪		
ফতেপুরমারাষ	৮৮	৮৮		
মাড়াষ	৮৬	৮৬		

MADE BY THE AUTHORITY OF GOVERNMENT IN 1934-36

F.O. Bell

SETTLEMENT OFFICER AND SUPERINTENDENT OF SURVEY

ADOPTED FOR THE PURPOSE OF OPERATION UNDER CHAPTER IV OF THE E.B.S.A.& T.ACT, 1950, WITHOUT CORRECTION.

SETTLEMENT OFFICER & SUPERINTENDENT OF SURVEY.