জিলা দিনাজপুর

থানা বোচাগঞ্জ

মৌজা বড় বালিহারা (BARA BALIHARA)

জে, এল, নং ১১৫

রে, সা, নং ৩৫

স্কেল ১৬" = ১ মাইল

১০০ কাঠিতে এক জরীপ।

৮০ জরীপে এক মাইল।

১ সাঃ = ১০ জরীপ

Name of				Kistwar		Khanapuri		Bujharat	
Kanungo	Kistwar	Khanapuri Amin.	Bujharat K.go.	Commenced	Ended	Commenced	Ended	Commenced	Ended
1	2	3	4	5	6	7	8	9	10
S. K. Chakraborty.		Aswini Kumar Mazumder	N.N. Sen Gupta	4. 12. 35.	14. 12. 35	14. 12. 35.		18. 3. 36	24. 3. 36

সাঙ্কেতিক

দালান	
ত্রিসীমানার পিলার	△
অন্যান্য পিলার	⊡
লোহার পিলার	↑
ট্রাভার্স ষ্টেসন	⊙
জি, টি, ষ্টেসন	⊿
বেঞ্চমার্ক	⍋
পাকা ইন্দারা	◎
নল কূপ	⊕
পান বরজ	
পাকা সড়ক	x
কাঁচা সড়ক	
রাস্তা ... ৮৮, ১৬৮, ২৬৮	
খাল ... ৩৩৯, ৪২৯, ২৫৪.	
অত্রসিটে ভুক্ত ... ১-৪১৭	

দাগ নং

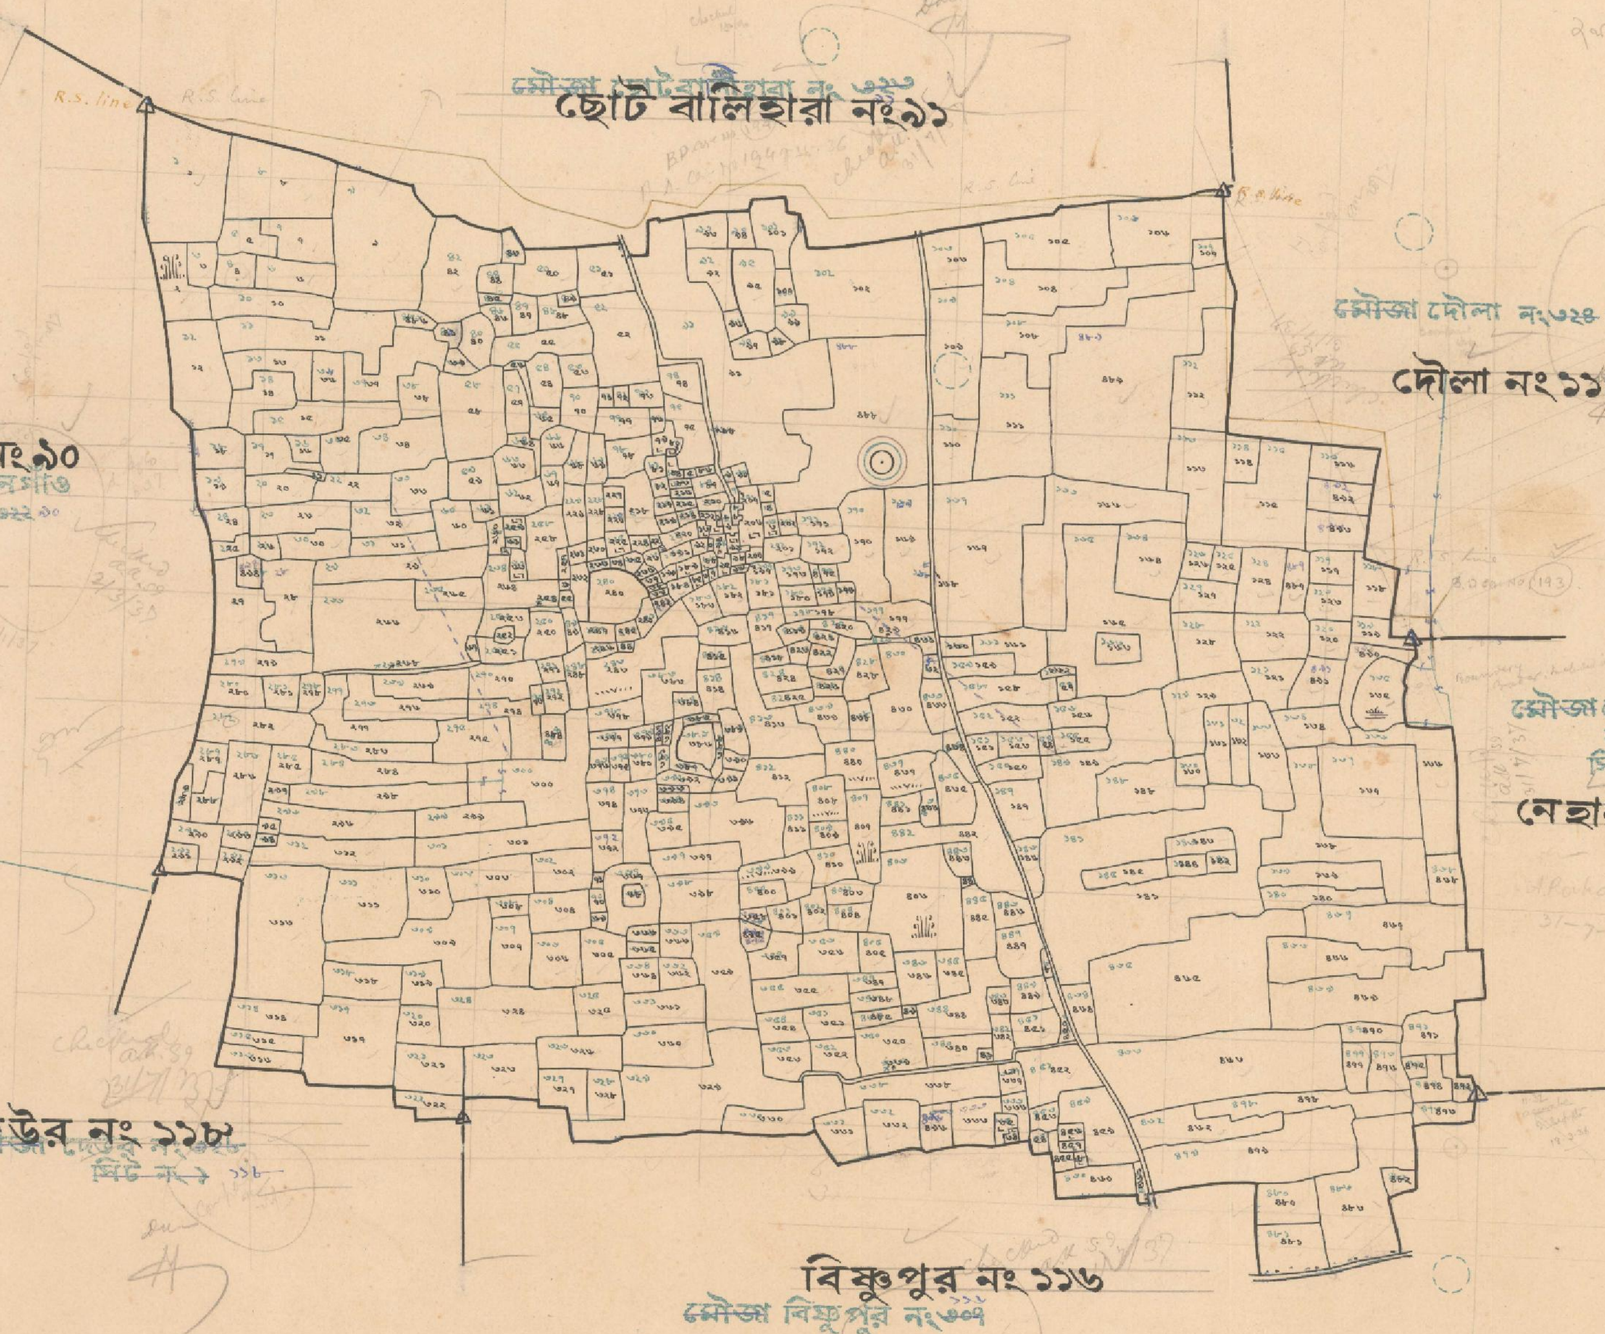

MADE BY THE AUTHORITY OF GOVERNMENT IN 1935-37

F O Bell

SETTLEMENT OFFICER AND SUPERINTENDENT OF SURVEY

ফটোনং — দাগনং
১৫৫—৯ — ১—১০২,
১৫৪—১১—১০৩—১৬৭,
৪৬২—৪৮৬,
১৫৫—১০—১৬৮—৪৬১,

ADOPTED FOR THE PURPOSE OF OPERATION UNDER CHAPTER IV OF THE E.B.S.A.& T.ACT, 1950, WITHOUT CORRECTION.

SETTLEMENT OFFICER & SUPERINTENDENT OF SURVEY.