জিলা দিনাজপুর

থানা নবাবগঞ্জ

মৌজা খিয়ার মির্জ্জাপুর (KHIAR MIRZAPUR)

জে, এল, নং ৩৫

রে, সা, নং ৫৫৮৩

স্কেল ১৬" = ১ মাইল

১০০ কড়িতে এক জরীপ।

৮০ জরীপে এক মাইল।

Kanungo	R. Amin	Sa. Amin	Survey Commenced	Survey Ended	Khanapuri Commenced	Khanapuri Ended	Bujharat Commenced	Bujharat Ended
			12.1.35	31.1.35	12.1.35.	31.1.35	11.4.35	11.9.35

সাঙ্কেতিক

দালান	
ত্রিসীমানার পিলার	▲
অন্যান্য পিলার	⊡
লোহার পিলার	↕
ট্রাভার্স ষ্টেসন	⊙
জি, টি, ষ্টেসন	△
বেঞ্চমার্ক	⌂
পাকা ইন্দারা	⊙
নল কূপ	⊗
পান বরজ	
দাগ নং	
পাকা সড়ক	×
কাঁচা সড়ক	×
রাস্তা ... ৪১৭, ৪৬৯, ৫০০, ৫০২, ৫৪৮, ৫৫০, ৫৭৫, ৬০০.	
খাল ... ৩০৫.	
অত্রগিটে ভুক্ত ... ১-১৯, ২০-২৬, ৩০১-৩৩০, ৪০১-৬১০.	

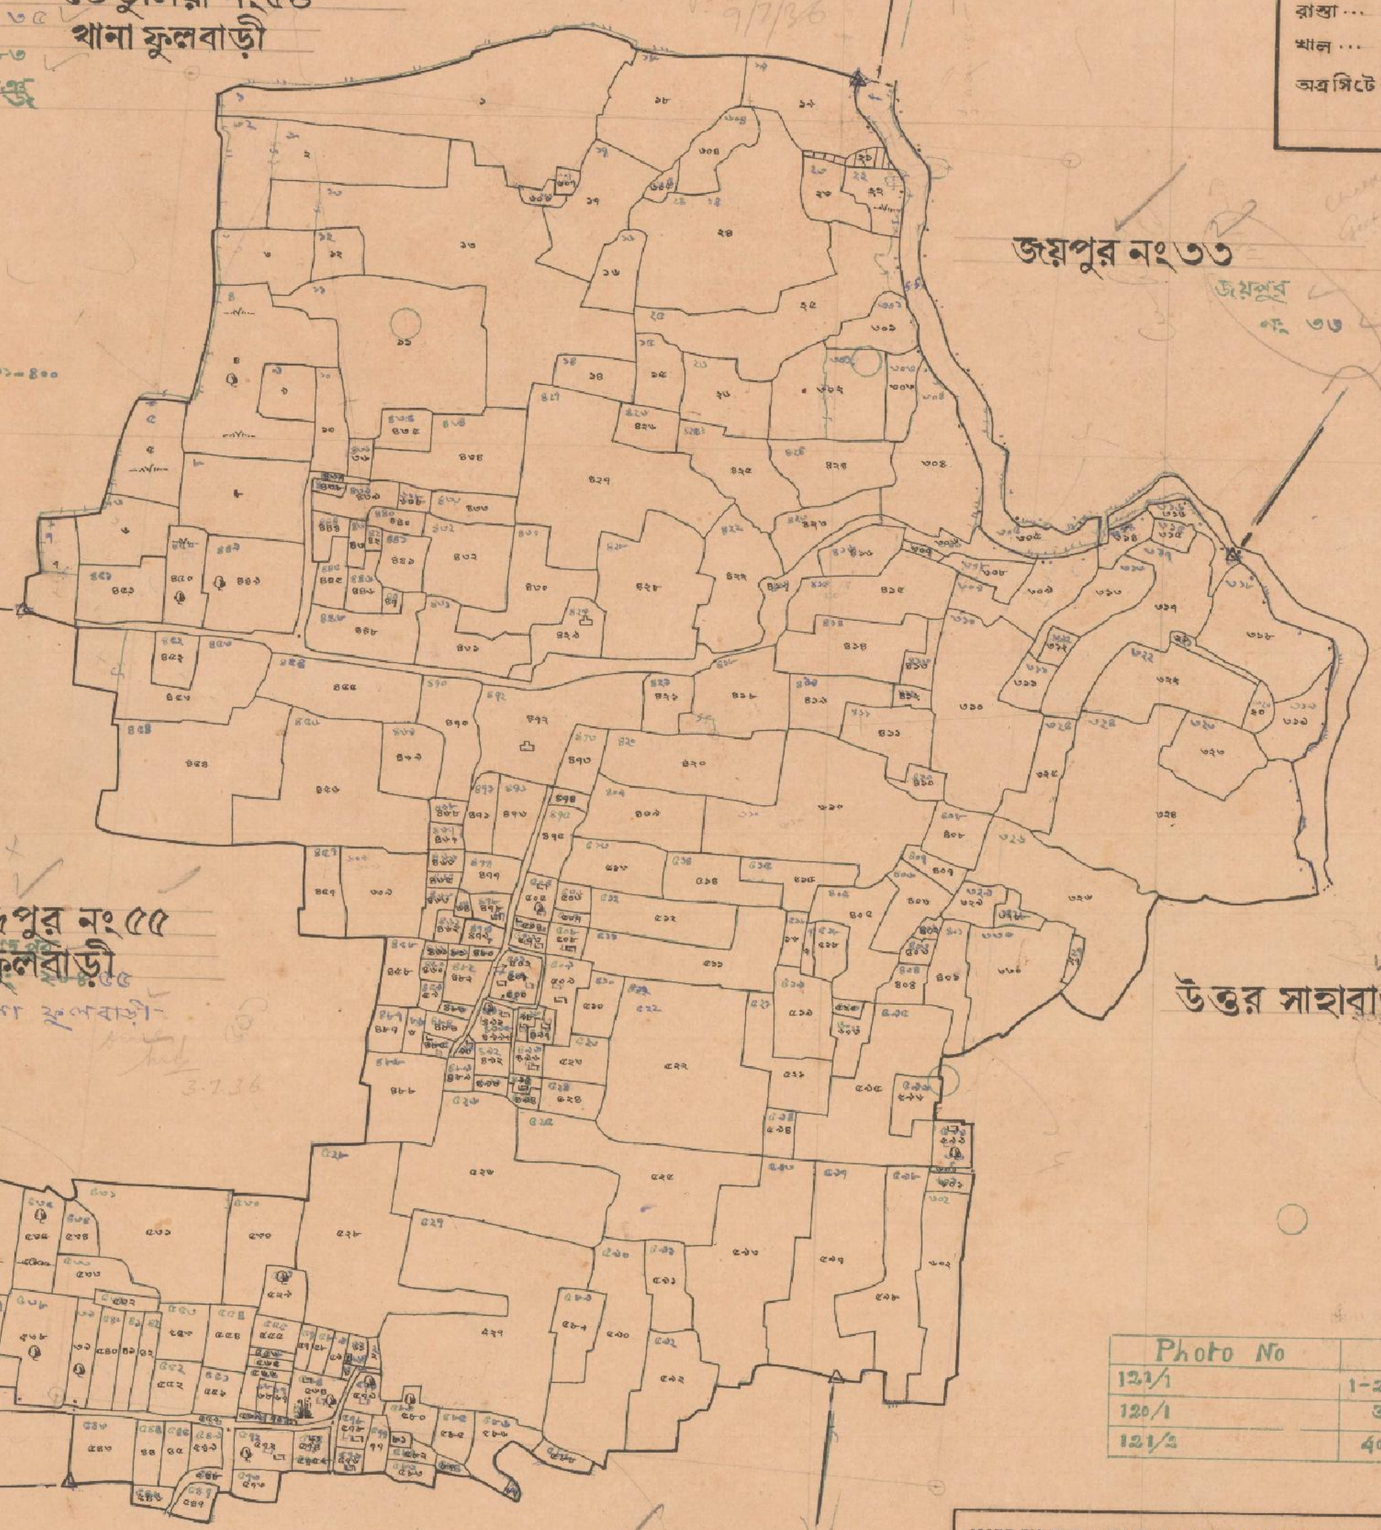

Photo No	Plot No
121/1	1-26. 604. 605
120/1	301-330
121/2	401-603

MADE BY THE AUTHORITY OF GOVERNMENT IN 1934-36

F.O. Bell

SETTLEMENT OFFICER AND SUPERINTENDENT OF SURVEY

ADOPTED FOR THE PURPOSE OF OPERATION UNDER CHAPTER IV OF THE E.B.S.A.& T.ACT, 1950, WITHOUT CORRECTION.

SETTLEMENT OFFICER & SUPERINTENDENT OF SURVEY.