জিলা দিনাজপুর

থানা বীরগঞ্জ

মৌজা চকমহাদেব (CHAK MAHADEB)

জে, এল, নং ১৩৭

রে, সা, নং ৬০৪৮, ৬০৪৯, ৬০৫০

স্কেল ১৬" = ১ মাইল

১০০ কড়িতে এক জরীপ,
৮০ জরীপে এক মাইল।

Kanungo	Kistwar Amin	Khanapuri Amin	Burhanal Kanungo	Survey Commenced	Survey Ended	Khanapuri Commenced	Khanapuri Ended	Burhanal Commenced
P.N. Adhikari		Hriday Ranjan Chaudhuri	P.N. Adhikari			16.11.35	7.12.35	25.2.36

সাঙ্কেতিক

দালান ...	
ত্রিসীমানার পিলার ...	
অন্যান্য পিলার ...	
লোহার পিলার ...	
ট্রাভার্স ষ্টেসন ...	
জি, টি, ষ্টেসন ...	
বেঞ্চমার্ক ...	
পাকা ইন্দারা ...	
নল কূপ ...	
পান বরজ ...	
দাগ নং	
পাকা সড়ক ...	
কাঁচা সড়ক ...	
রাস্তা ...	
খাল ...	
অত্রসিটে ভুক্ত ...	

ক ... মহাদেব পুর রে: সা: নং ৬০৪৮
খ ... বংশী জোত রে: সা: নং ৬০৪৯
গ ... রসুলপুর রে: সা: নং ৬০৫০

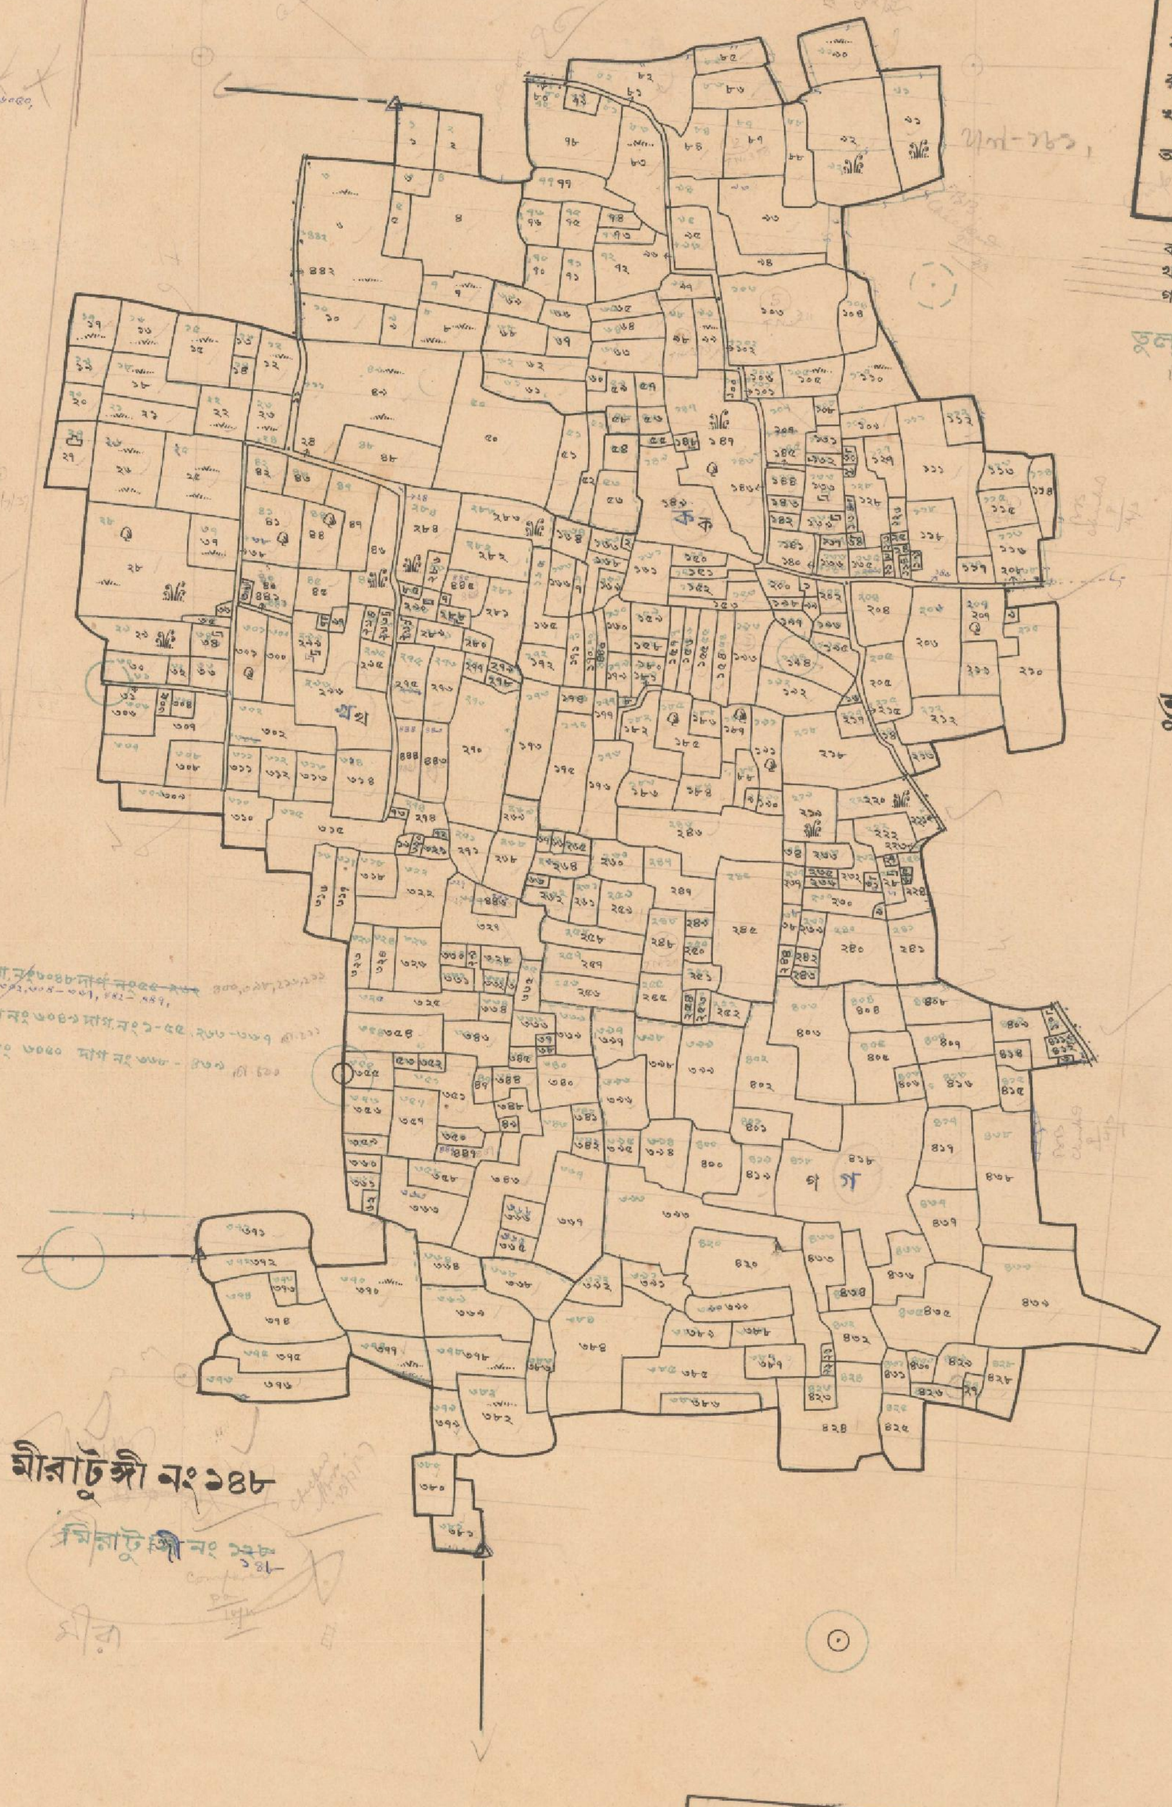

তুলশীপুর নং ১৩৮

মাটিয়াকুড়া নং ১৩৬

মীরাটুঙ্গী নং ১৪৮

ক মৌজা চকমহাদেব রে সা নং ৬০৪৮ দাগ নং ১-৫৫, ২৬৬-৩৬৭

খ মৌজা জোত বংশী রে সা নং ৬০৪৯ দাগ নং ১-৫৫, ২৬৬-৩৬৭

গ মৌজা রসুলপুর রে সা নং ৬০৫০ দাগ নং ৩৬৮-৪৬৭

MADE BY THE AUTHORITY OF GOVERNMENT IN 1935-37

Forbell

SETTLEMENT OFFICER AND SUPERINTENDENT OF SURVEY

ADOPTED FOR THE PURPOSE OF OPERATION UNDER CHAPTER IV OF THE E.B.S.A.& T.ACT, 1950, WITHOUT CORRECTION.

SETTLEMENT OFFICER & SUPERINTENDENT OF SURVEY.