জিলা দিনাজপুর

থানা নবাবগঞ্জ

মৌজা বিশাগড় (BISAGAR)

জে, এল, নং ১১১

রে, সা, নং ৪৫৫১

স্কেল ১৬" = ১ মাইল

১০০ কড়িতে এক জরীপ।
৮০ জরীপে এক মাইল।

NAME OF				SURVEY		KHANAPURI		BUJHARAT	
KANUNGO	RASTWAR AMIN	KHANAPURI AMIN	BUJHARAT KANUNGO	COMMENCED	ENDED	COMMENCED	ENDED	COMMENCED	ENDED
		Md. Azgam	J. C. Bhattacharjee			2. 2. 3			

সাঙ্কেতিক

দালান	...	...
ত্রিসীমানার পিলার	...	...
অন্যান্য পিলার	...	...
লোহার পিলার	...	...
ট্রাভার্স ষ্টেসন	...	...
জি, টি, ষ্টেসন	...	...
বেঞ্চমার্ক	...	...
পাকা ইন্দারা	...	...
নল কূপ	...	...
পান বরজ	...	...
	দাগ নং	
পাকা সড়ক	...	...
কাঁচা সড়ক	...	...
রাস্তা	...	...
খাল	...	...
অত্রমিটে ভুক্ত	...	...

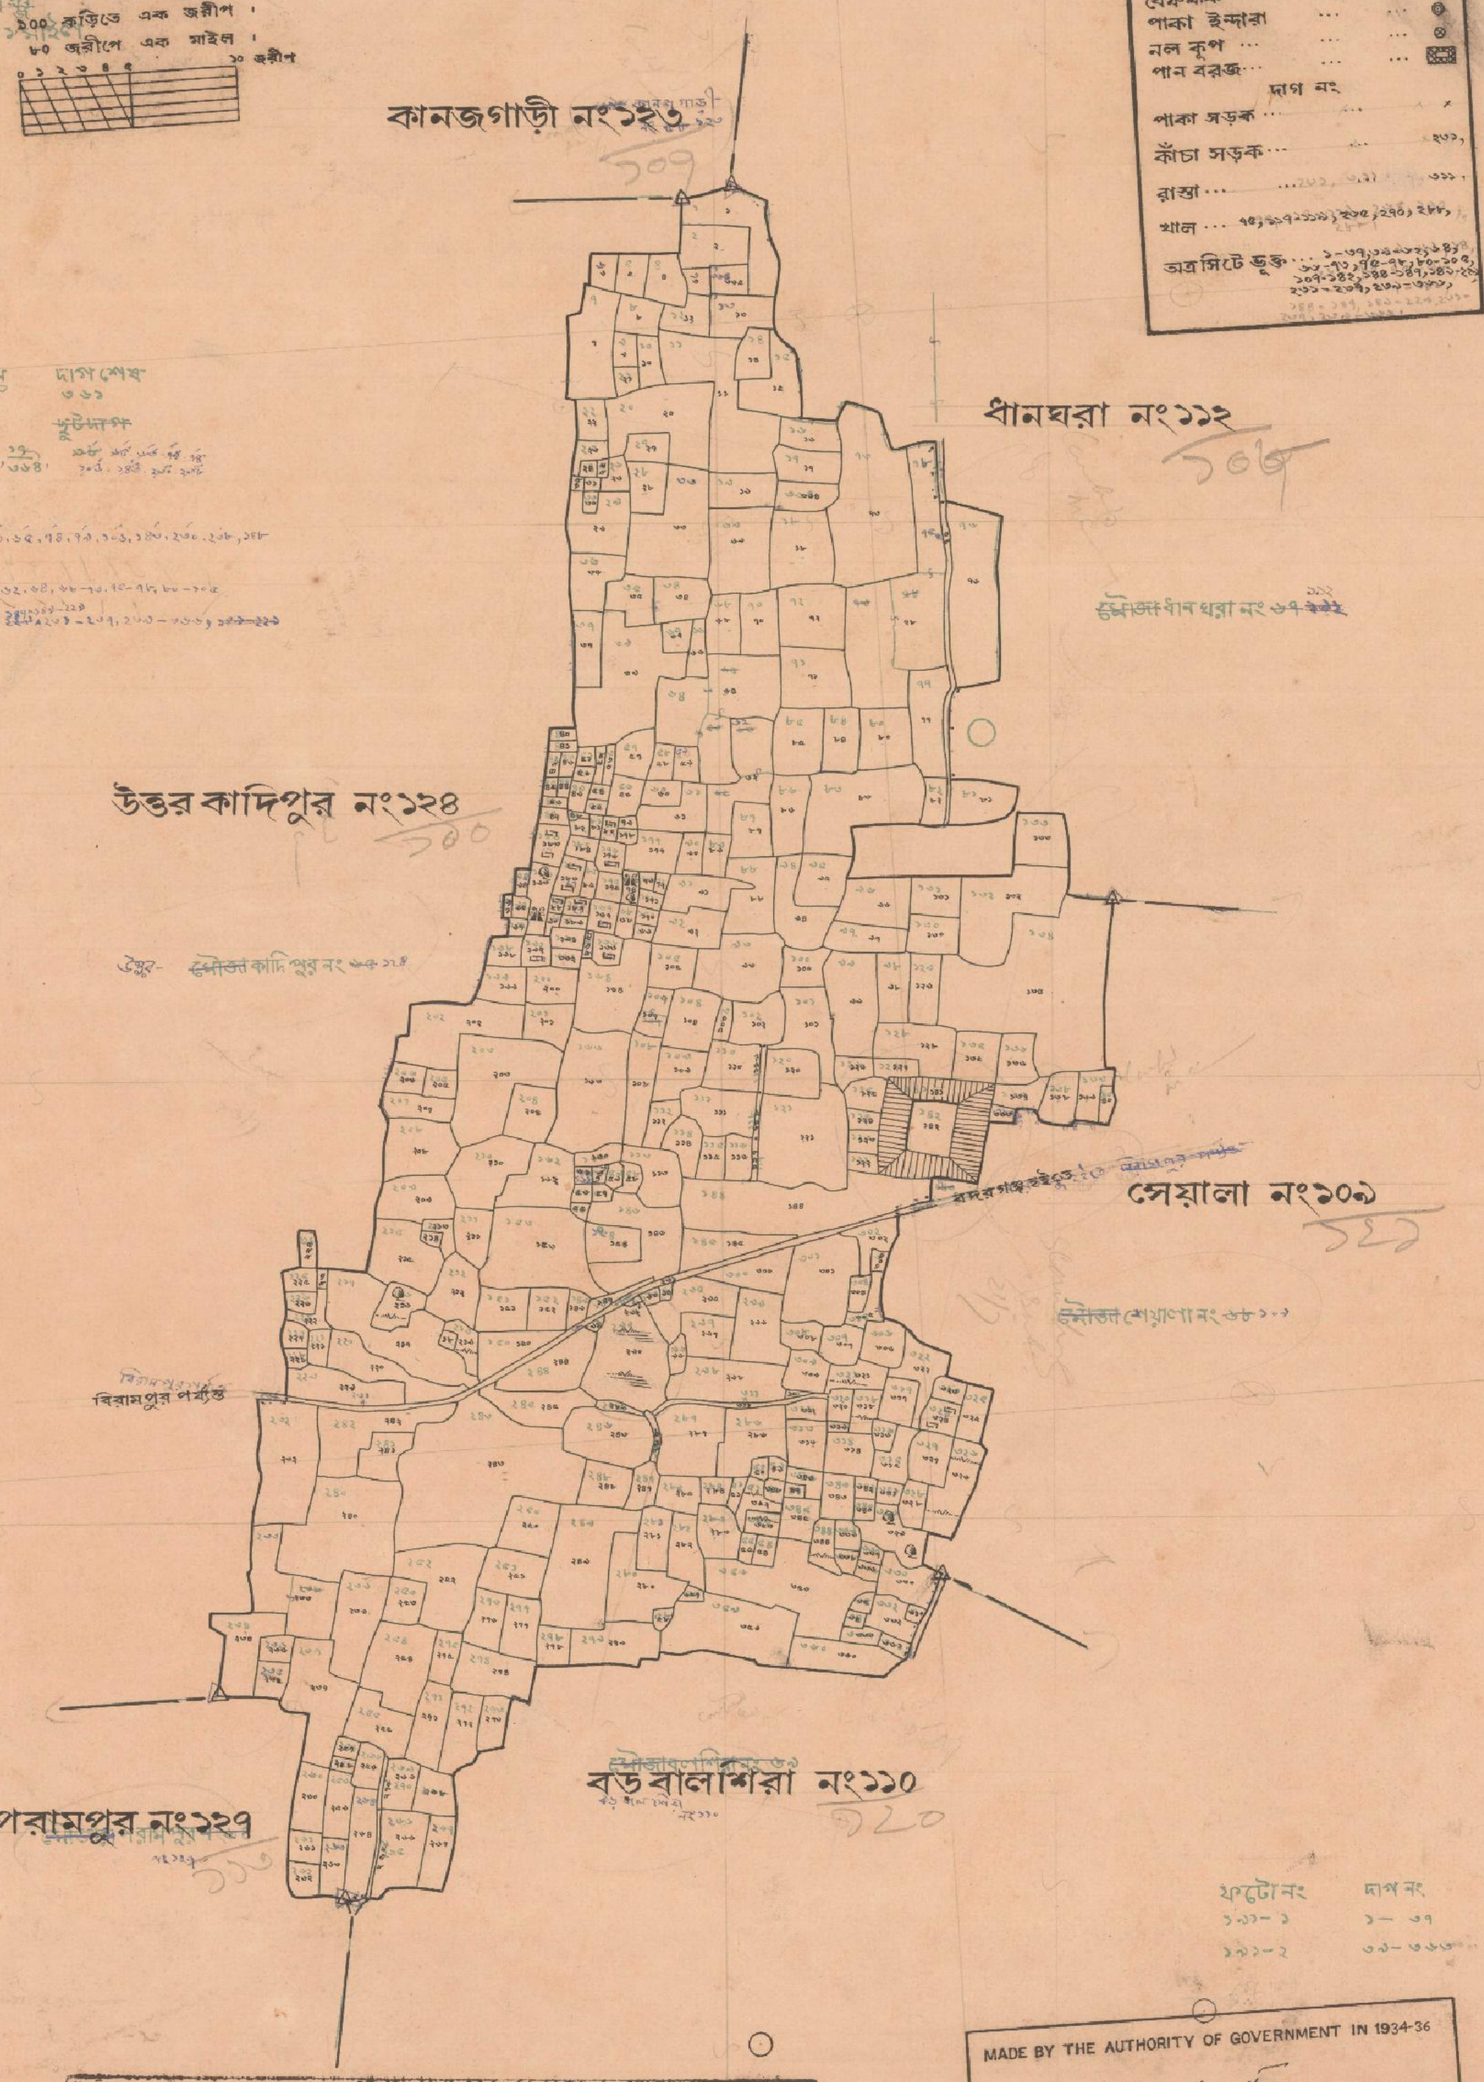

NAME OF MAUZA	R.S. J.L. No	G.T. J.L. No	P.S.	REM.
বিশাগড়	১১১	১০৯		
কানজগাড়ী	১২৩	১০৭		
ধানঘরা	১১২	১০৮		
উত্তর কাদিরপুর	১২৪	১১০		
রূপরামপুর	১২৭	১১৩		
বড়বালশিরা	১১০	১২০		
সেয়ালা	১০৯	১২১		

ফটো নং	দাগ নং
১-১১-১	১- ৩৭
১-১১-২	৩৯- ৩৬৩

MADE BY THE AUTHORITY OF GOVERNMENT IN 1934-36

SETTLEMENT OFFICER AND SUPERINTENDENT OF SURVEY

ADOPTED FOR THE PURPOSE OF OPERATION UNDER CHAPTER IV OF THE C.S.&A.R. ACT, 1950, WITHOUT CORRECTION.

SETTLEMENT OFFICER & SUPERINTENDENT OF SURVEY.