জিলা দিনাজপুর

থানা বোচাগঞ্জ

মৌজা মোল্লাপাড়া সিটনং১(MOLLÀPÀRÀ)

জে, এল, নং ১০১

রে, সা, নং ৭১

স্কেল ১৬" = ১ মাইল

১০০ কড়িতে এক জরীপ।

৮০ জরীপে এক মাইল।

০ ১ ২ ৩ ৪ ৫ ১০ জরীপ।

Name of Kanungo	Kistwar	Amin	Khanapuri	Amin	Bujharat	Kgo.	Kistwar Commenced	Kistwar Ended	Khanapuri Commenced	Khanapuri Ended	Bujharat Commenced	Bujharat Ended
S. K. Chakraborty			Mafiz uddin Mahmud		S. K. Chakraborty		30. 11. 35	30. 11. 35	3.11. 35		13. 4. 36	

সাঙ্কেতিক

দালান	...	...
কাঁচাঘর	...	...
কবর স্থান	...	...
ইন্দারা	...	...
নলকূপ	...	...
পান বরজ	...	...
জঙ্গল	...	...
ঝোপ	...	...
পুরাতন পতিত	...	...
লটা ঘাস	...	...
তাল গাছ	...	...
খেজুর গাছ	...	...
নারিকেল গাছ	...	...
সুপারী গাছ	...	...
আম গাছ	...	...
শাল গাছ	...	...
বিল	...	...
বাঁশঝাড়	...	...
পাকা সড়ক	...	...
কাঁচা সড়ক	...	...

রাস্তা ... ৬, ৭৮, ১২৫, ১৭০, ৪৬৭, ৫৫৩, ৫৬০, ৫৬২, ৭৬৫, ৫৮৭, ৬১৮, ৬৬১, ৬৬৮, ৬৮৬, ৭৬১

খাল ... ২৪৭, ৪৬০, ৫৭৮, ৫৮০, ৫৮২, ৭৫৫,

অত্র সিটে ভুক্ত ... ১-১২৭, ১৬২-১৯৬, ১৬৫-২২৯, ২৬১-৩৫৭, ৩৫৭-৪৩৩, ৪১৮-৪৬৯, ৪৬৮-২৭৪, ২৭৭-৩৭৬, ৬১৫-৬২৫, ৭১৮-৭৫৭, ৭৬১, ৭৬২, ৭৬৪-৮০১,

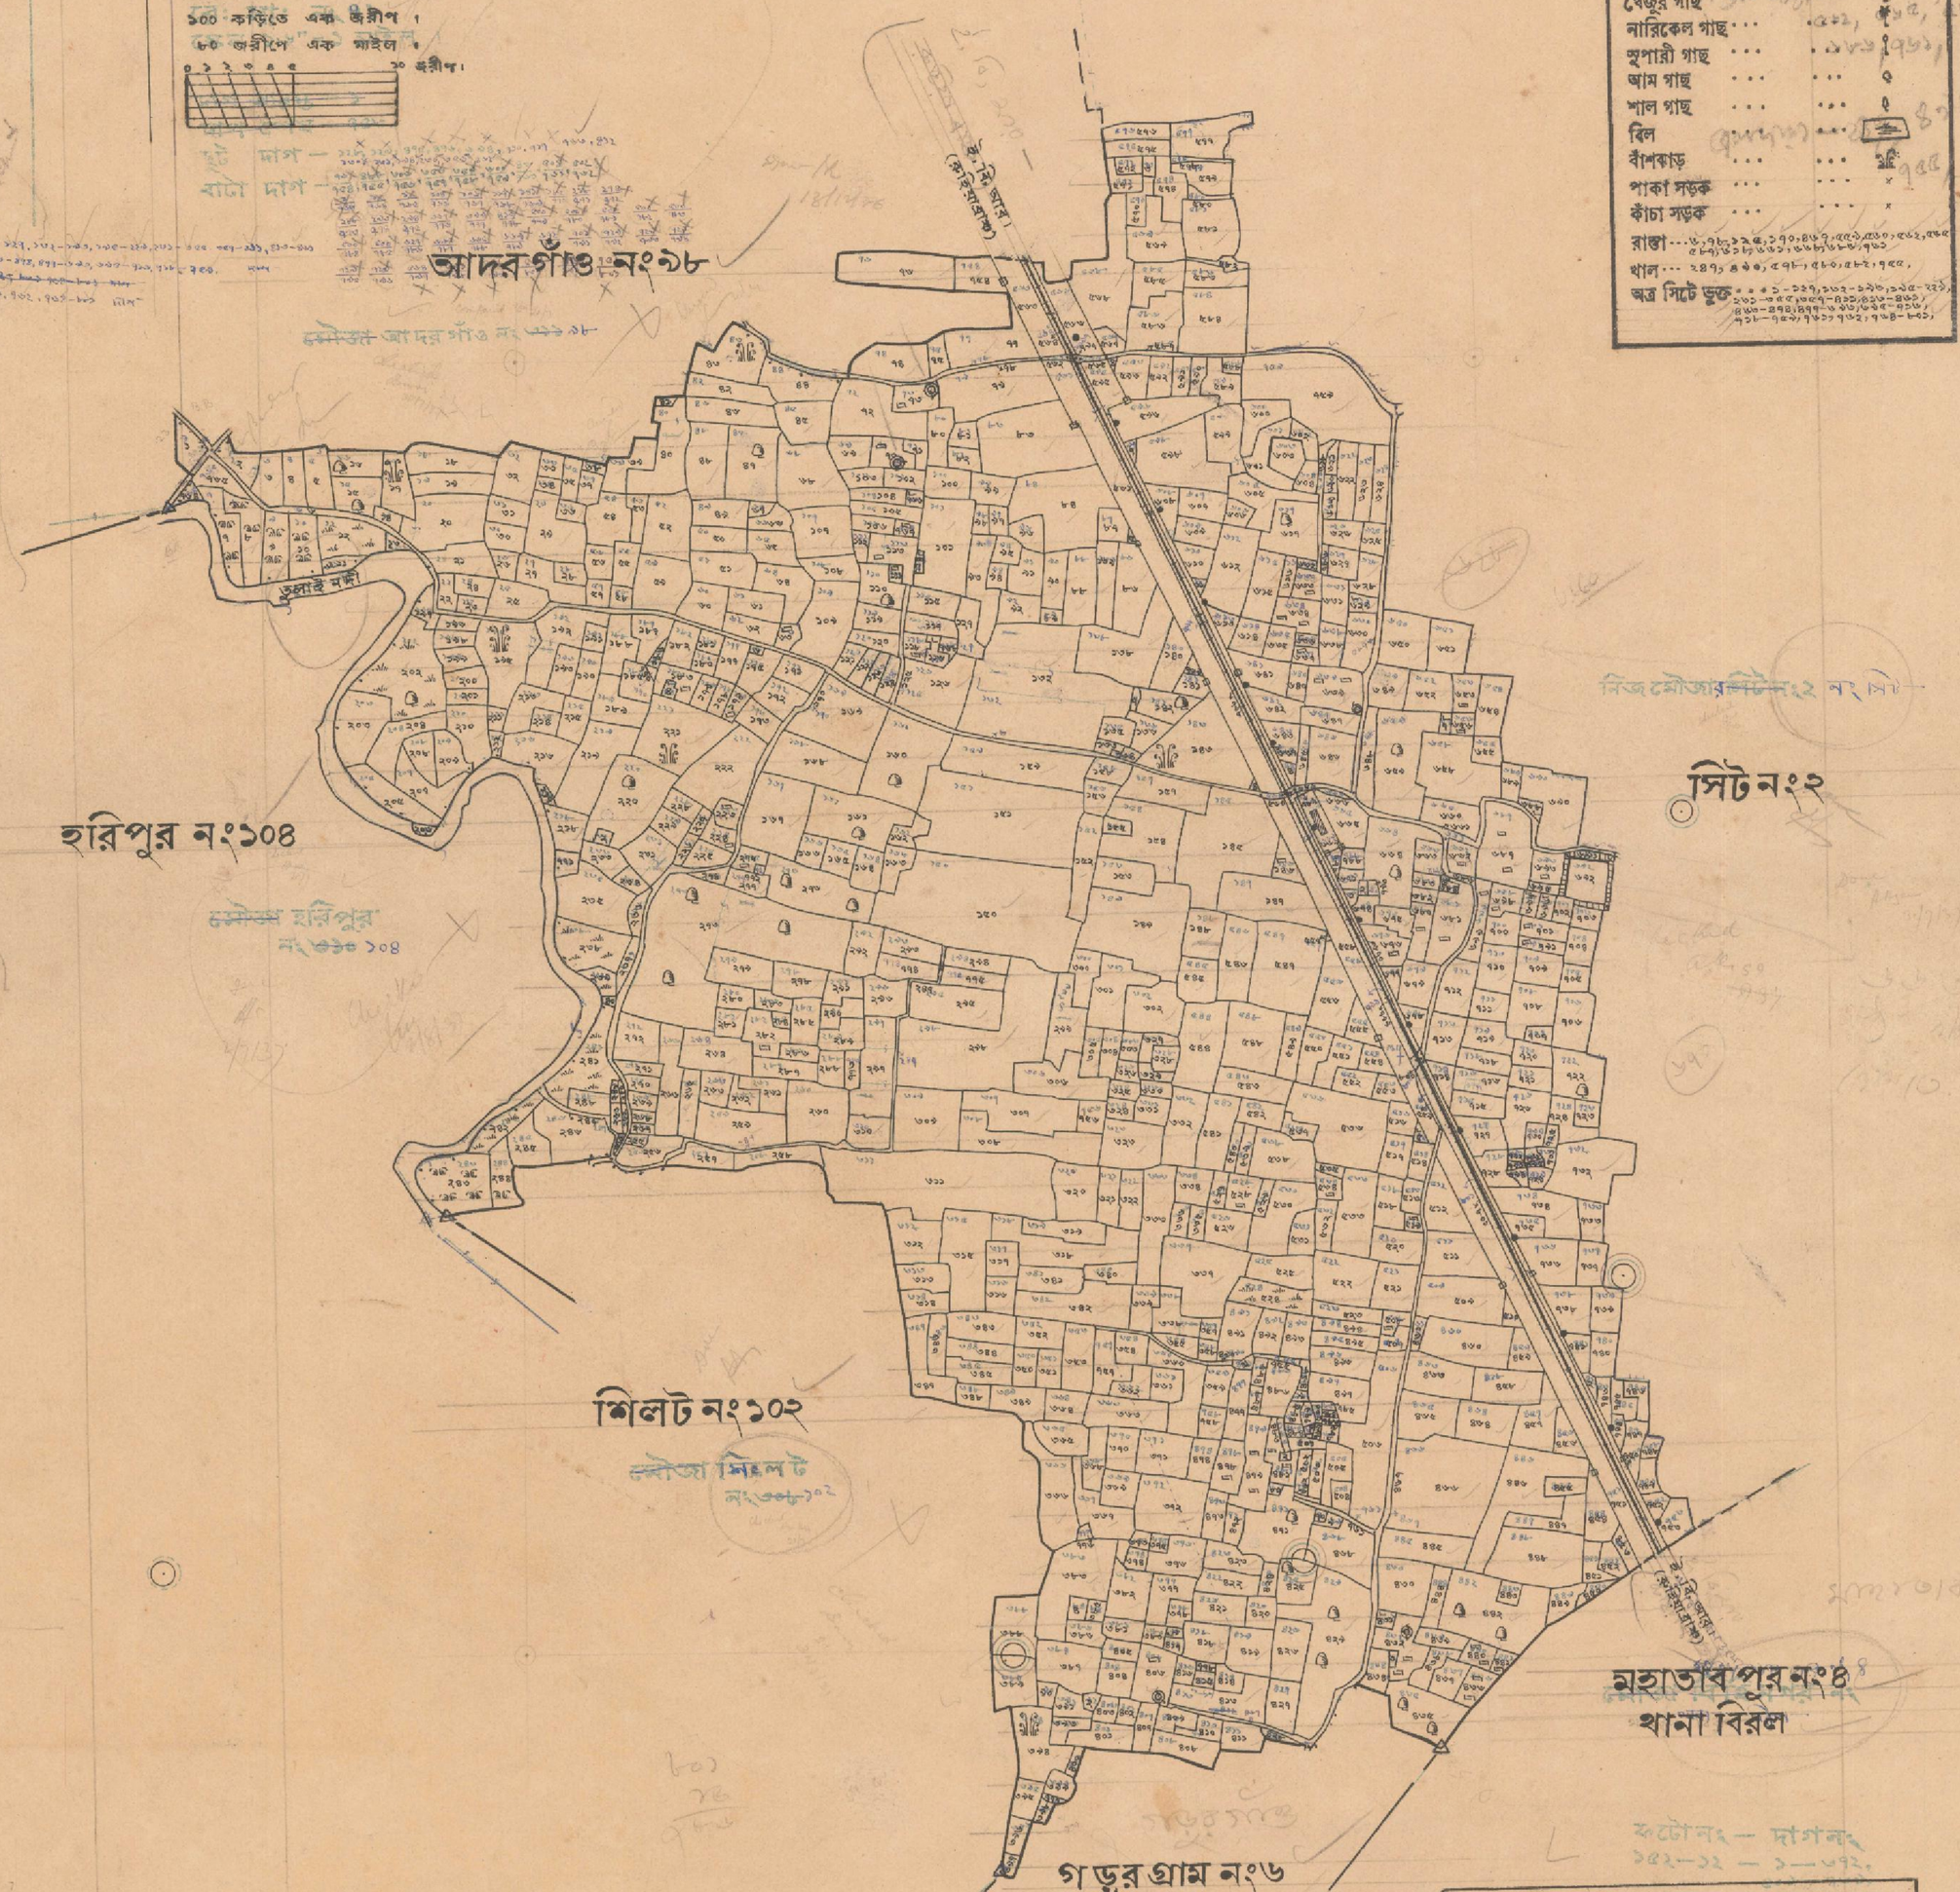

MADE BY THE AUTHORITY OF GOVERNMENT IN 1965-67

F. O'Bell

SETTLEMENT OFFICER AND SUPERINTENDENT OF SURVEY

ADOPTED FOR THE PURPOSE OF OPERATION UNDER CHAPTER IV OF THE E.B.S.A.& T.ACT, 1950, WITHOUT CORRECTION.

SETTLEMENT OFFICER & SUPERINTENDENT OF SURVEY.