জিলা দিনাজপুর

থানা নবাবগঞ্জ

মৌজা ঘোনাবিছানা (GHONĀ BICHHĀNĀ)

জে, এল, নং ১৮৫

রে, সা, নং ৫৪৩০

স্কেল ১৬" = ১ মাইল

১০০ কড়িতে এক জরীপ।
৮০ জরীপে এক মাইল।

০ ১ ২ ৩ ৪ ৫ ১০ জরীপ

Name of Karungo	Kist. Amin	Khana Amin	Bujharat Kgo	Survey Commenced	Survey Ended	Khanapuri Commenced	Khanapuri Ended	Bujharat Commenced	Bujharat Ended
Islam	A. Razzak	A. Razzak	S. Amin	8. 2. 35	1. 3. 35	8. 2. 35	1. 3. 35	12. 6. 35	[illegible]

সাঙ্কেতিক

দালান	
ত্রিসীমানার পিলার	△
অন্যান্য পিলার	□
লোহার পিলার	↓
ট্রাভার্স ষ্টেসন	○
জি, টি, ষ্টেসন	△
বেঞ্চমার্ক	
পাকা ইন্দারা	
নল কূপ	
পান বরজ	
দাগ নং	
পাকা সড়ক	×
কাঁচা সড়ক	×
রাস্তা ... ৩৩৭, ৩৪৩, ৩৩১, ৪০৫,	
খাল ... ২০২, ২১৮, ৪১২, ৬৫৩,	
অত্রসিটে ভুক্ত ... ৩৫, ২০১, ২০২, ২০৫, ২০৬-২১১, ২১৬, ২১৫-২৫৪, ২৫৬-২৫৮, ৩০১-৩১৩, ৩৬৮-৩৮৪, ৩৮৬-৪১০, ৪১২-৪২০, ৪২২-৪২৯, ৩০১-৩০৩, ৩০৮-৩৪৯, ৩৫১-৩৬৭, ৩৭৭-৭৩১।	

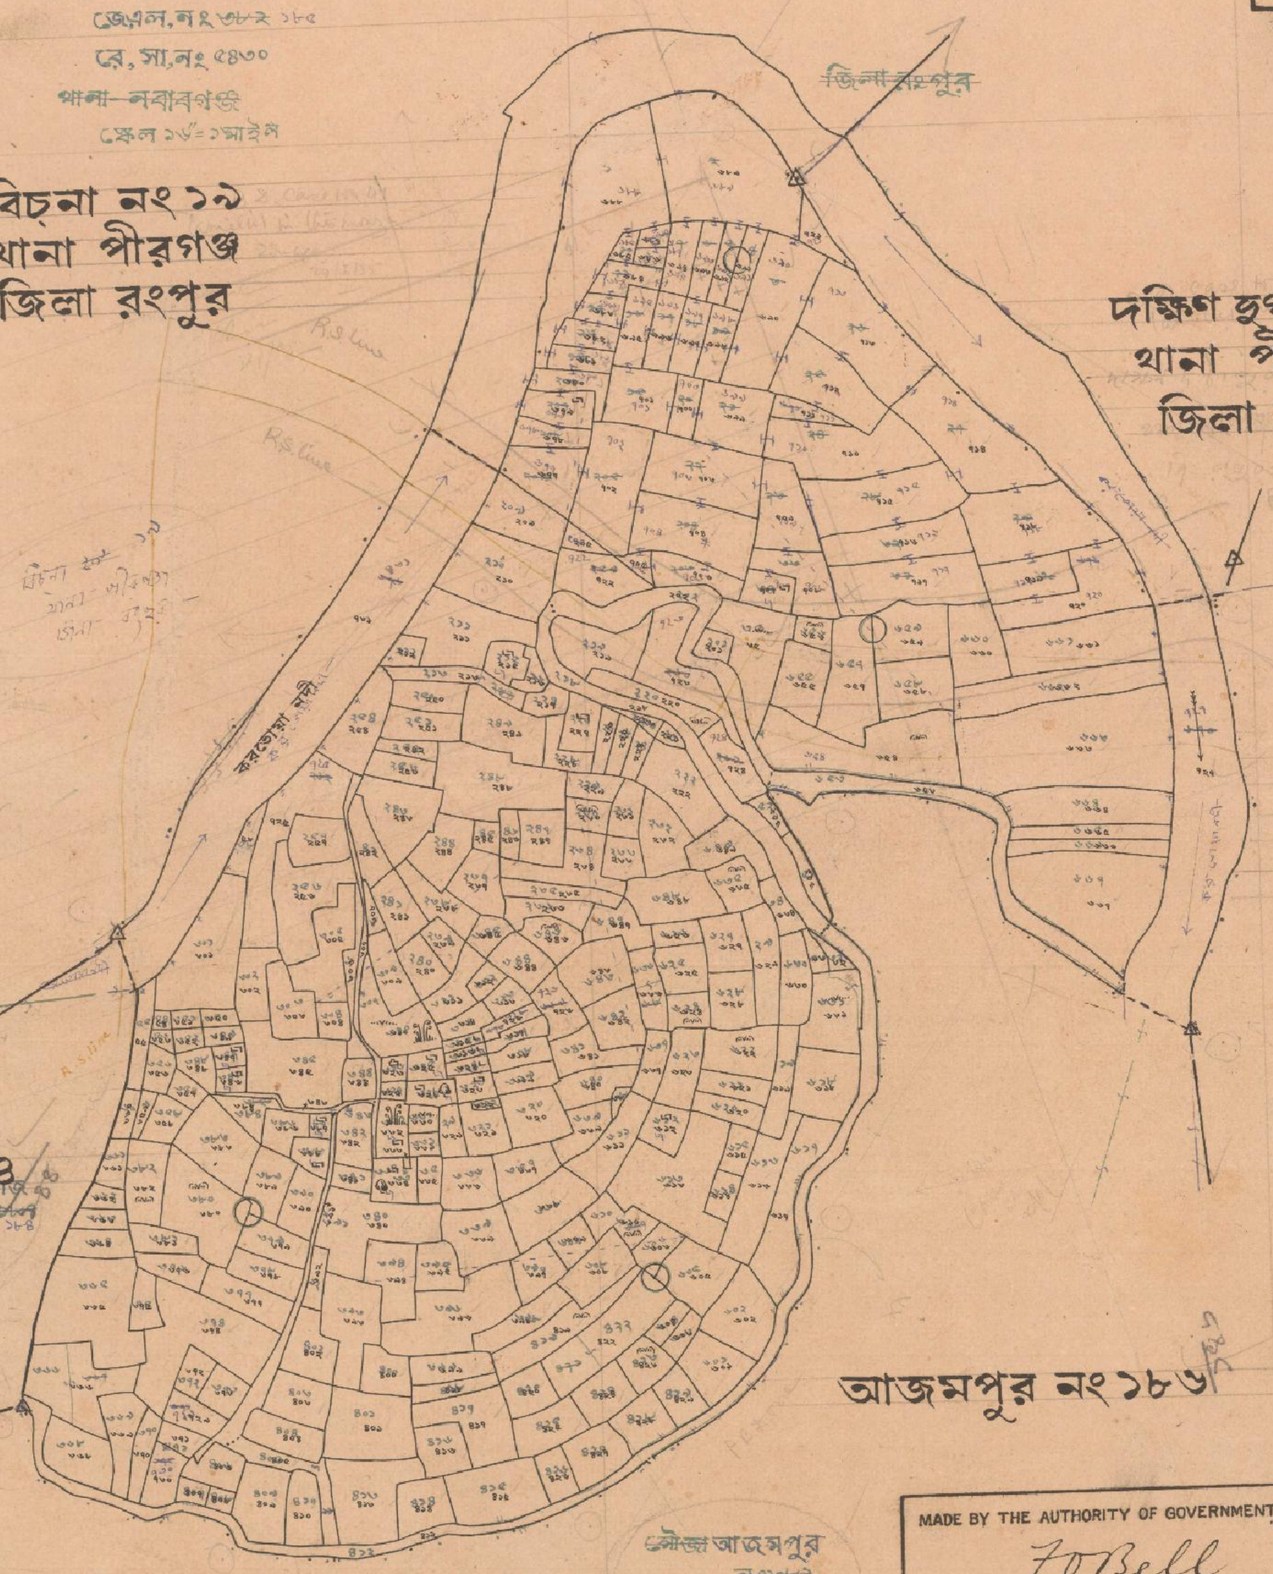

MADE BY THE AUTHORITY OF GOVERNMENT IN 1934-38
F.O. Bell
SETTLEMENT OFFICER AND SUPERINTENDENT OF SURVEY

NAME OF MOUZA	OLD J.L.NO	NEW J.L.NO	P.S.	DIST.
ঘোনাবিছানা	১৮৫	১৪৫	নবাবগঞ্জ	দিনাজপুর
সিরাজ	১৮৪	১৪৪	ঐ	ঐ
আজমপুর	১৮৬	১৪৬	ঐ	ঐ
তিওরমারী	৩০	৩০	পীরগঞ্জ	রংপুর
দক্ষিন দুর্গাপুর	২৯	২৯	ঐ	ঐ
বিচনা	১৯	১৯	ঐ	ঐ

ADOPTED FOR THE PURPOSE OF OPERATION UNDER CHAPTER IV OF THE B.B.S.A.& T.ACT, 1950, WITHOUT CORRECTION.
Islam
SETTLEMENT OFFICER & SUPERINTENDENT OF SURVEY.