NAME OF				SURVEY		KHANAPURI		BUJHARAT	
KANUNGO	KISTWAR AMIN	KHANAPURI AMIN	BUJHARAT KANUNGO	COMMENCED	ENDED	COMMENCED	ENDED	COMMENCED	ENDED
J.C. Bhattacharjee		Arshad ulla	J.C. Bhattacharjee			22.1.35	16.2.35	18.4.35	17.5.35

জিলা দিনাজপুর

থানা নবাবগঞ্জ

মৌজা ধানঘরা (DHANGHARA)

জে, এল, নং ১১২

রে, সা, নং ৪৫৫০

স্কেল ১৬" = ১ মাইল

১০০ কড়িতে এক জরীপ।

৮০ জরীপে এক মাইল।

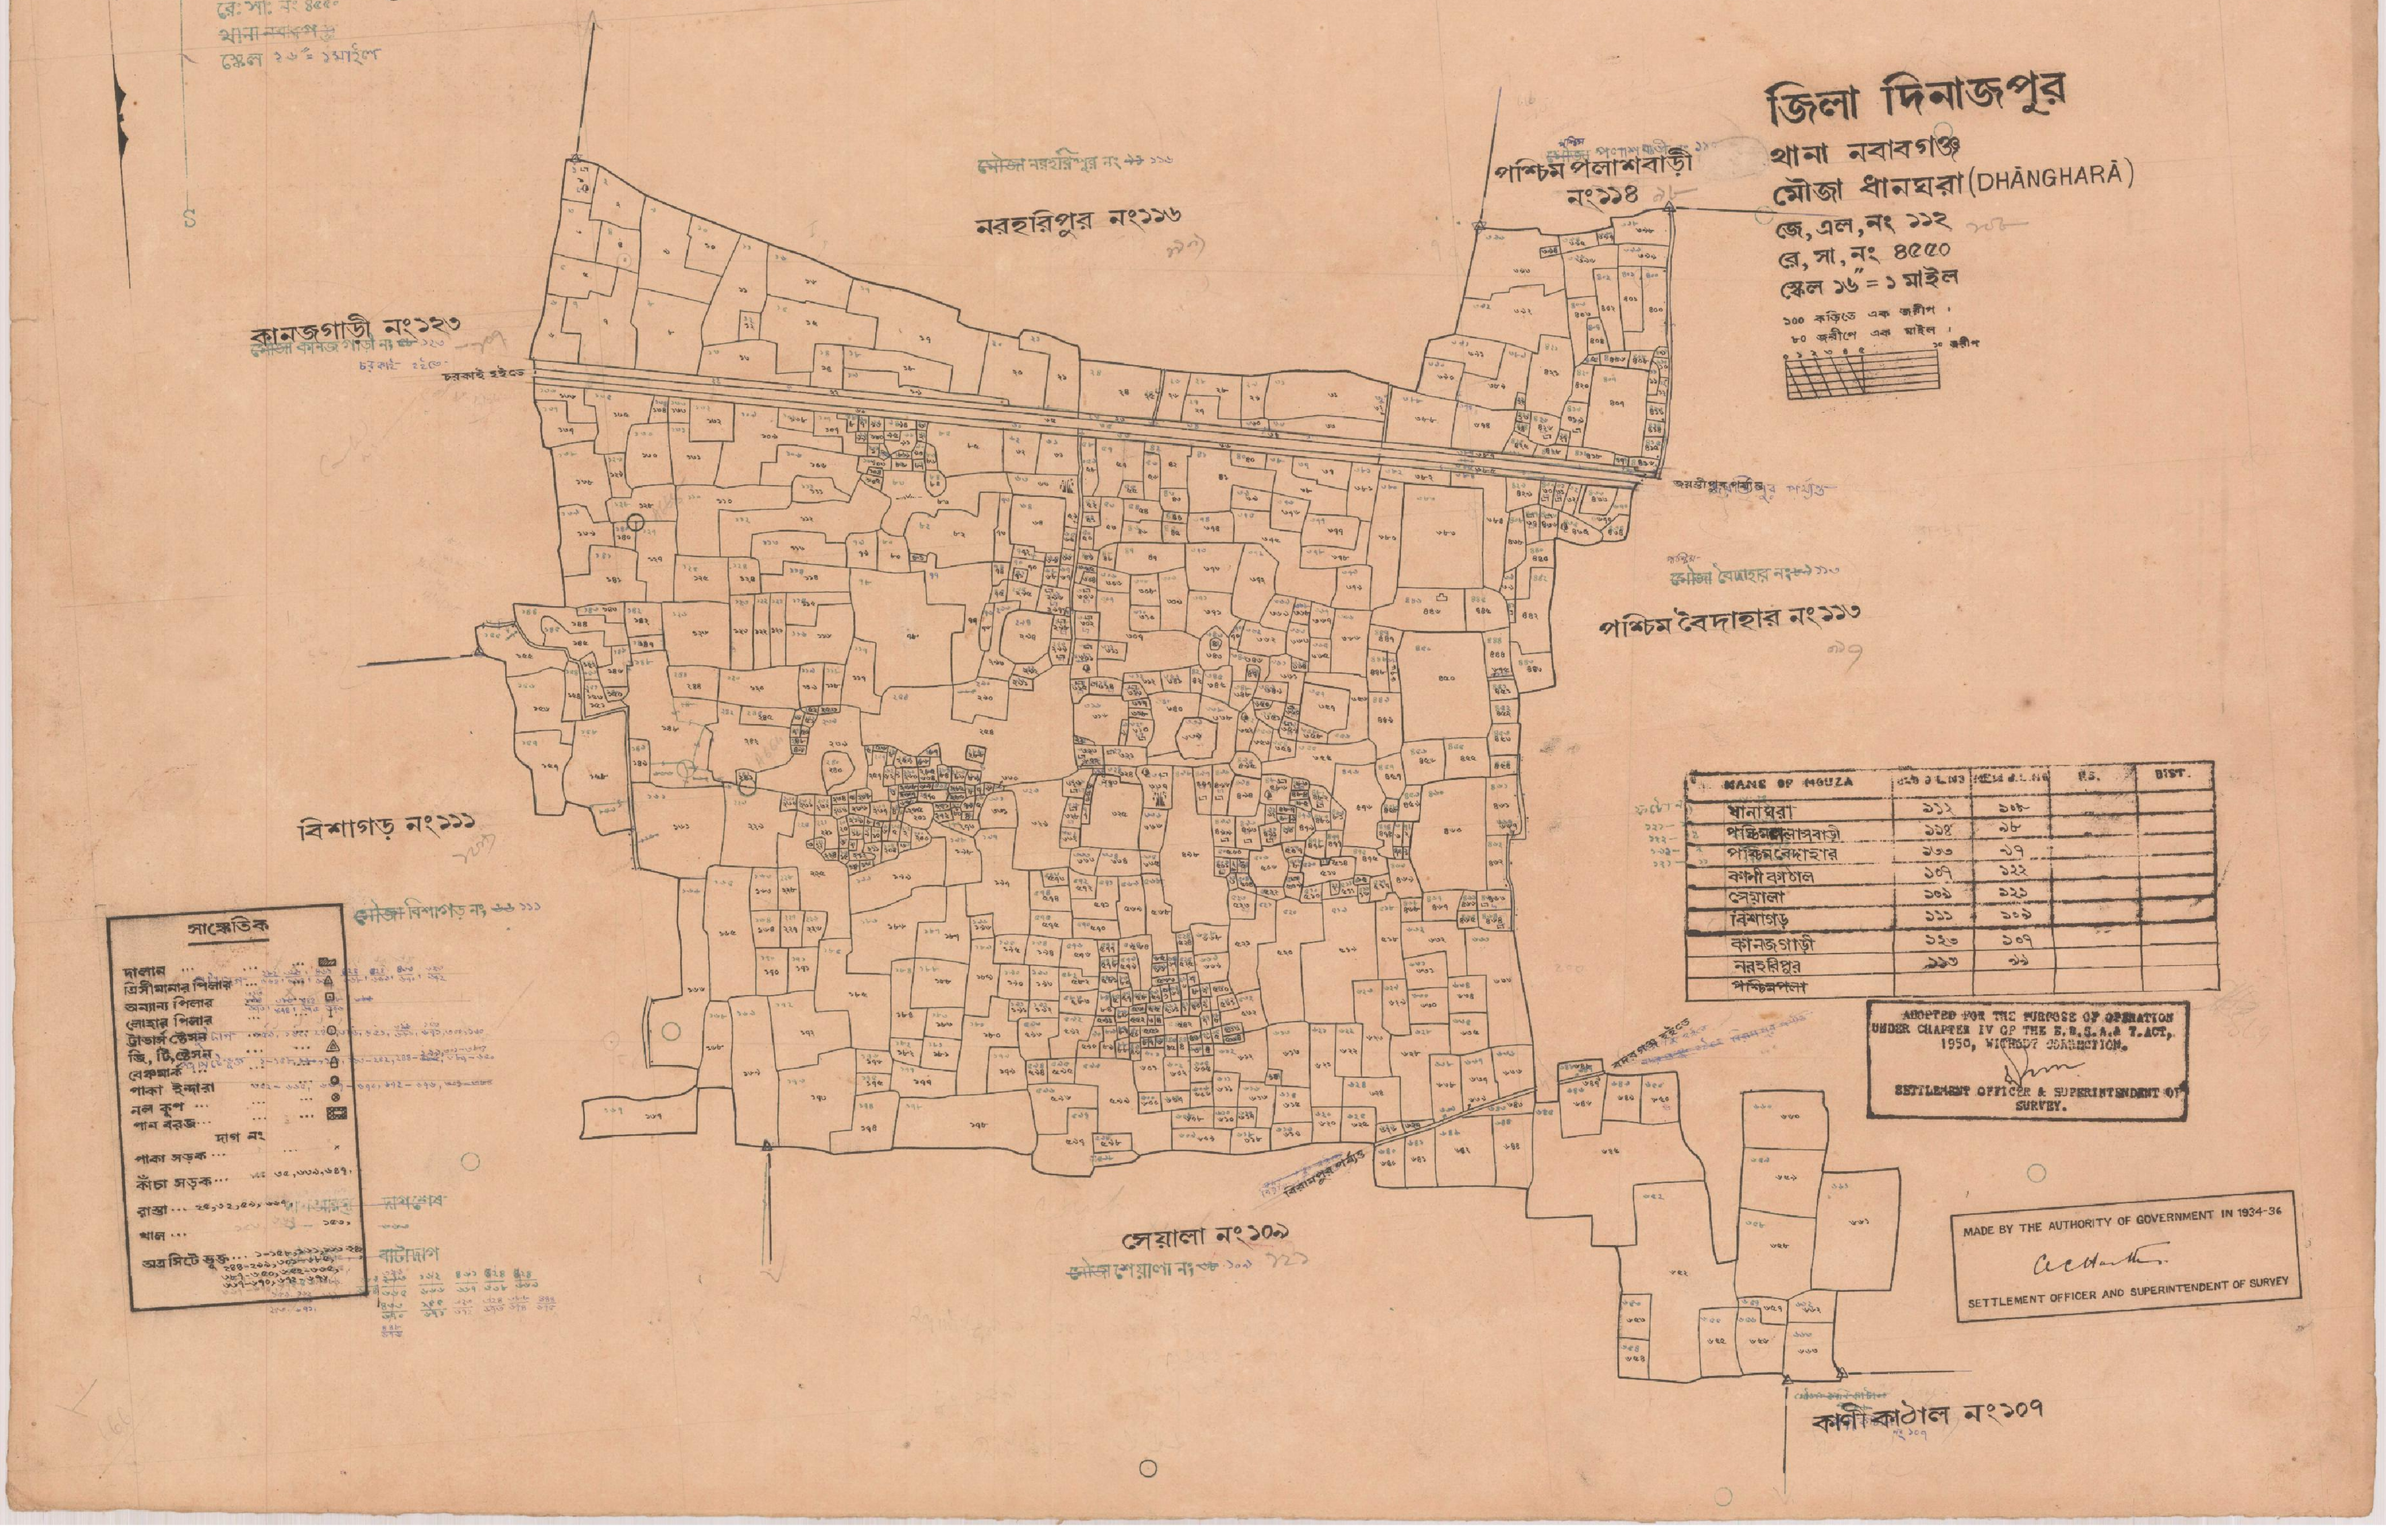

NAME OF MOUZA	OLD J.L.NO	NEW J.L.NO	R.S.	DIST.
ধানঘরা	১১২	১০৮		
পশ্চিমপলাশবাড়ী	১১৪	১৮		
পশ্চিমবৈদাহার	১১৩	১৭		
কালীকাঠাল	১০৭	১২২		
সেয়ালা	১০৯	১২১		
বিশাগড়	১১১	১১৯		
কানজগাড়ী	১২৩	১০৭		
নরহরিপুর	১১৬	১১		
পশ্চিমপলা				

ADOPTED FOR THE PURPOSE OF OPERATION UNDER CHAPTER IV OF THE B.T.A.A. & T. ACT, 1950, WITHOUT JURISDICTION.

SETTLEMENT OFFICER & SUPERINTENDENT OF SURVEY.

MADE BY THE AUTHORITY OF GOVERNMENT IN 1934-36

SETTLEMENT OFFICER AND SUPERINTENDENT OF SURVEY