জিলা দিনাজপুর

থানা ফুলবাড়ী

মৌজা ভেটাই (BHETAI)

জে, এল, নং ৪১

রে, সা, নং ৫০৯২, ৫০৯৩

স্কেল ১৬" = ১ মাইল

১০০ কড়িতে এক জরীপ।

৮০ জরীপে এক মাইল।

Survey				Revisional				Bujharat			
Name	Kishwar Amin	Bujharat Karanga	Commenced	Ended	Commenced	Ended	Commenced	Ended	Commenced	Ended
A. Huq	Mir Mobarak ali	Abdul Qani			16.1.35.	15.2.35.				
Abdul Qani	Abdul Qani	Kali Charan					26.4.35	27.4.35		

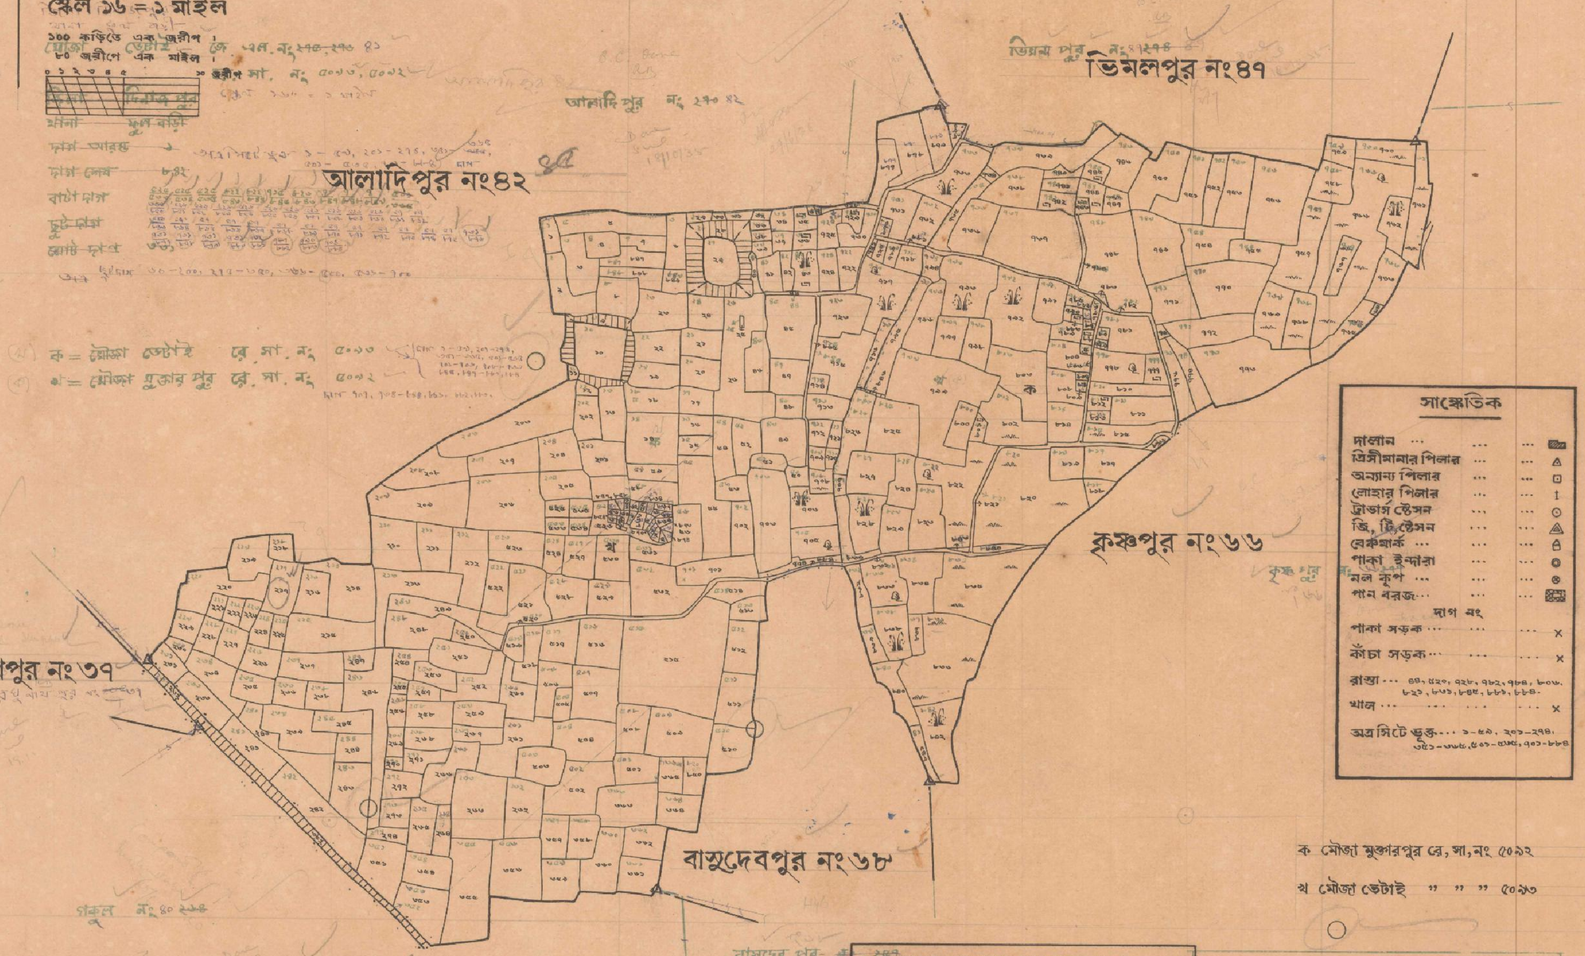

ক = মৌজা ভেটাই রে. সা. নং ৫০৯৩

খ = মৌজা মুক্তার পুর রে. সা. নং ৫০৯২

সাঙ্কেতিক

দালান	
ত্রিসীমানার পিলার	△
অন্যান্য পিলার	⊡
লোহার পিলার	1
ট্রাভার্স ষ্টেসন	⊙
জি, টি, ষ্টেসন	△
বেঞ্চমার্ক	
পাকা ইন্দারা	
নল কূপ	
পান বরজ	
দাগ নং	
পাকা সড়ক	×
কাঁচা সড়ক	×
রাস্তা ... ৩৯, ৫২৯, ৭২৮, ৭৮২, ৭৮৪, ৮০৬, ৮২১, ৮৬১, ৮৪৫, ৮৮১, ৮৮৪.	
খাল	×
অব্রজিটে ভুক্ত ... ১-৫৯, ২০১-২৭৪, ৬৫১-৬৬৬, ৫০১-৫৩৬, ৭০১-৮৮৪	

ক মৌজা মুক্তারপুর রে, সা, নং ৫০৯২

খ মৌজা ভেটাই " " " ৫০৯৩

MADE BY THE AUTHORITY OF GOVERNMENT IN 1934-36

F.O. Bell

SETTLEMENT OFFICER AND SUPERINTENDENT OF SURVEY

Bhatai J.L. No 275 278

Photo No	Sheet No	Plot No	Remark
125—3	1	351—364	
125—2		201—274 501—532	
124—1		1—53 701—842	

ADOPTED FOR THE PURPOSE OF OPERATION UNDER CHAPTER IV OF THE E.B.S.A.& T.ACT, 1950, WITHOUT CORRECTION.

SETTLEMENT OFFICER & SUPERINTENDENT OF SURVEY.

NAME OF MOUZA	OLD J.L.NO	NEW J.L.NO	P.S.	DIST.
ভেটাই	৪১	৫১		
আলাদিপুর	৪২	৪৫		
ভিমলপুর	৪৭	৫০		
কৃষ্ণপুর	৬৬	৫২		
বাসুদেবপুর	৬৮	৭২		
গকুল	৪০	৭৩		
উত্তর রঘুনাথপুর	৩৭	৪৪		